




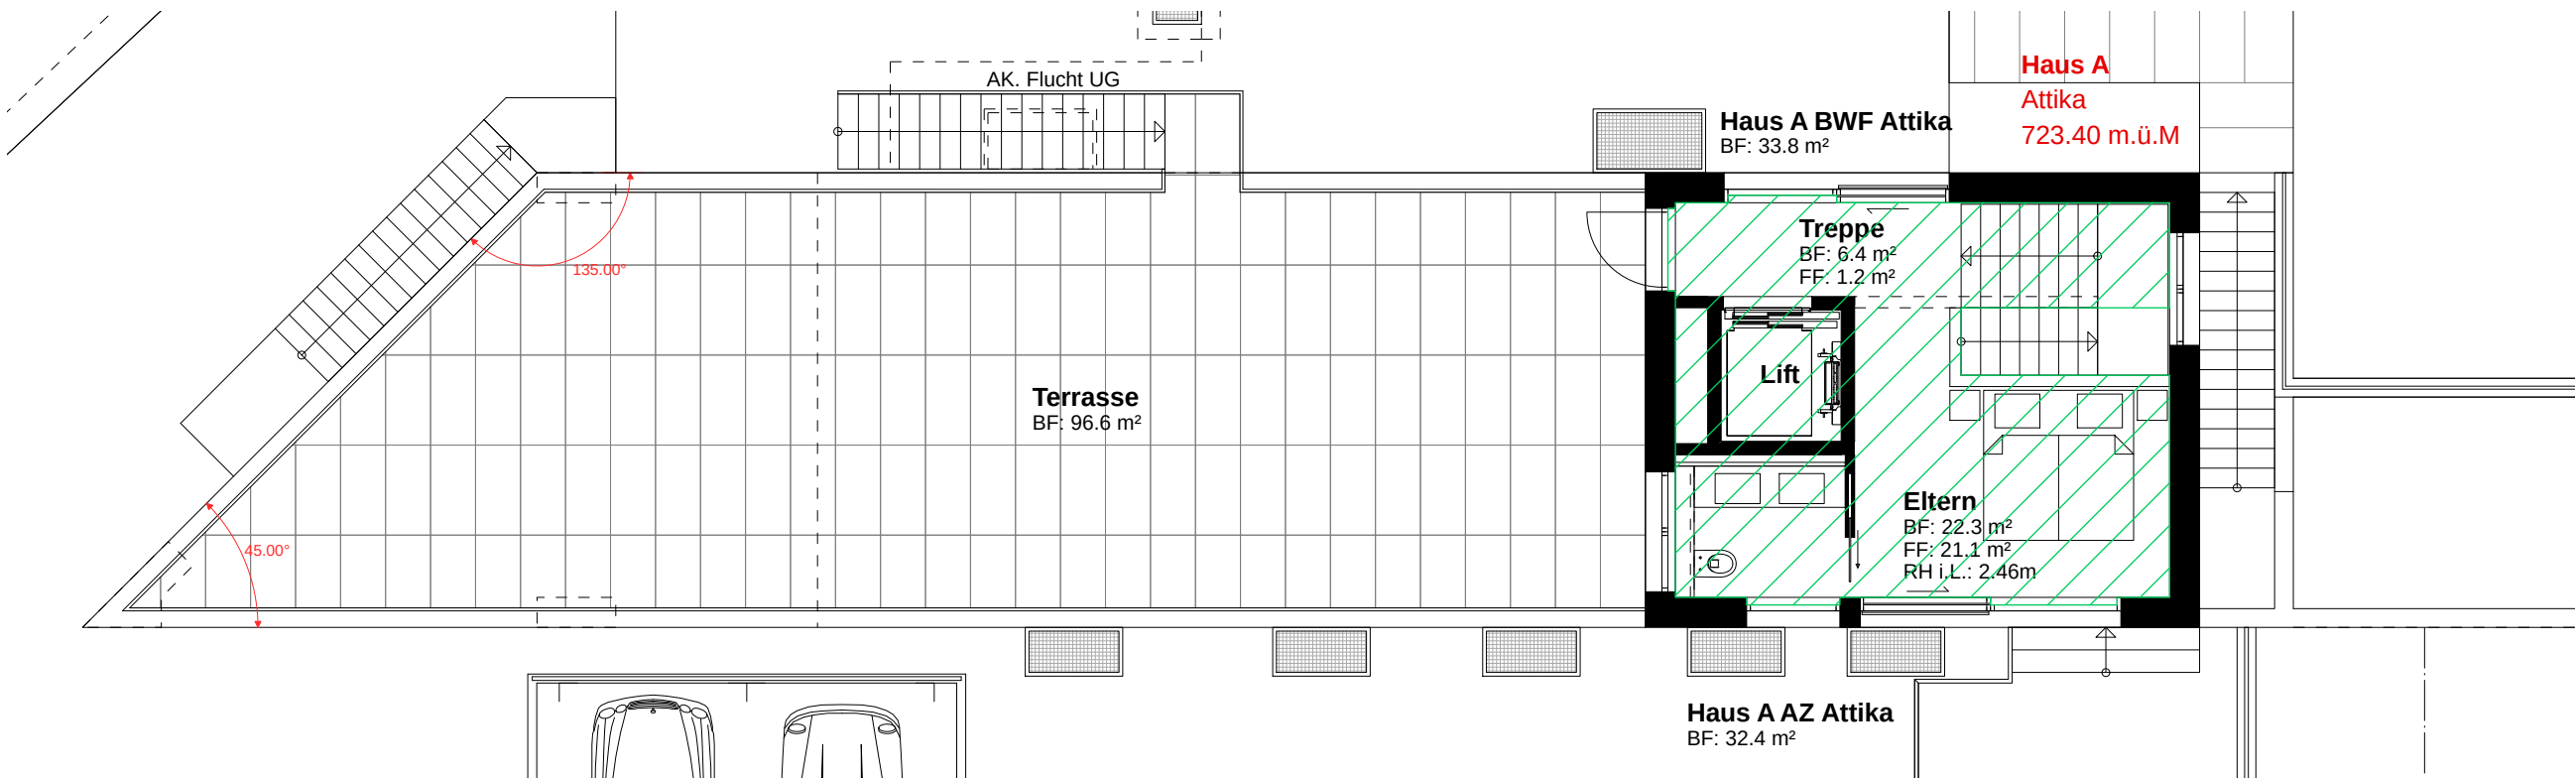


Attika

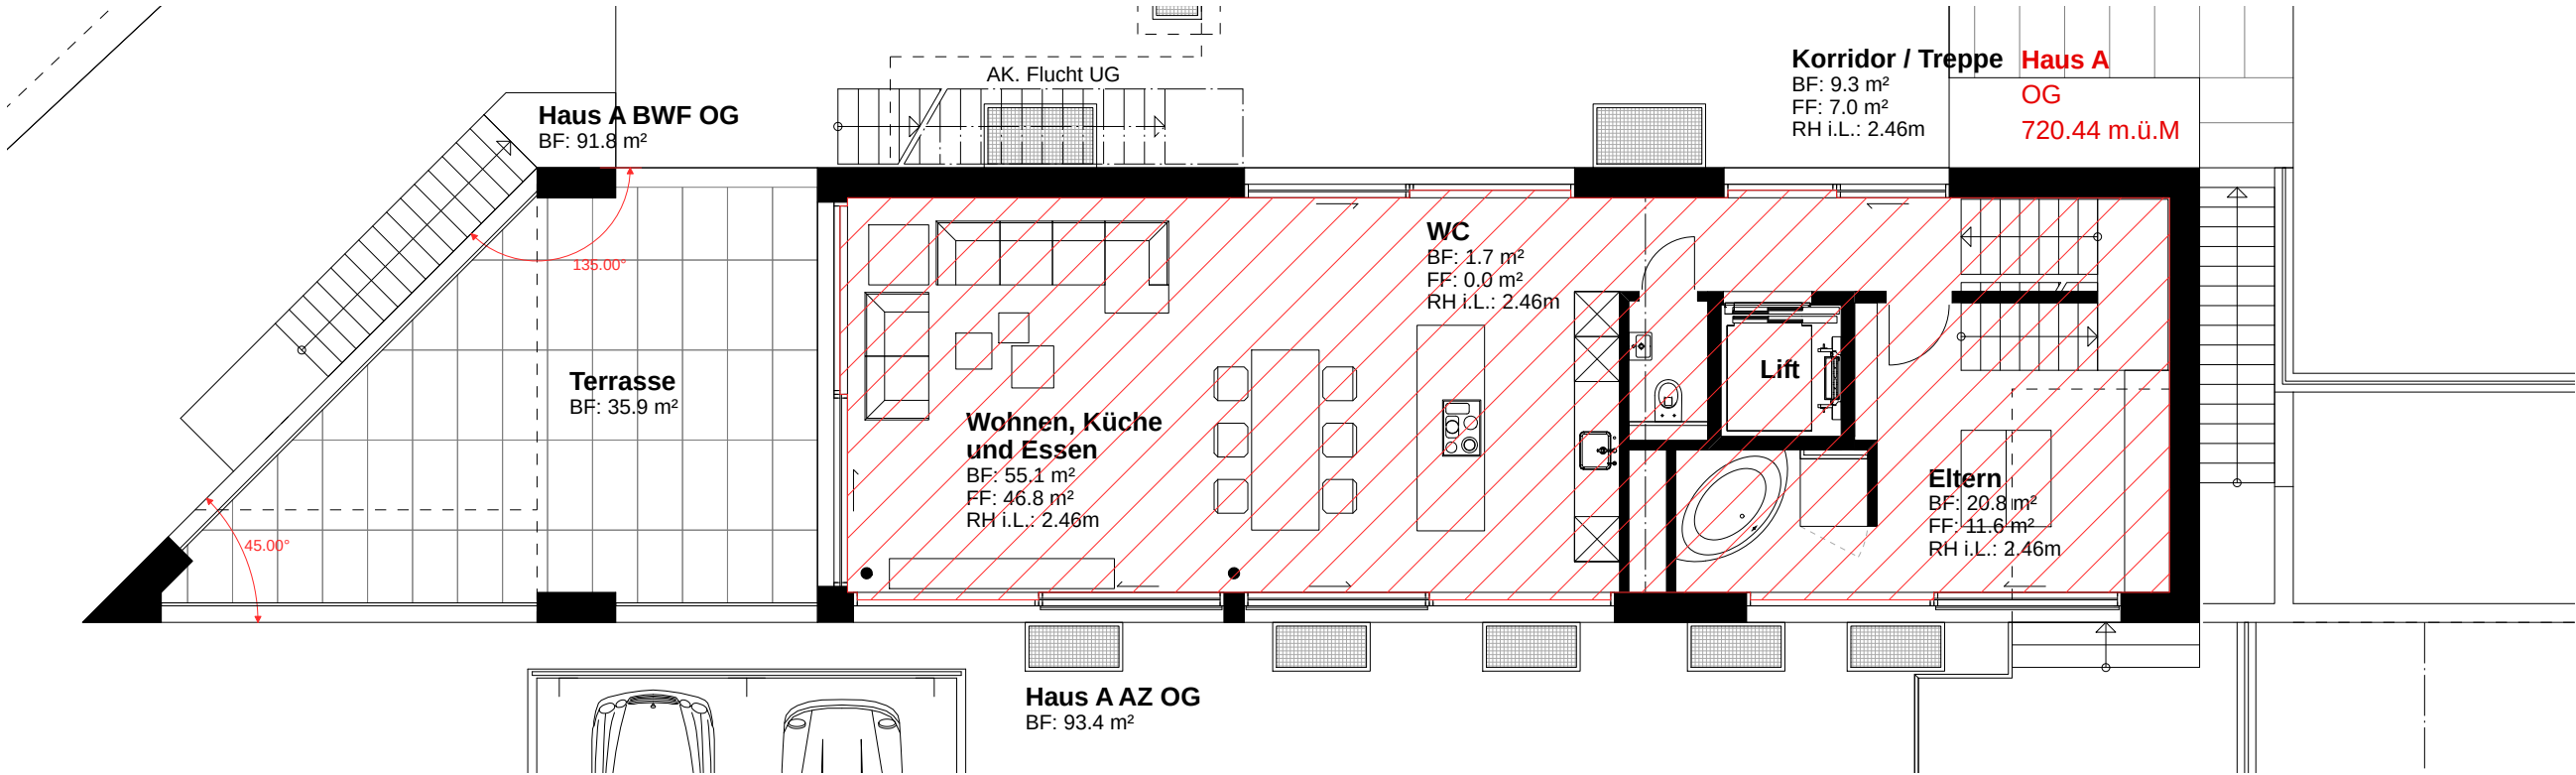

Obergeschoss

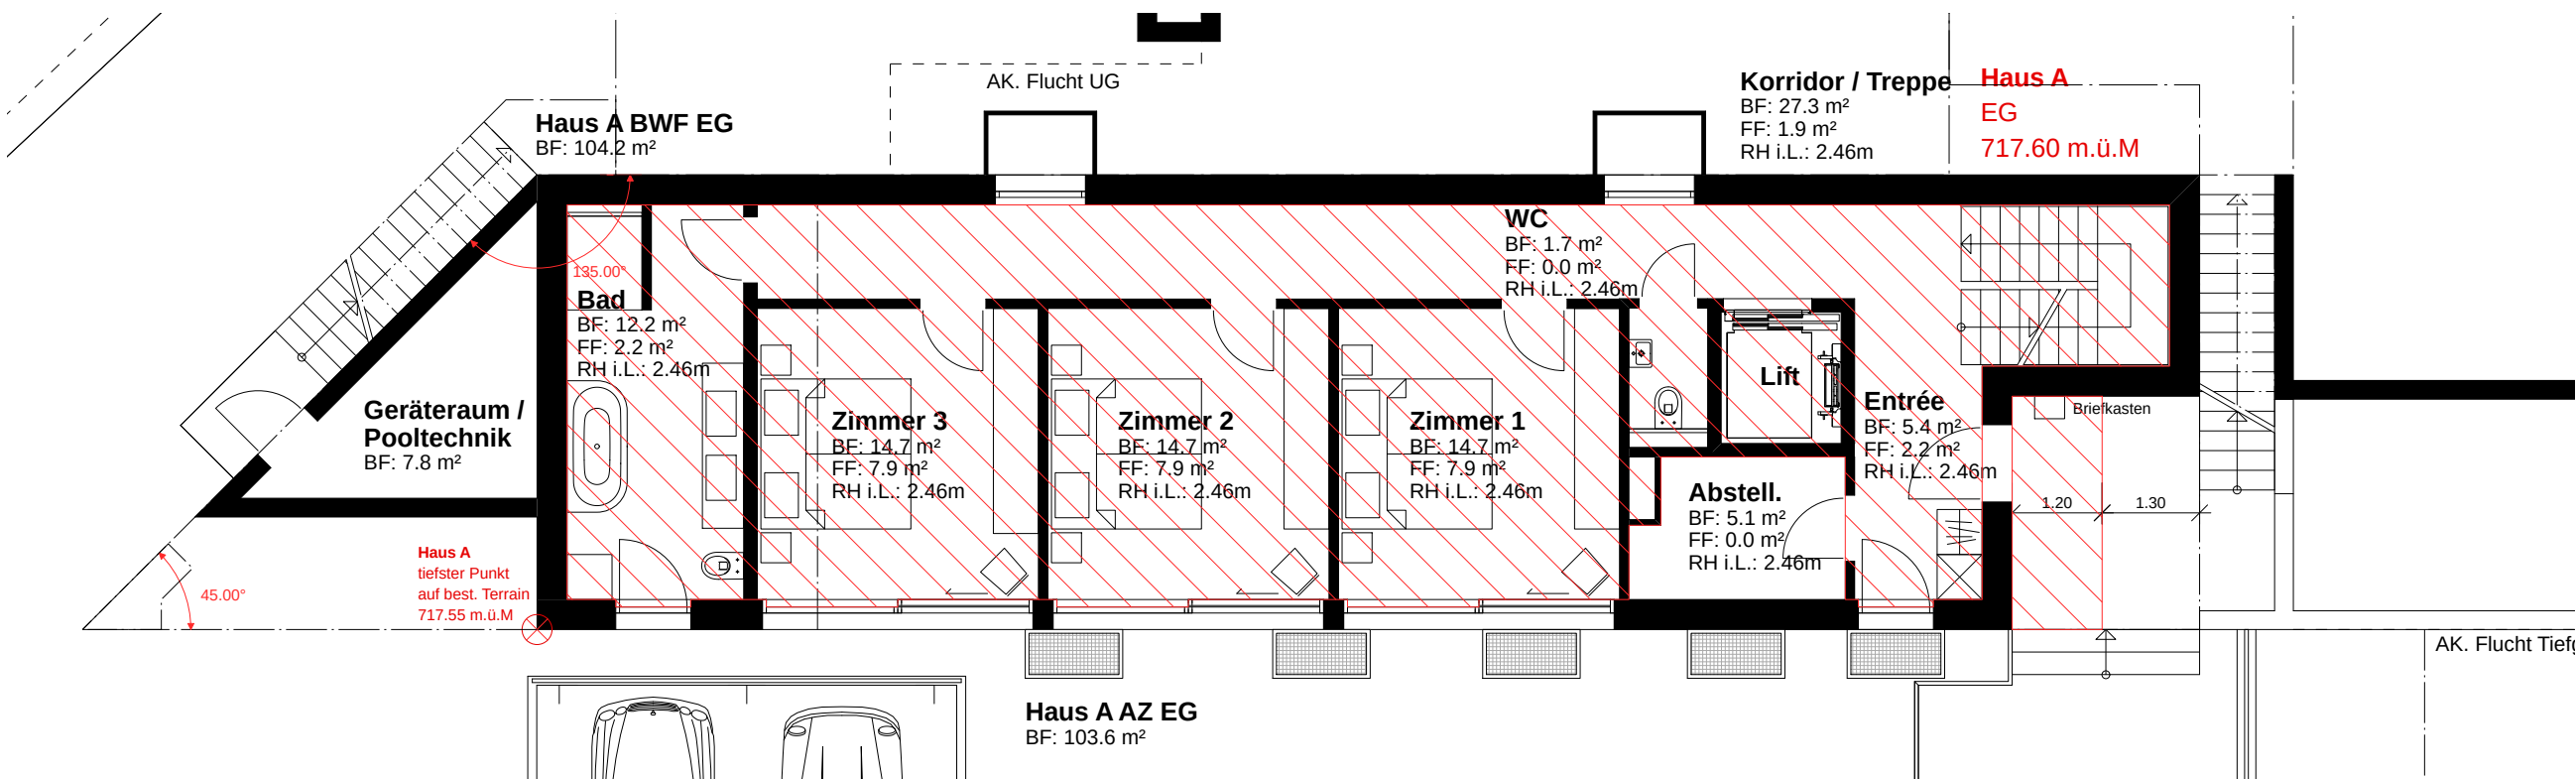

Erdgeschoss

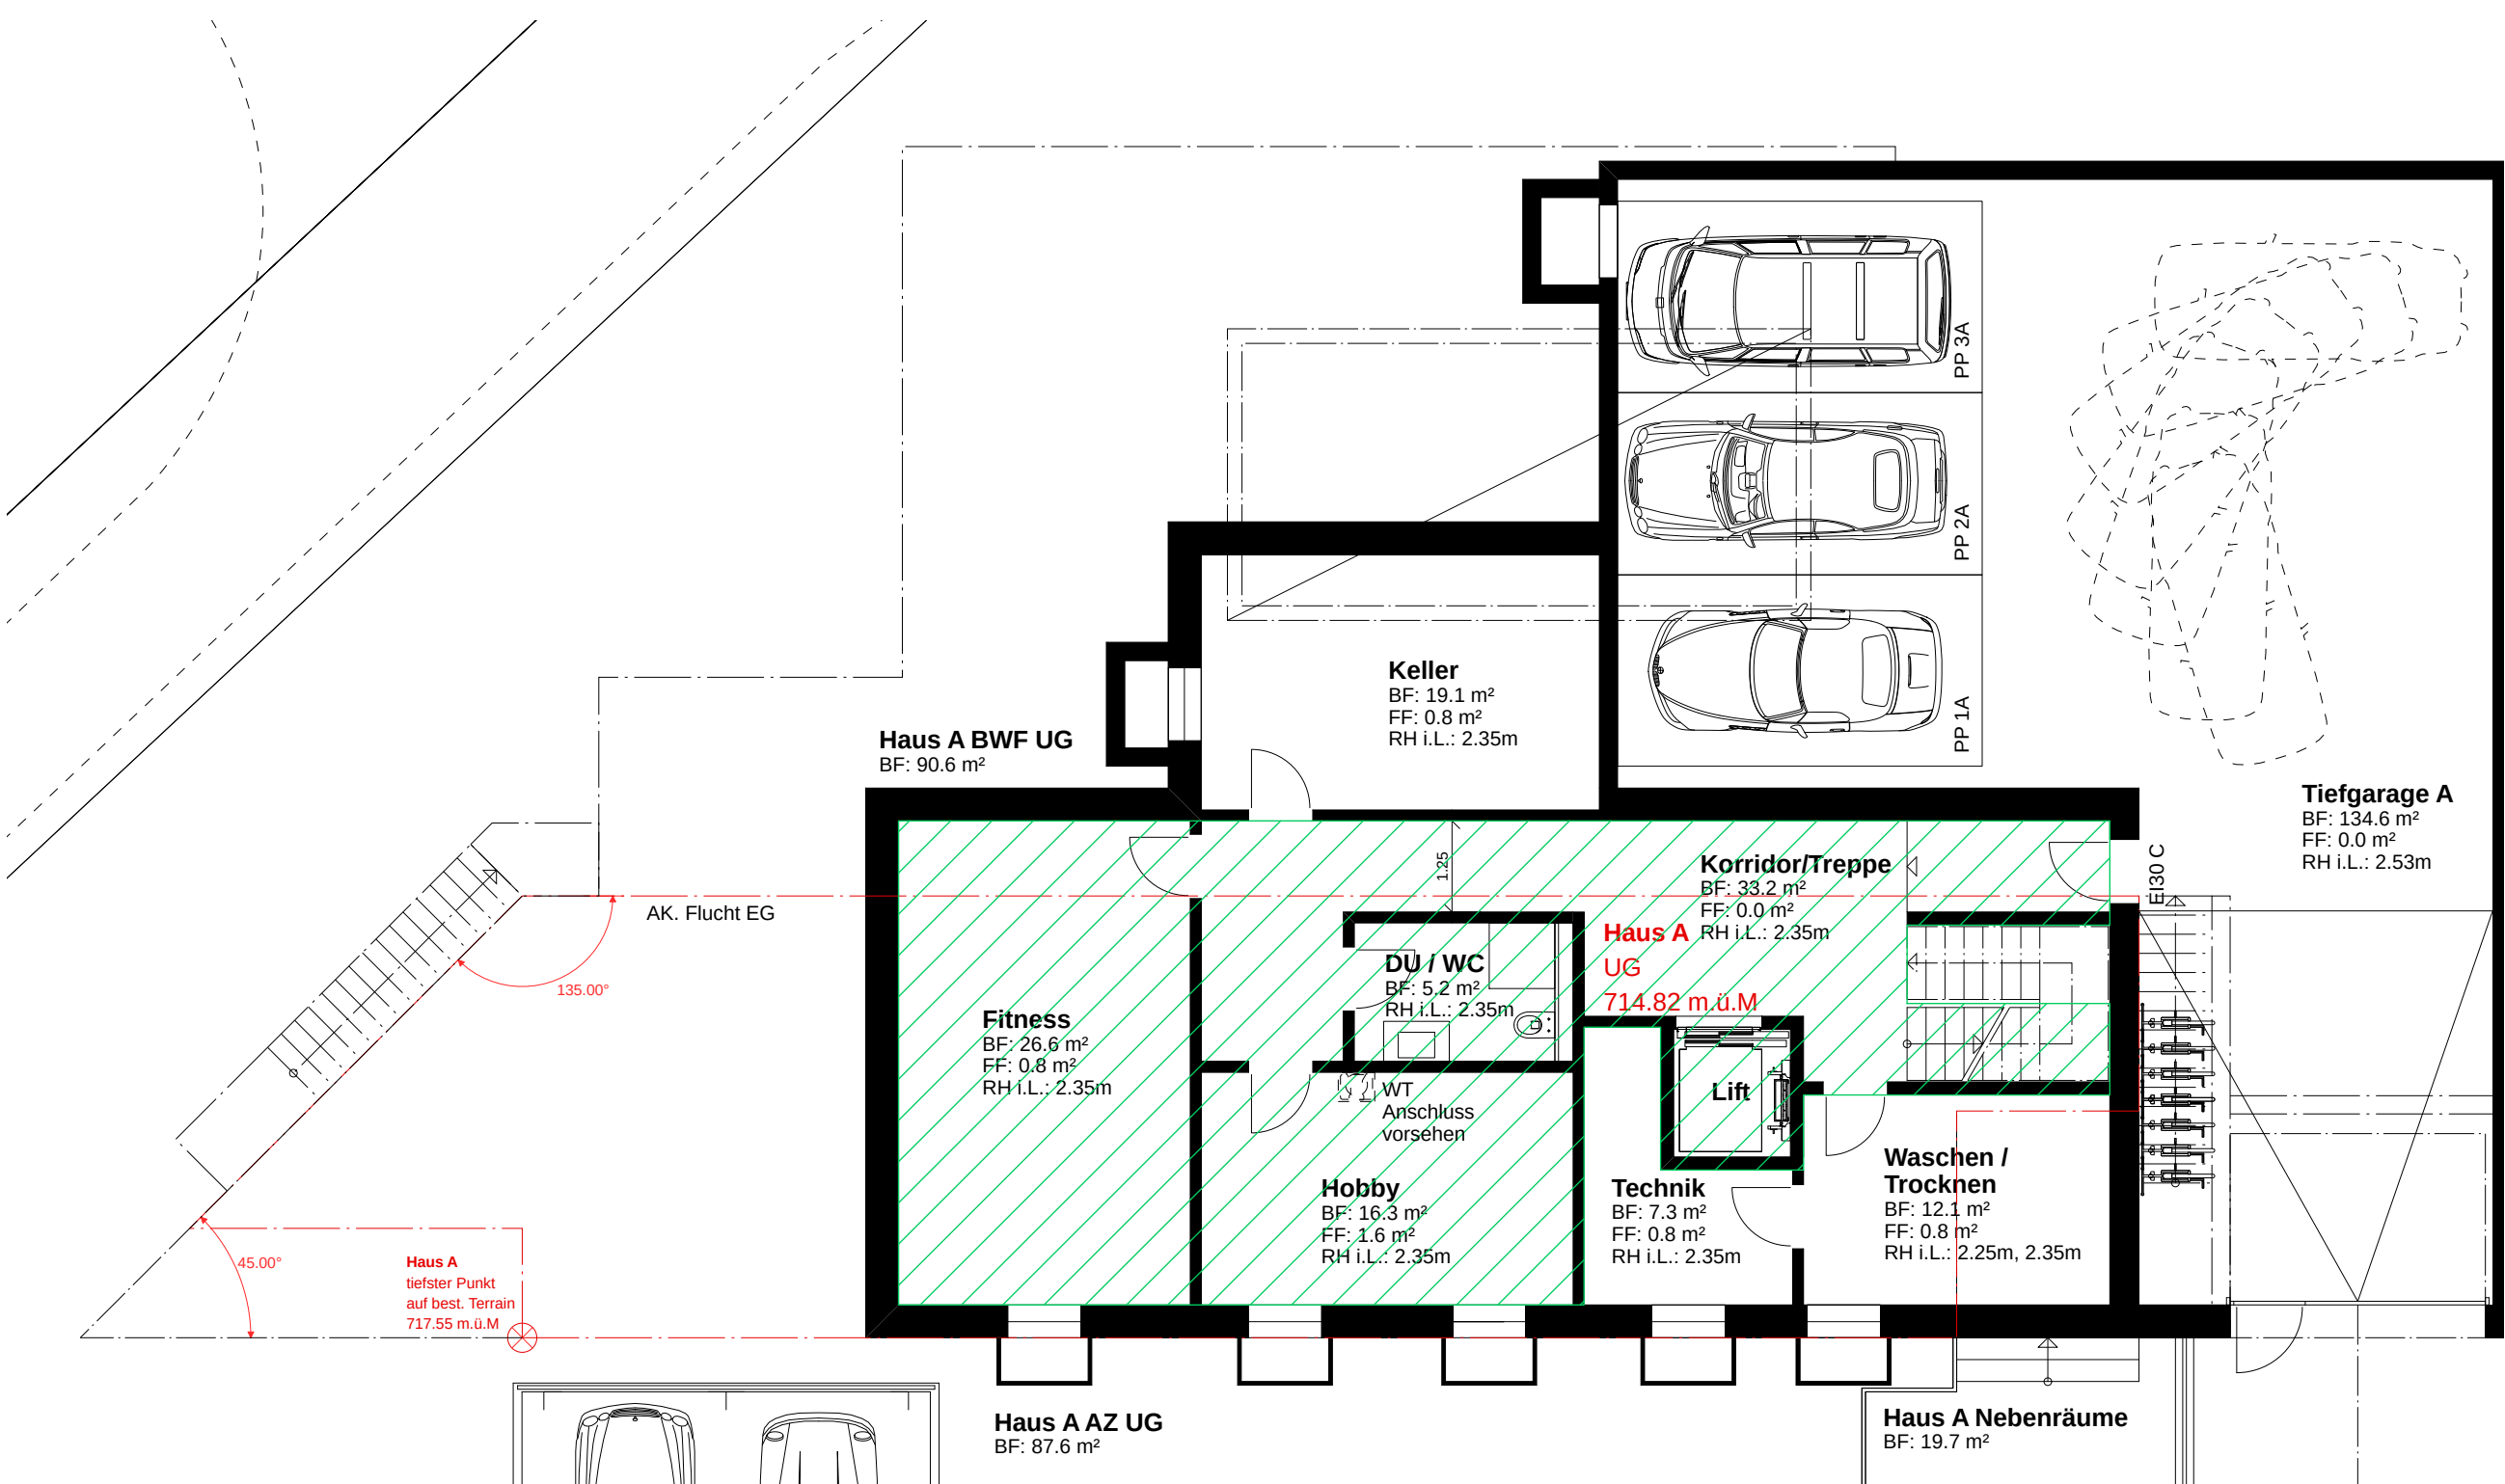

Untergeschoss

Projektverfasser:

dw design & concept ag  
Hofstrasse 106  
8620 Wetzikon

Bauherr / Grundeigentümer:

rlw immobilien ag  
Hofstrasse 106  
8620 Wetzikon

.....

Unterschrift Projektverfasser

.....

Unterschrift Bauherr / Grundeigentümer

±0.00 = 717.60 m.ü.M (OK Fertigbelag EG Haus A und B)

Alle Masse sind vom Unternehmer vor der Ausführung am Bau zu nehmen, bzw. zu kontrollieren. Allfällige Differenzen sind unverzüglich mit der Bauleitung zu klären. Falls nicht anderst vermerkt sind die Fensterhöhen von OK fertig Boden bis UK Sturz gemessen. Türhöhen sind von OK fertig Boden oder Schwelle bis UK roher Sturz gemessen.

| Index | Datum      | Geändert von | Änderung                                 |
|-------|------------|--------------|------------------------------------------|
| A     | 26.07.2023 | MDS          | Planauswechslung / Planlayout angepasst. |
|       |            |              |                                          |
|       |            |              |                                          |
|       |            |              |                                          |

**BAUVORHABEN:** Überbauung Zumikon

**ADRESSE:** Haldenstrasse 5, 8126 Zumikon  
Parzelle 2999

dw design & concept ag

dw design & concept ag  
Hofstrasse 106  
8620 Wetzikon

Tel: +41 (0)43 477 44 33

info@dw-dc.ch  
www.dw-dc.ch

Dieser Plan ist urheberrechtlich geschützt!  
Geistiges Eigentum der dw design & concept ag.  
Kopieren und weiterverkaufen verboten!

|             |                                                             |       |            |
|-------------|-------------------------------------------------------------|-------|------------|
| Phase       | BAUEINGABE                                                  |       |            |
| Plannummer  | 110A                                                        |       |            |
| Planinhalt  | Grundrisse Ausnützung<br>Haus A<br>Untergeschoss bis Attika |       |            |
| Plangröße   | 630/600                                                     |       |            |
| gezeichnet  | Michael Di Stefano                                          | Datum | 2022-11-17 |
| geprüft     |                                                             |       |            |
| freigegeben |                                                             |       |            |

1:100

dw design & concept ag