




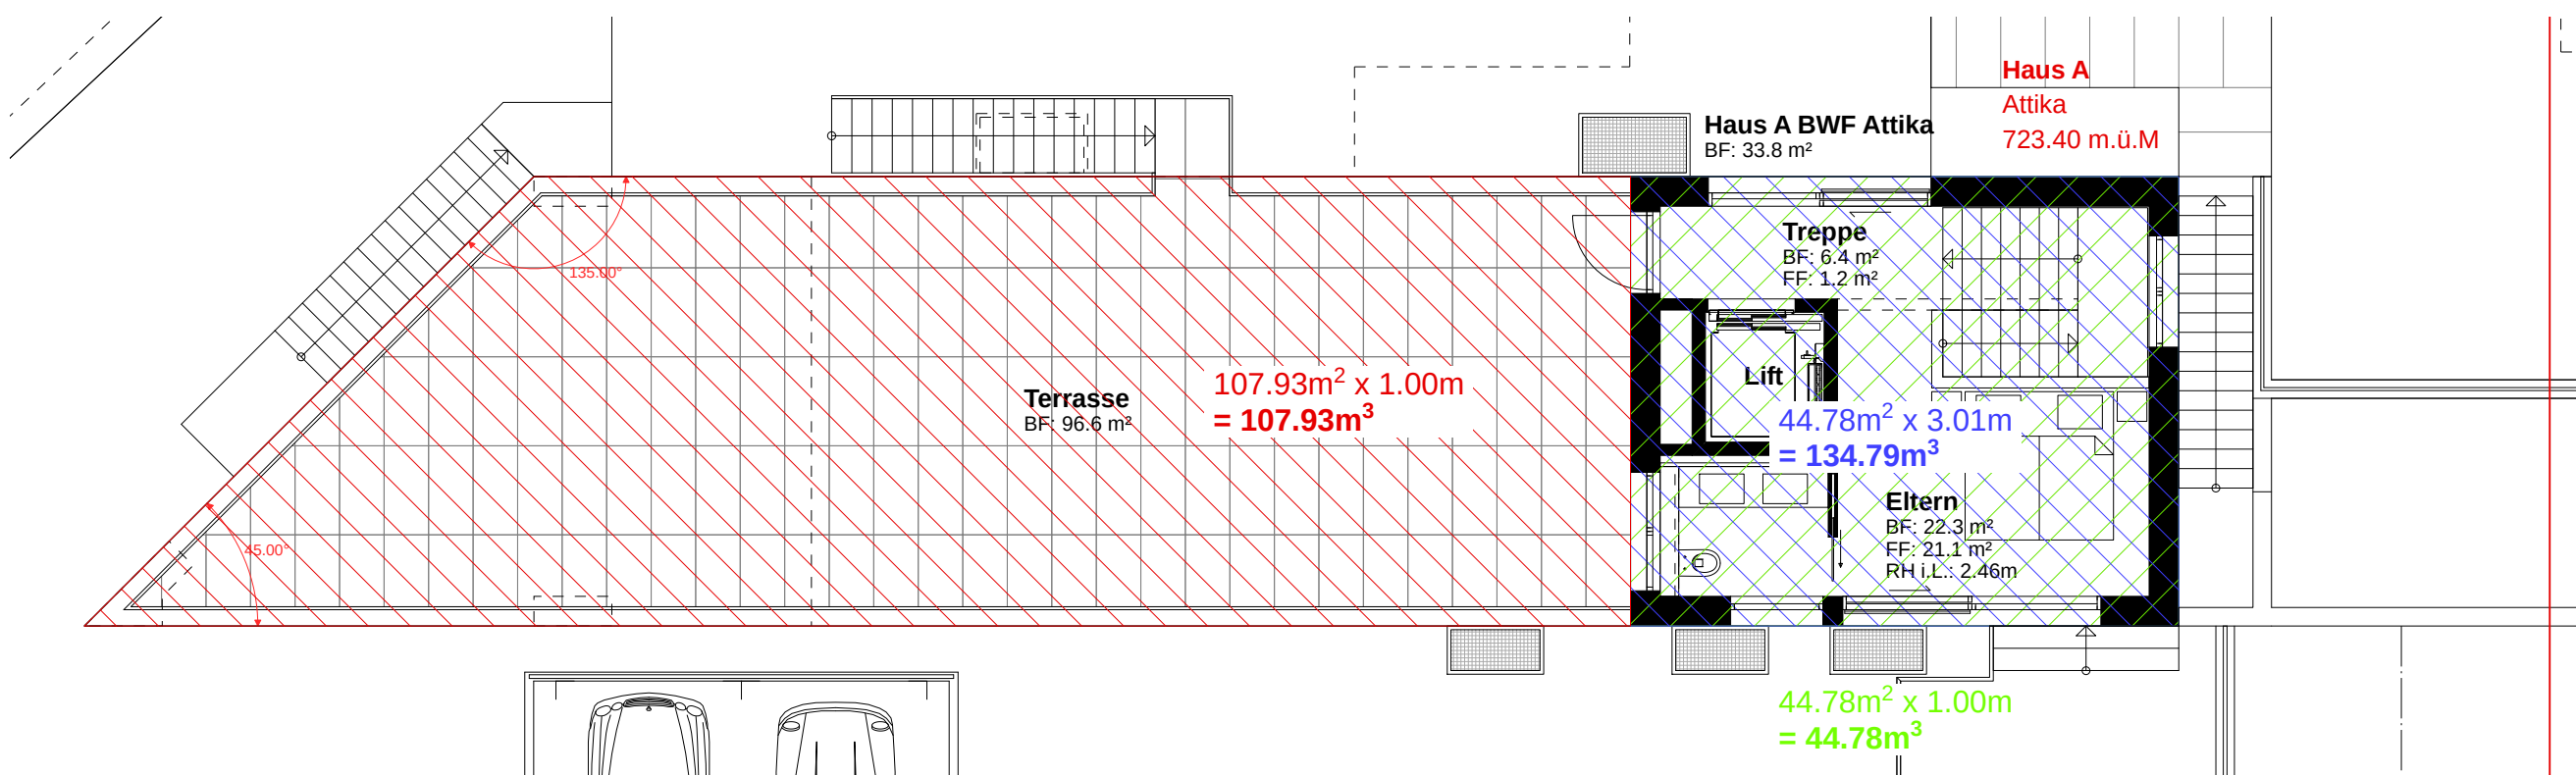


Attika

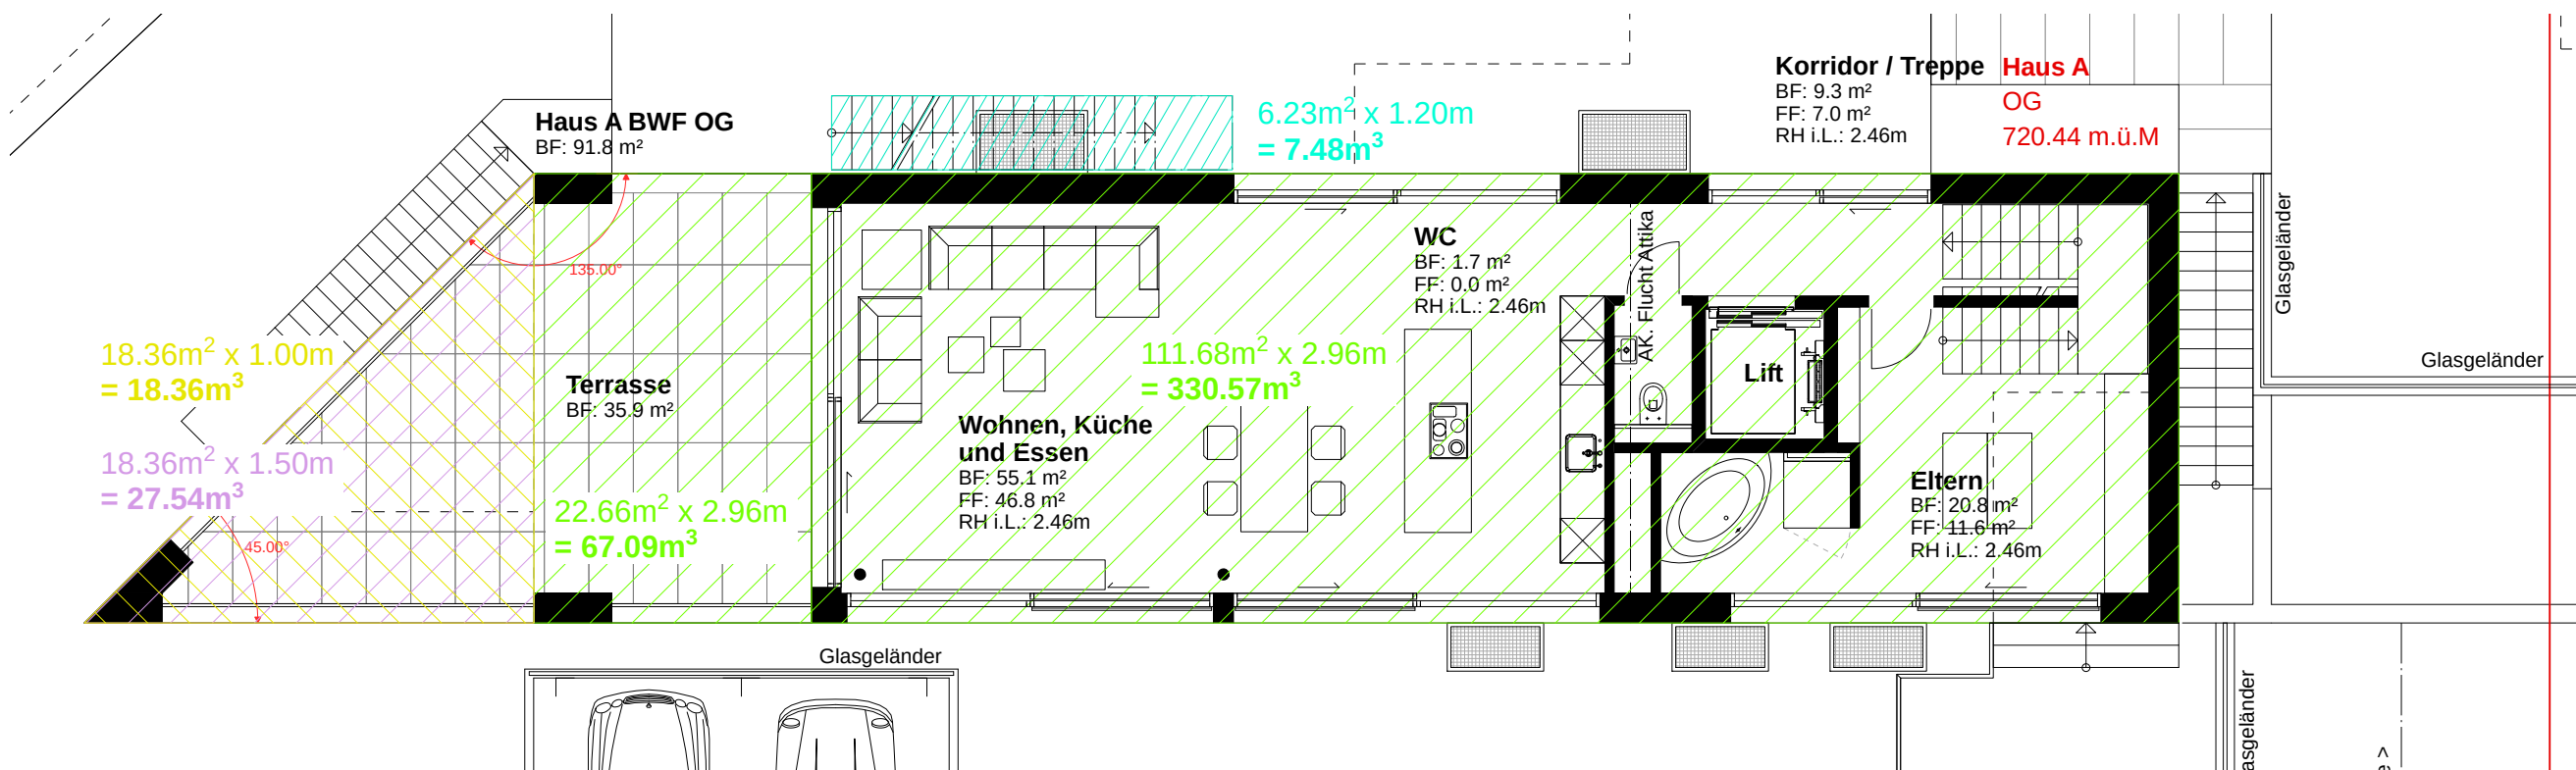

Obergeschoss

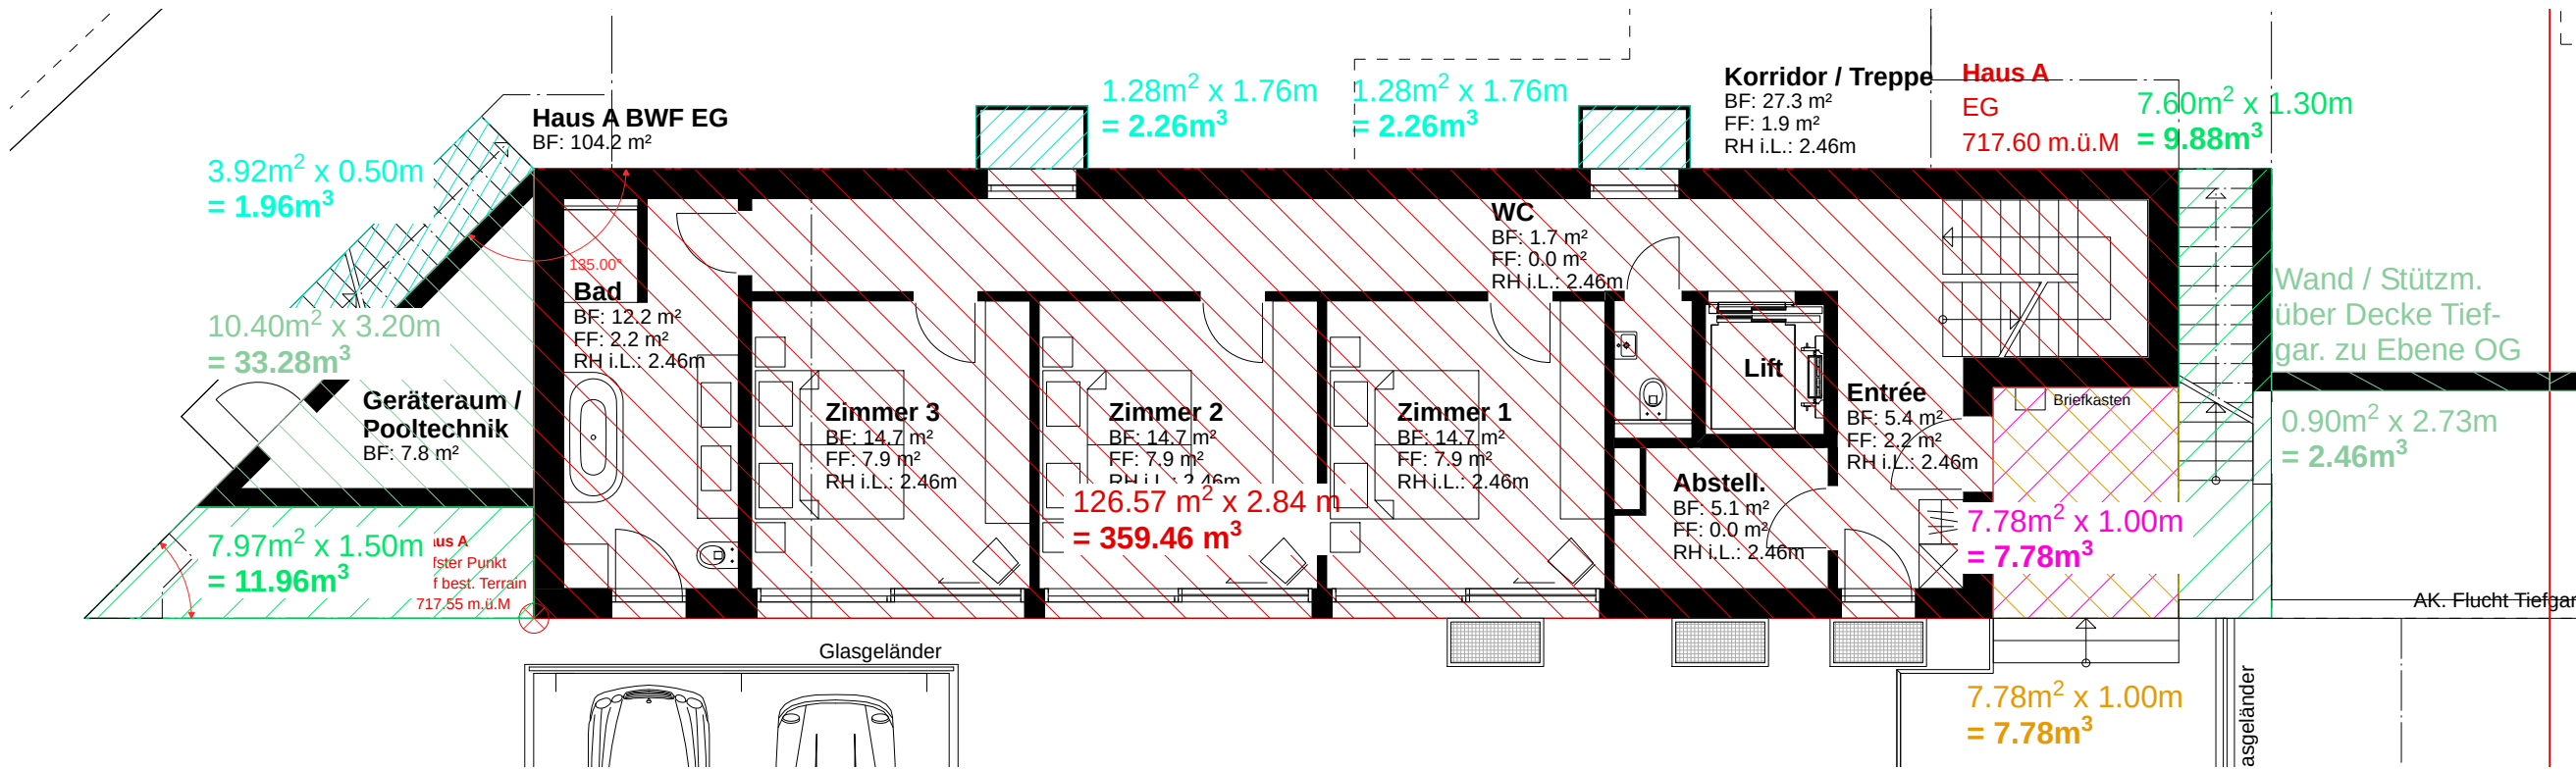

Erdgeschoss

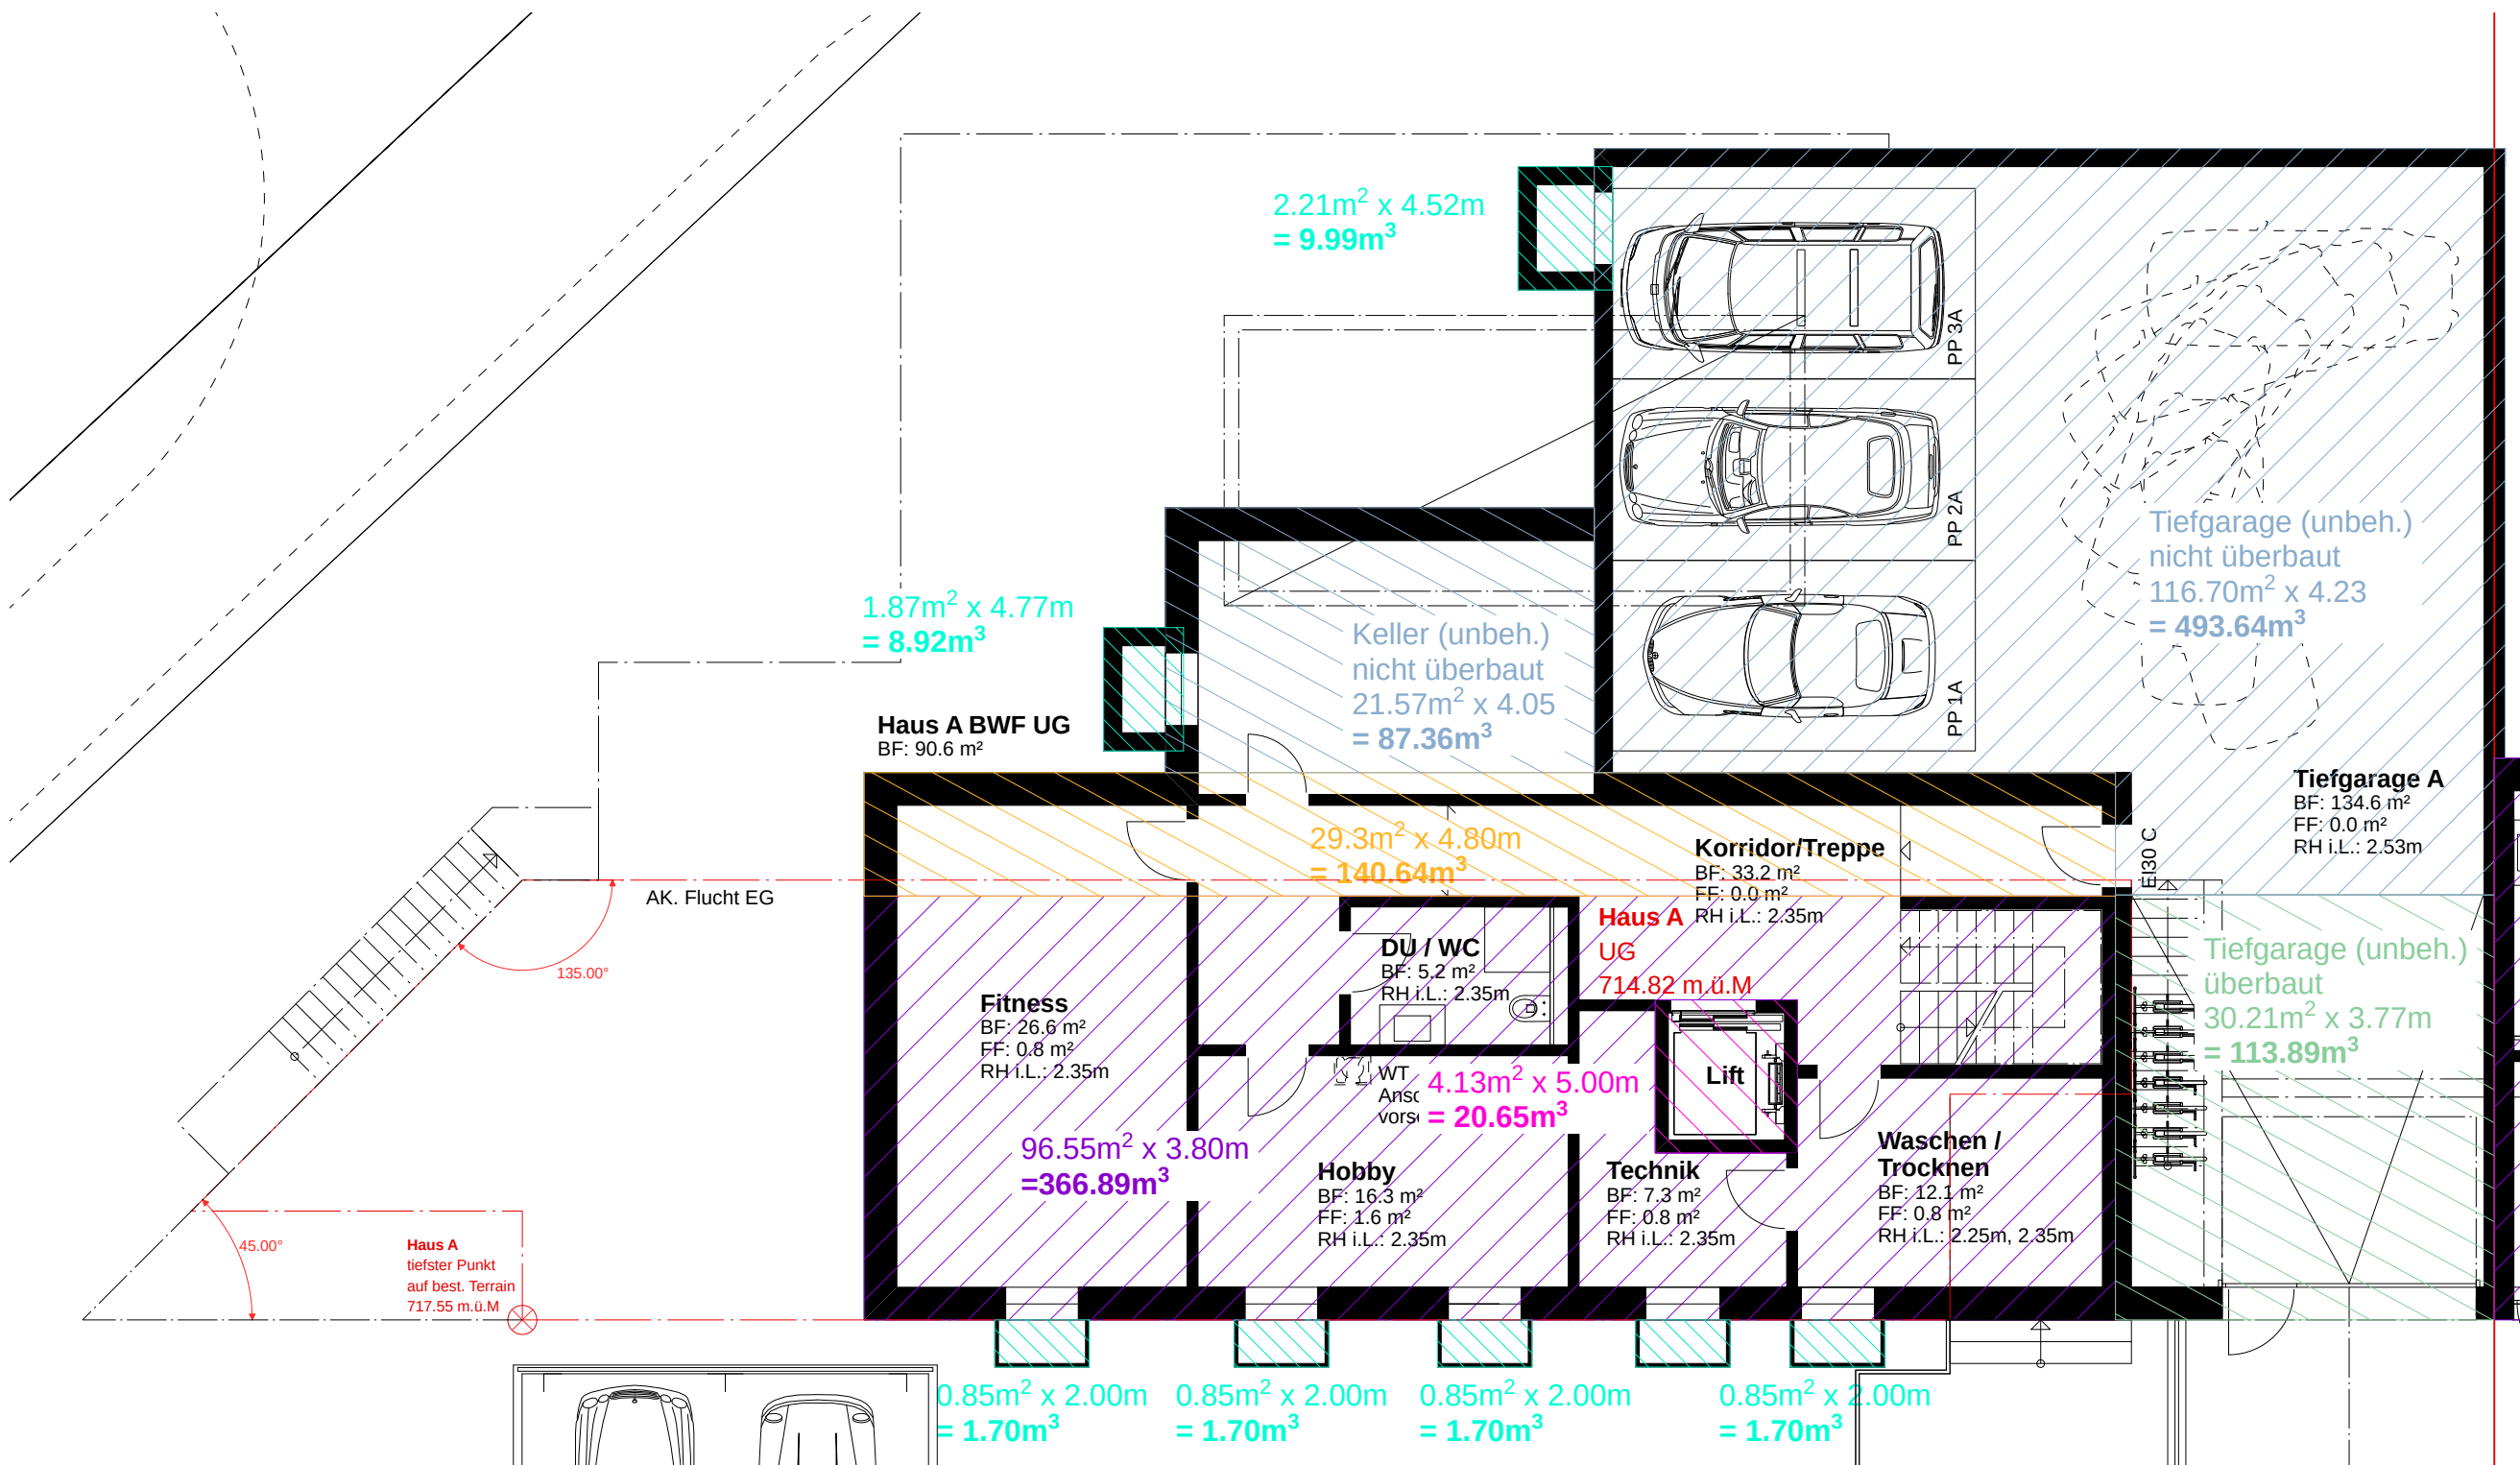

Untergeschoss

Projektverfasser:

dw design & concept ag
Hofstrasse 106
8620 Wetzikon

Bauherr / Grundeigentümer:

rlw immobilien ag
Hofstrasse 106
8620 Wetzikon

Unterschrift Projektverfasser

Unterschrift Bauherr / Grundeigentümer


±0.00 = 717.60 m.ü.M (OK Fertigbelag EG Haus A und B)

Alle Masse sind vom Unternehmer vor der Ausführung am Bau zu nehmen, bzw. zu kontrollieren. Allfällige Differenzen sind unverzüglich mit der Bauleitung zu klären. Falls nicht anders vermerkt sind die Fensterhöhen von OK fertig Boden bis UK Sturz gemessen. Türhöhen sind von OK fertig Boden oder Schwelle bis UK roher Sturz gemessen.

Index	Datum	Geändert von	Änderung
A	26.07.2023	MDS	Planauswechslung / Planlayout angepasst.

BAUVORHABEN: Überbauung Zumikon
Haus A

ADRESSE: Haldenstrasse 5, 8126 Zumikon
Parzelle 2999

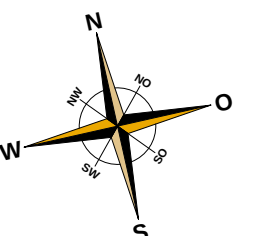

dw design & concept ag		Phase	BAUEINGABE	
dw design & concept ag Hofstrasse 106 8620 Wetzikon		Plannummer	114A	
Tel: +41 (0)43 477 44 33		Planinhalt	Grundrisse Kubische Berechnung	
info@dw-dc.ch www.dw-dc.ch		Plangröße	630x600	
Dieser Plan ist urheberrechtlich geschützt! Geistiges Eigentum der dw design & concept ag. Kopieren und weiterverkaufen verboten!		Name	Datum	Maßstab
		gezeichnet	Michael Di Stefano	2022-11-17
		geprüft		
		freigegeben		1:100