




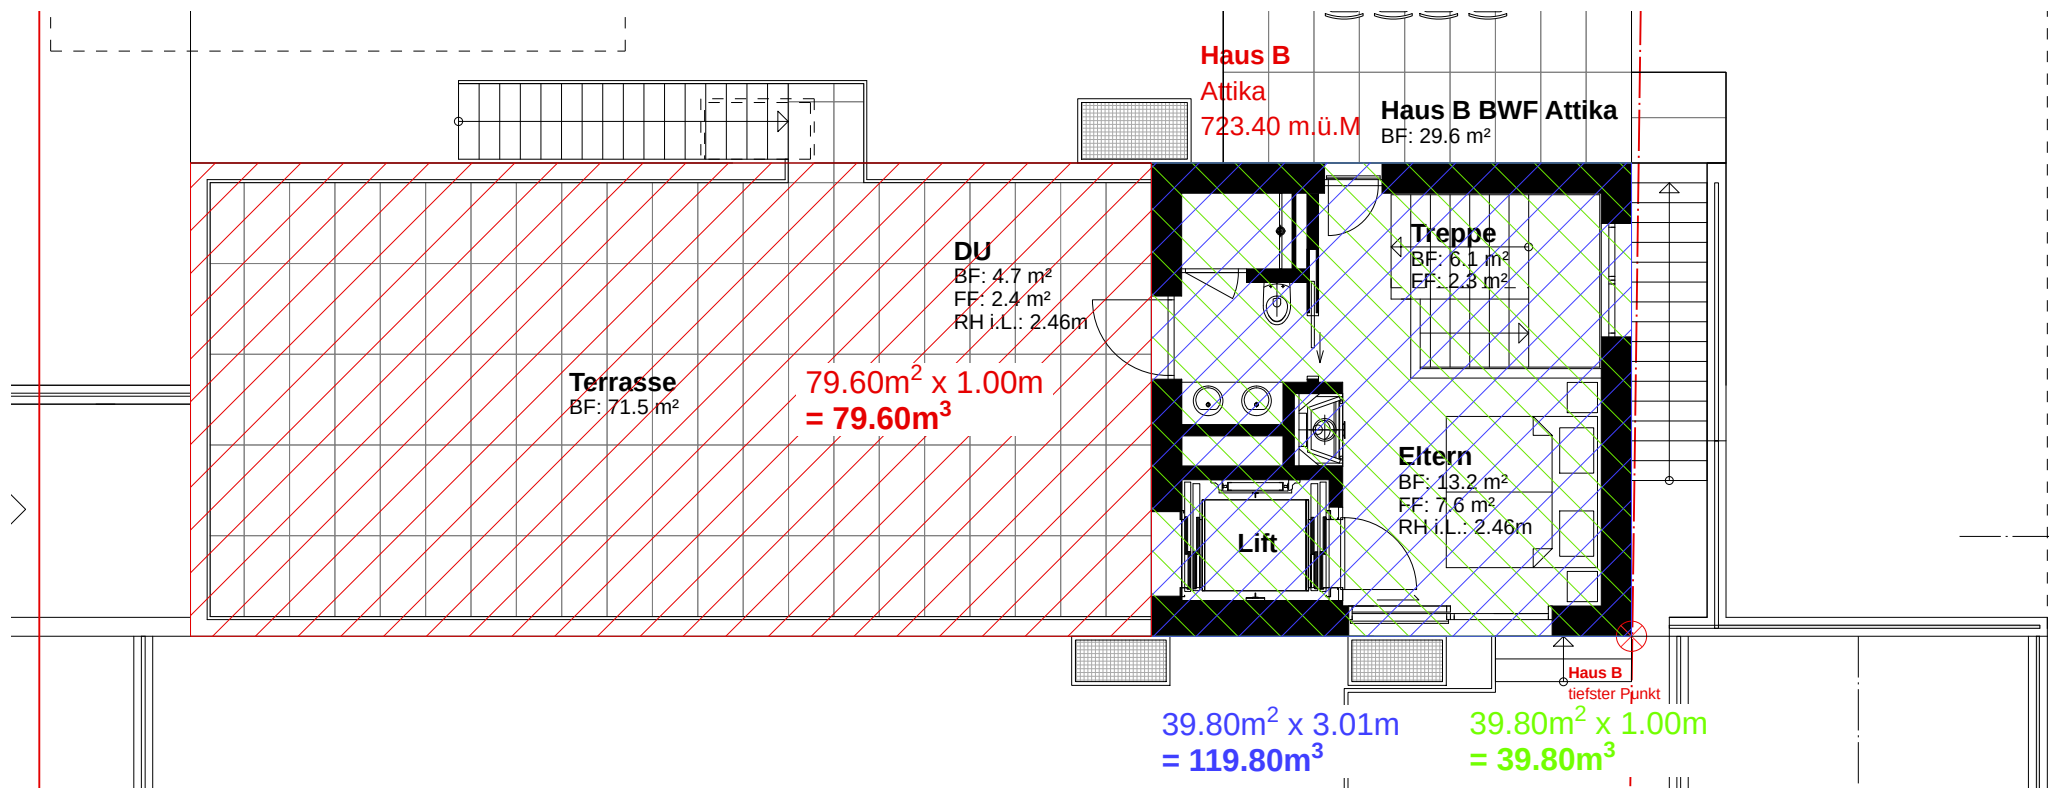


Attika

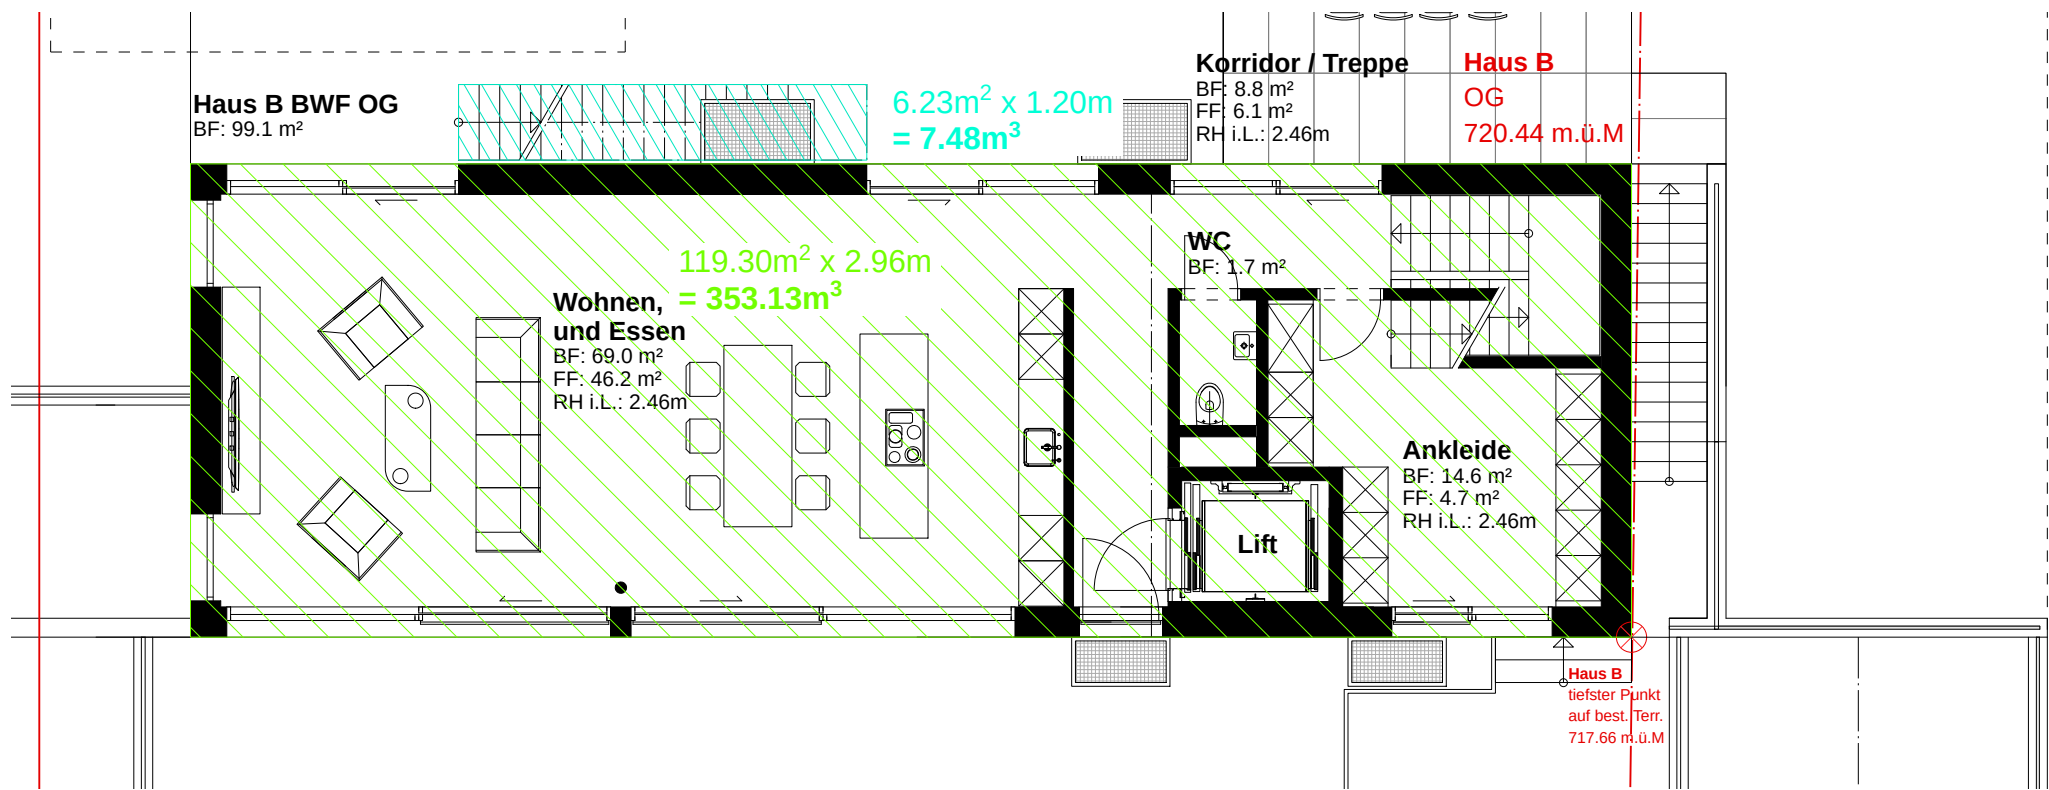

Obergeschoss

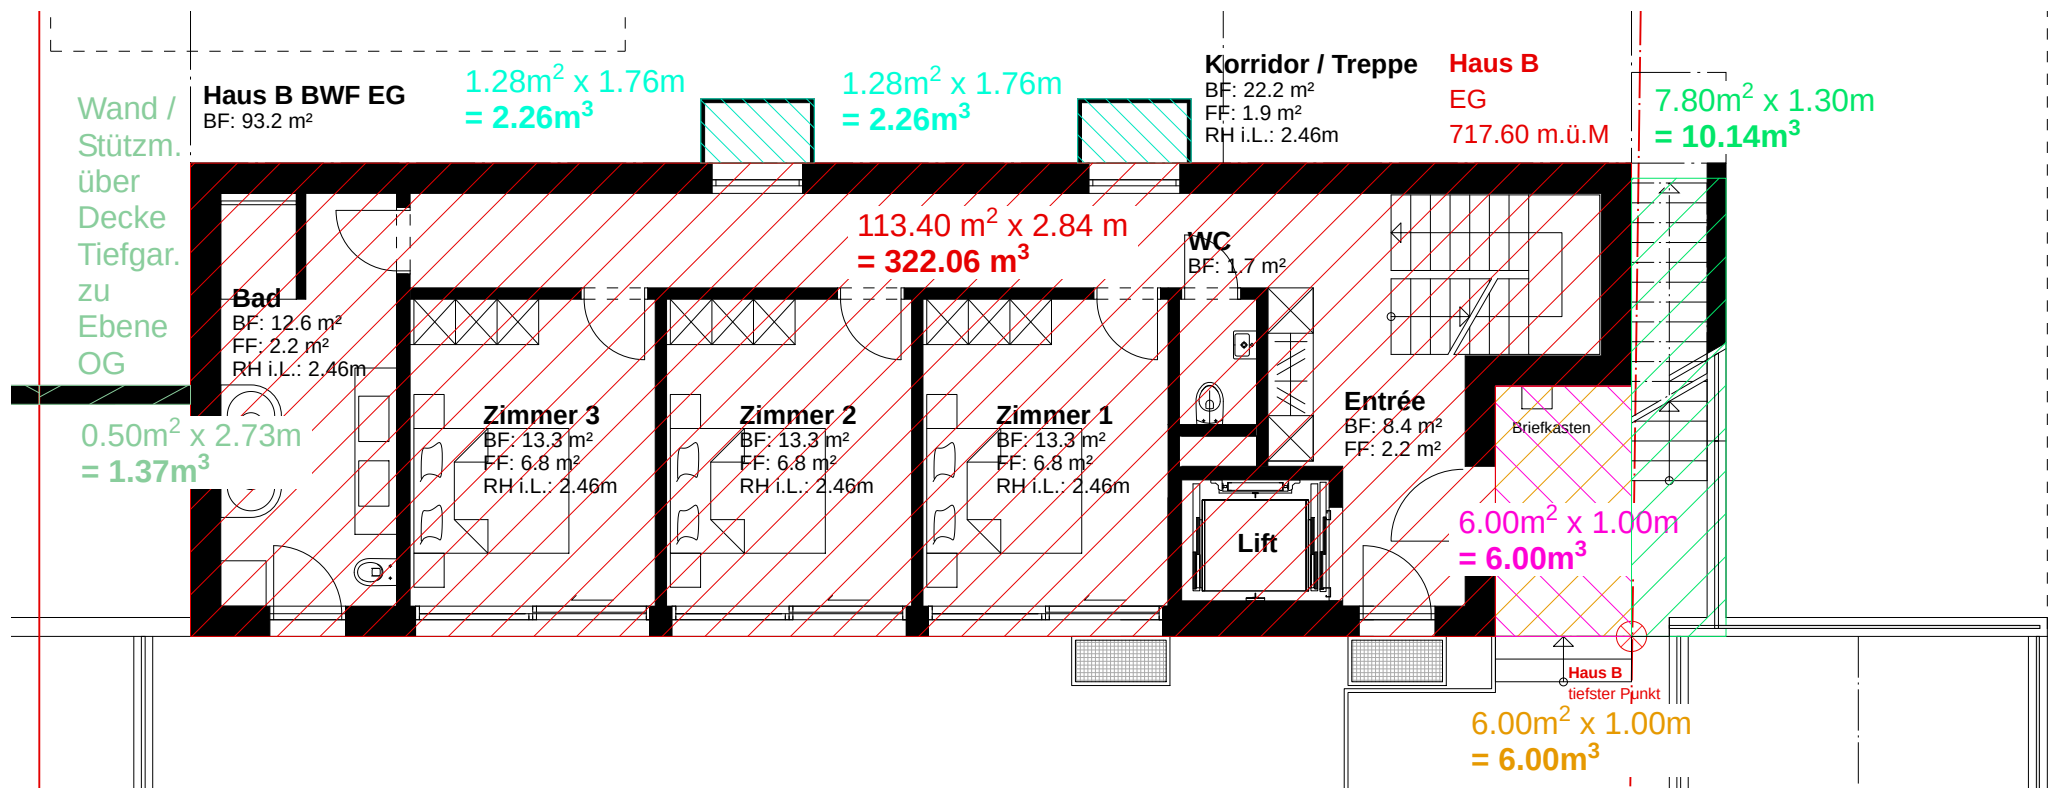

Erdgeschoss

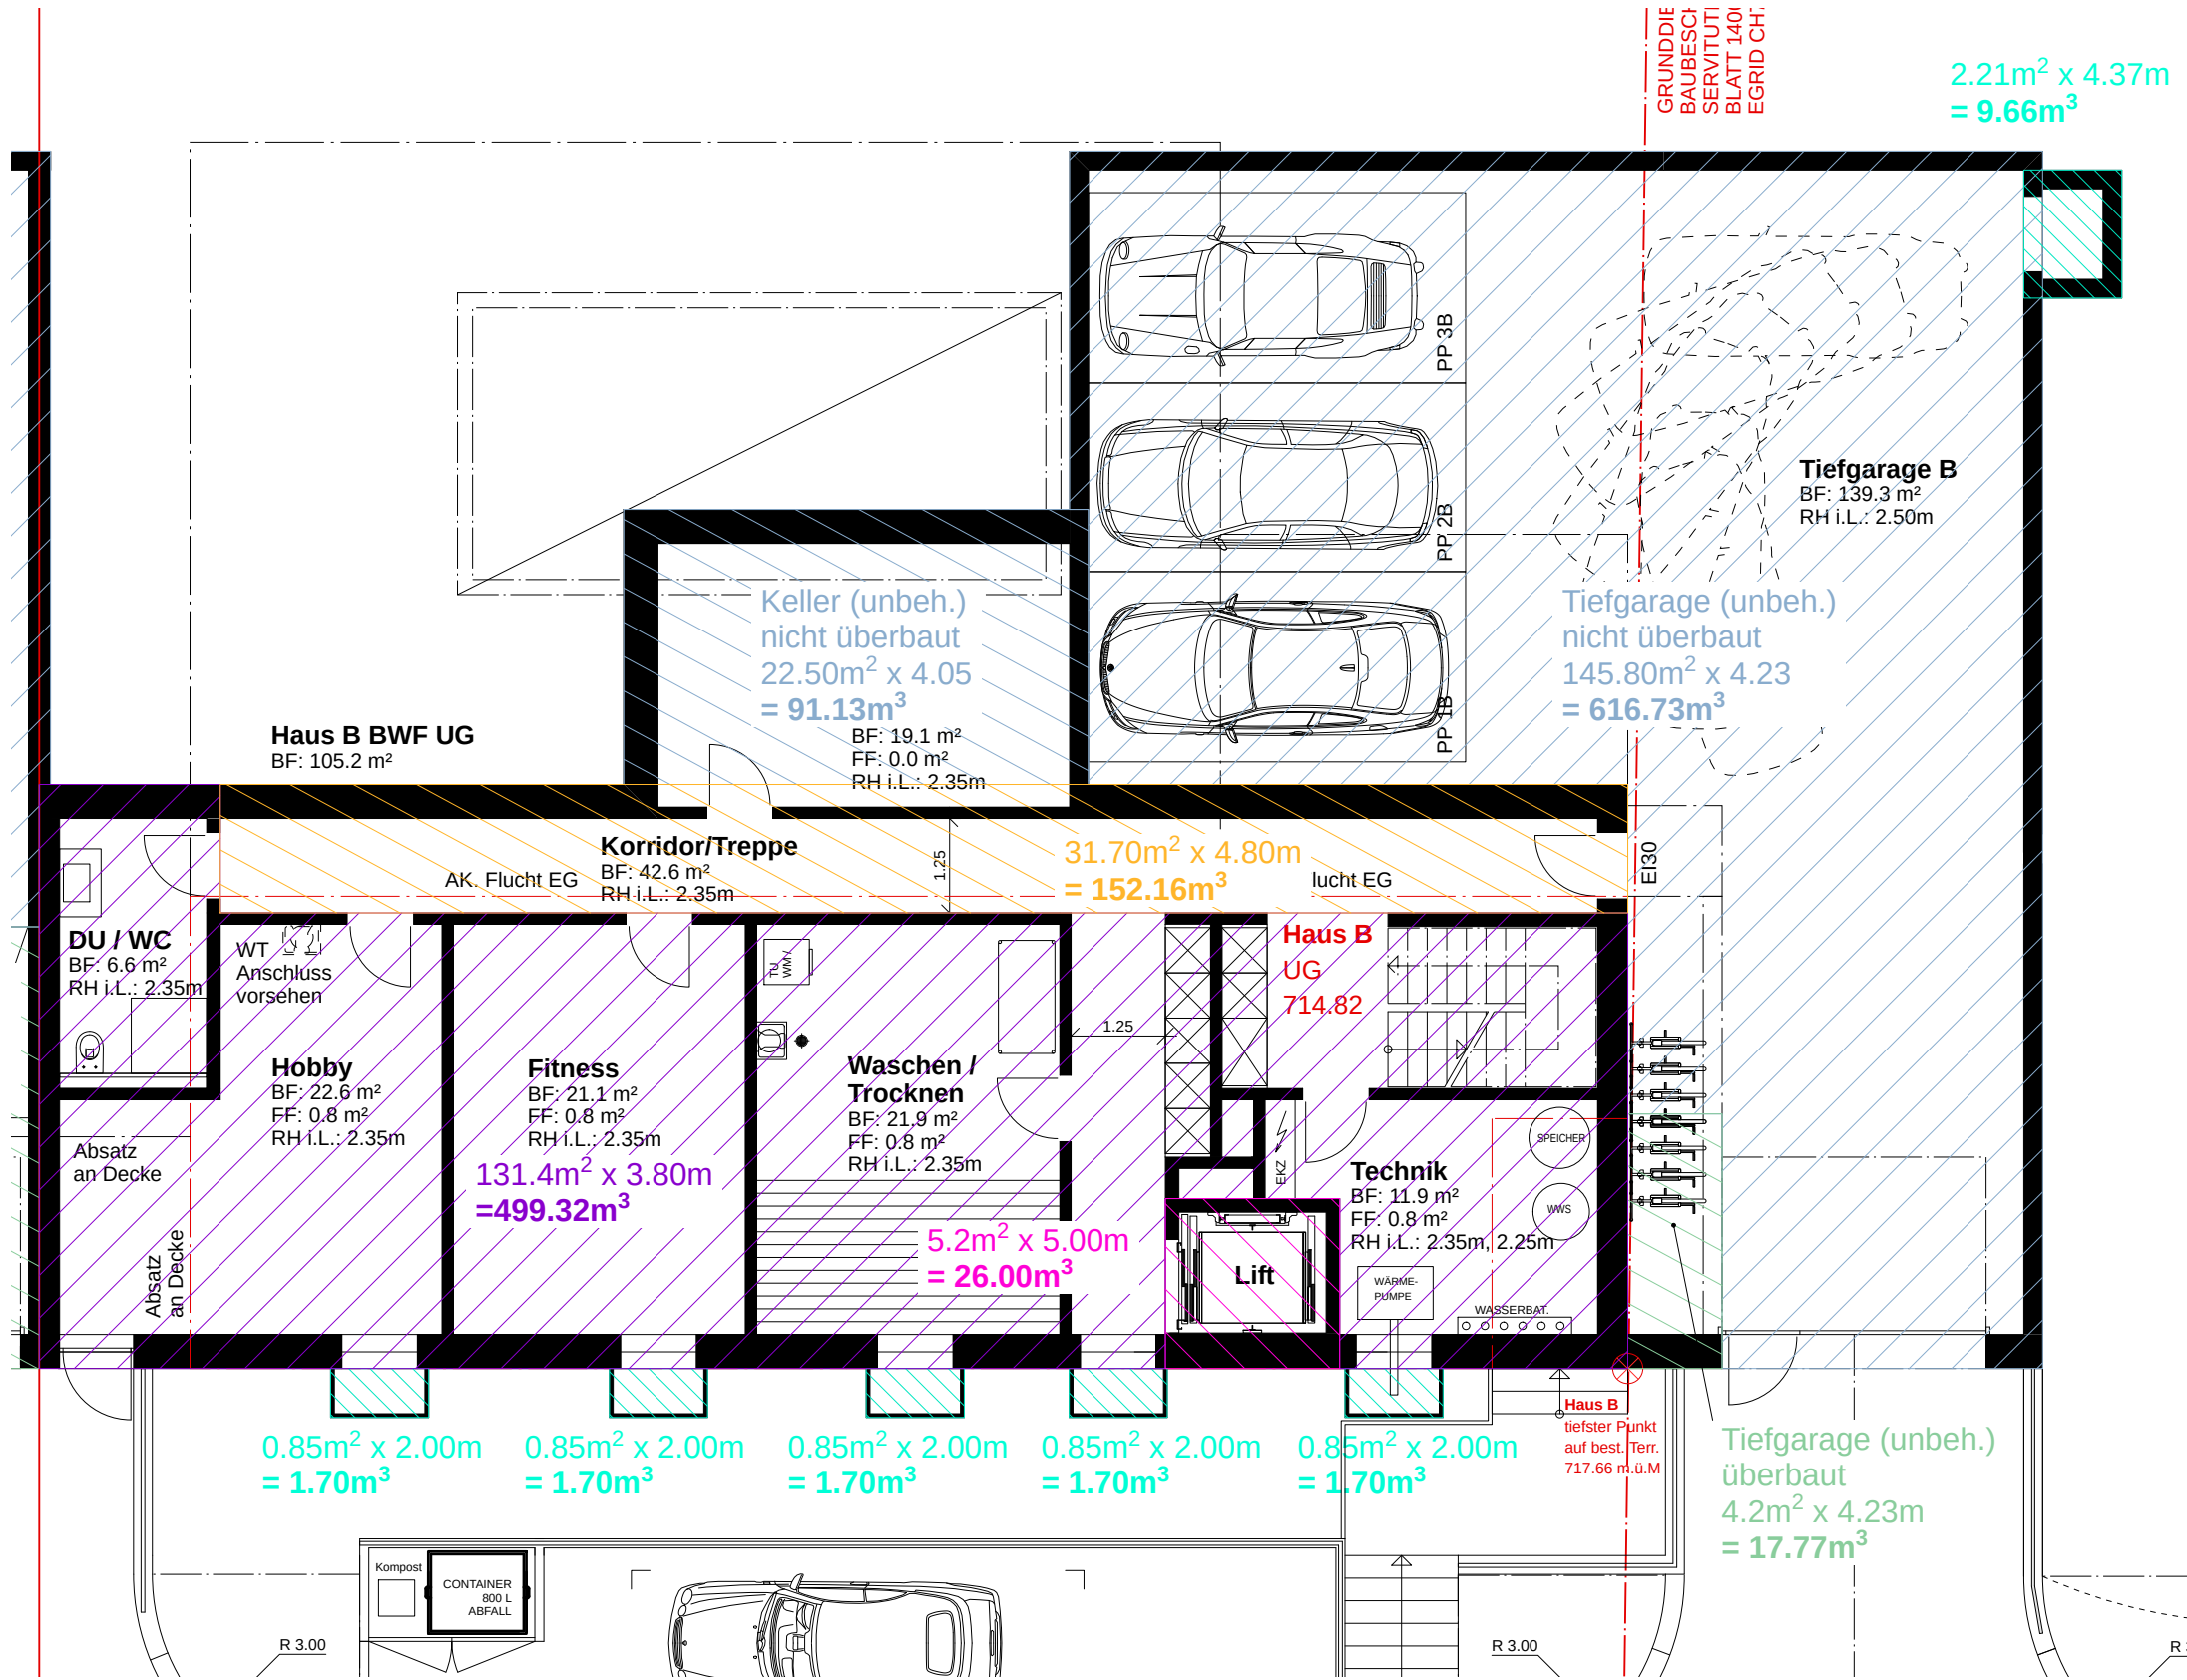

Untergeschoss

Projektverfasser:

dw design & concept ag
Hofstrasse 106
8620 Wetzikon

Bauherr / Grundeigentümer:

rlw immobilien ag
Hofstrasse 106
8620 Wetzikon

Unterschrift Projektverfasser

Unterschrift Bauherr / Grundeigentümer

±0.00 = 717.60 m.ü.M (OK Fertigbelag EG Haus A und B)

Alle Masse sind vom Unternehmer vor der Ausführung am Bau zu nehmen, bzw. zu kontrollieren. Allfällige Differenzen sind unverzüglich mit der Bauleitung zu klären. Falls nicht anders vermerkt sind die Fensterhöhen von OK fertig Boden bis UK Sturz gemessen. Türhöhen sind von OK fertig Boden oder Schwelle bis UK roher Sturz gemessen.

Index	Datum	Geändert von	Änderung
A	26.07.2023	MDS	Planauswechslung / Haus B gespiegelt, gekürzt und 3 m zu Haus A verschoben.

BAUVORHABEN: Überbauung Zumikon
Haus B

ADRESSE: Haldenstrasse 5, 8126 Zumikon
Parzelle 2999

dw design & concept ag

dw design & concept ag
Hofstrasse 106
8620 Wetzikon
Tel: +41 (0)43 477 44 33
info@dw-dc.ch
www.dw-dc.ch

Dieser Plan ist urheberrechtlich geschützt!
Geistiges Eigentum der dw design & concept ag.
Kopieren und weiterverkaufen verboten!

Phase

Plannummer

Planinhalt

Plangröße

gezeichnet

geprüft

freigegeben

BAUEINGABE

115A

Grundrisse
Kubische Berechnung

630x600

Michael Di Stefano

2022-11-17

1:100

9

dw design & concept