


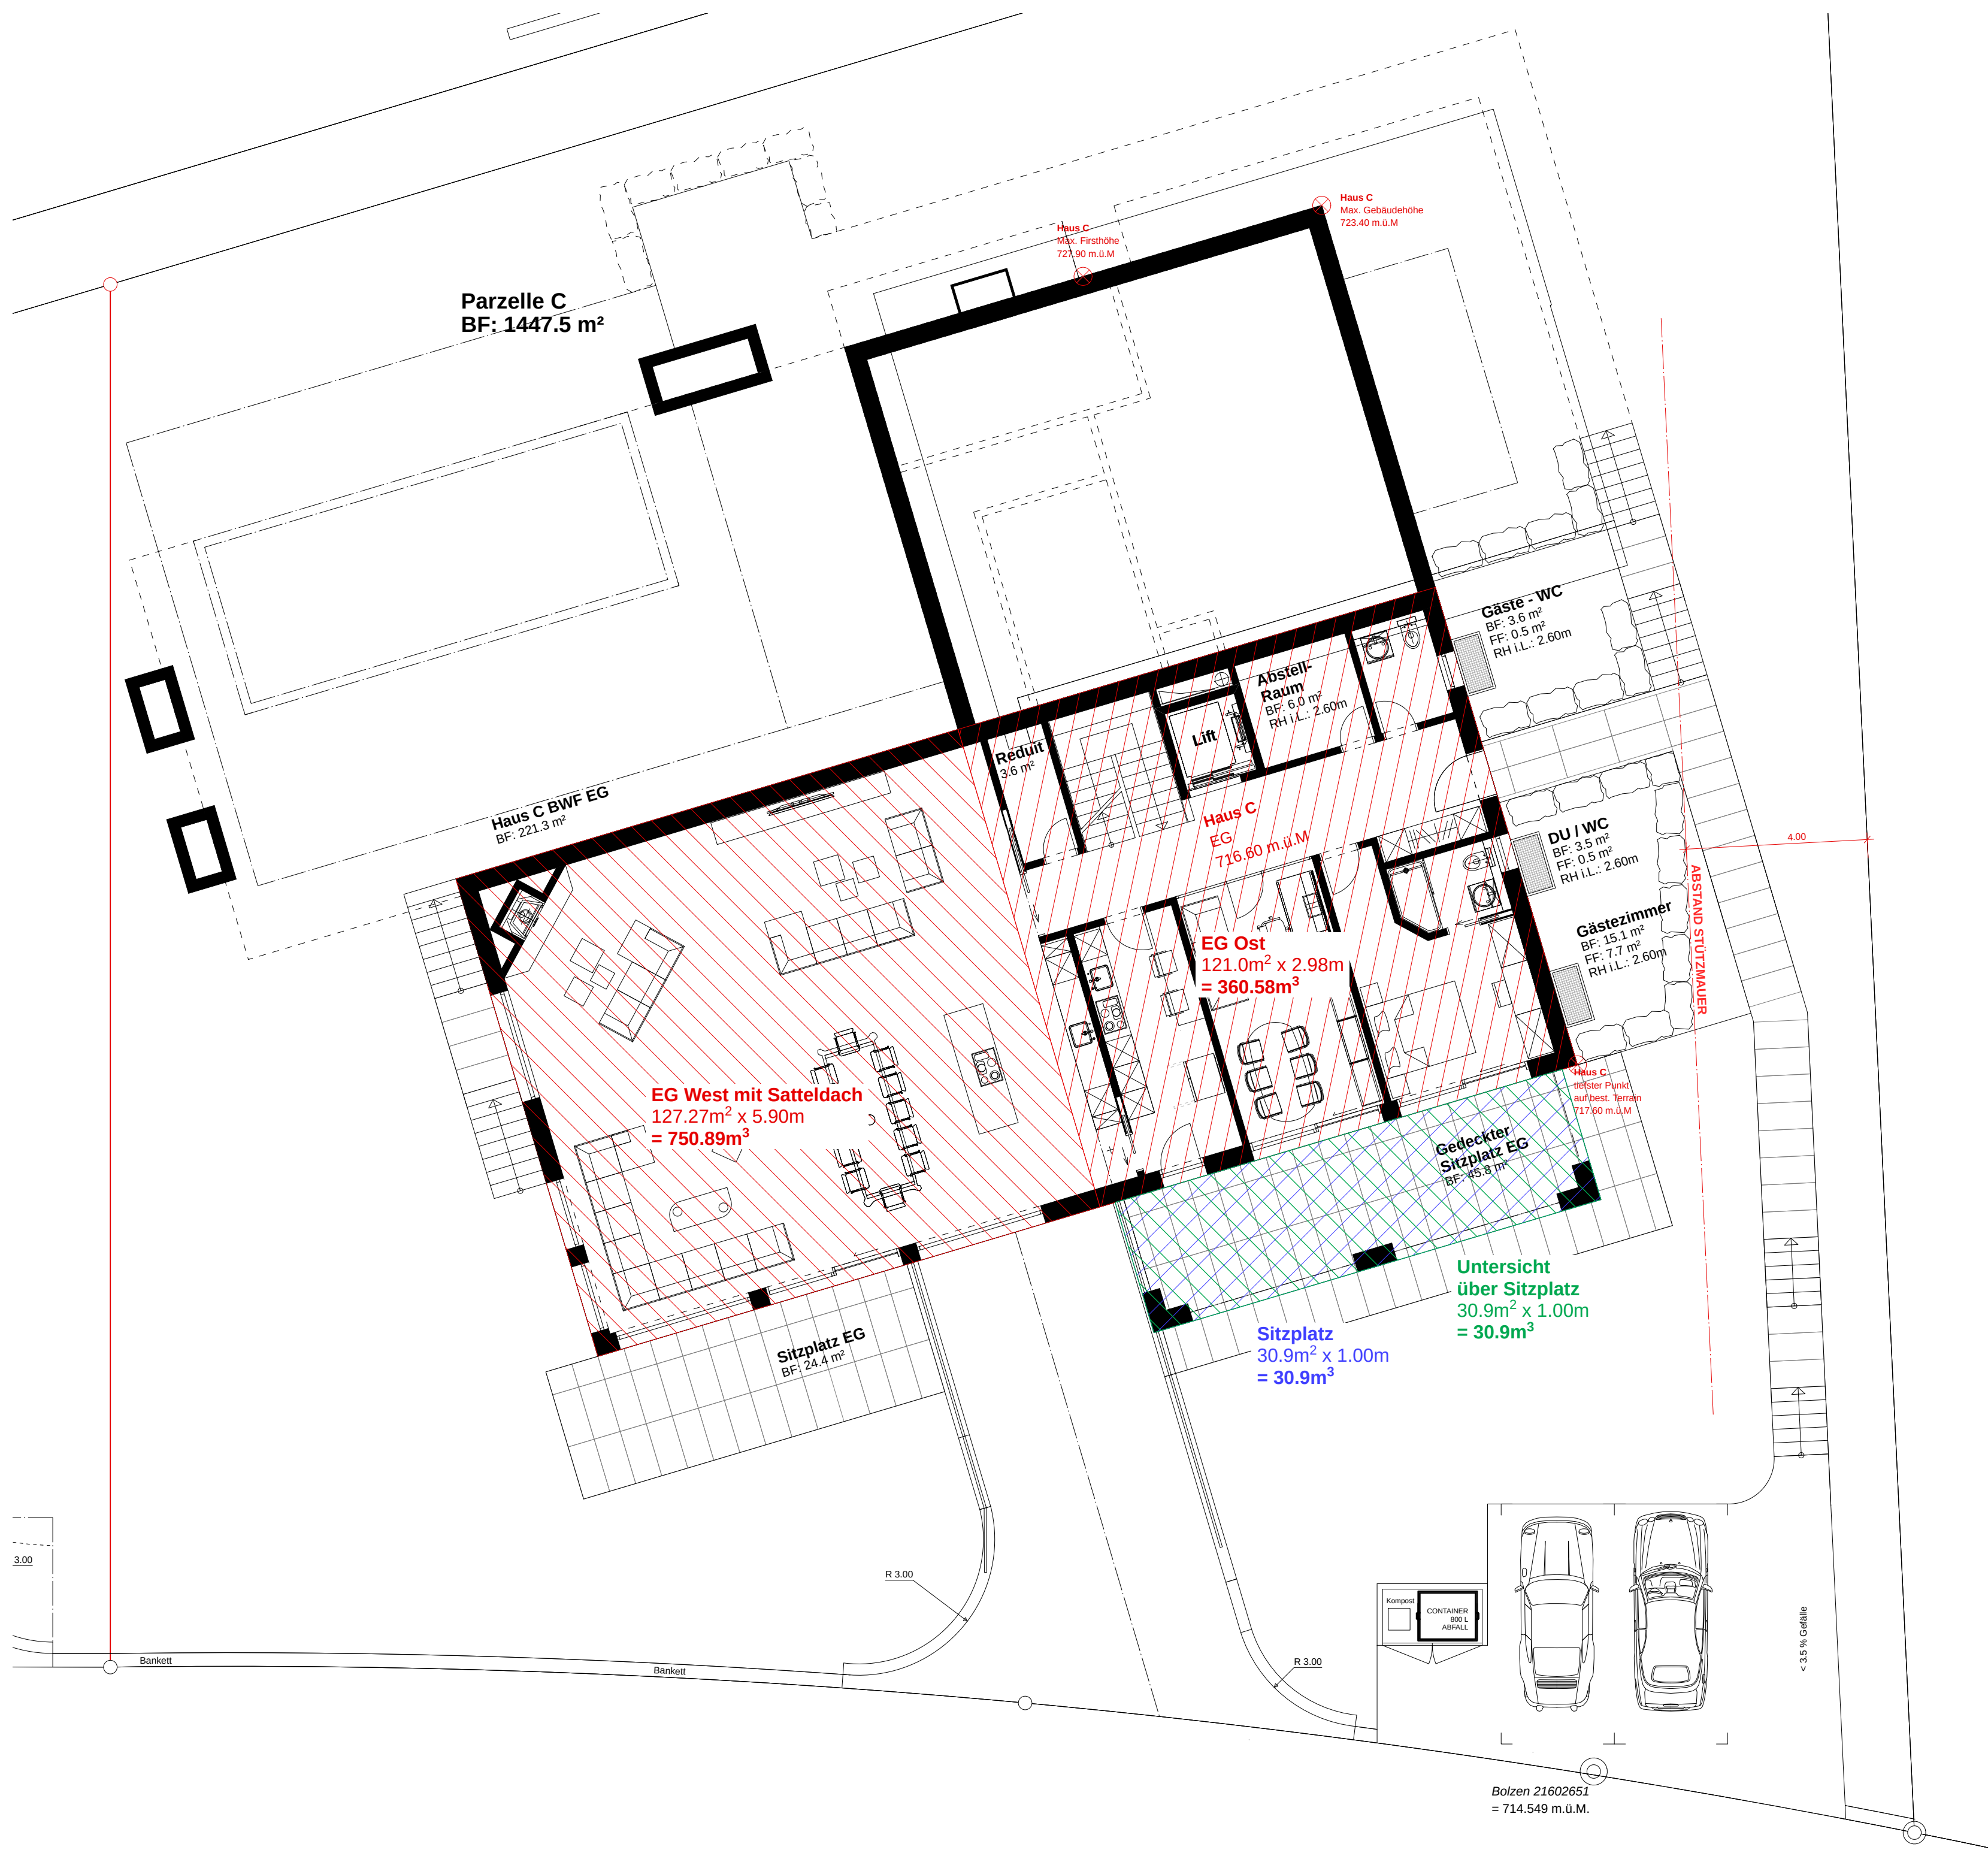

Erdgeschoss



Obergeschoss



Untergeschoss



Dachgeschoss

Projektverfasser:

dw design & concept ag
Haldenstrasse 106
8620 Weiskirchen

Unterschrift Projektverfasser

Bauherr / Grundeigentümer:

ivw Immobilien ag
Haldenstrasse 106
8620 Weiskirchen

Unterschrift Bauherr / Grundeigentümer

±0.00 = 717.60 m.u.M (OK Fertigbelag EG Haus A und B)

Alle Masse sind vom Unternehmer vor der Ausführung am Bau zu nehmen, bzw. zu kontrollieren. Abtätige Differenzen sind unverzüglich mit der Bauleitung zu klären. Falls nicht anders vermerkt sind die Fensterhöhen von OK fertig Boden bis UK Sturz gemessen. Türen sind von OK fertig Boden oder Schwelle bis UK roher Sturz gemessen.

Index	Datum	Geändert von	Änderung
A	26.07.2023	MDS	Planauwechslung 1 kleine Stützmauer Ost, parallel mit 4 m Abstand zur Nachbargr. abgedreht.

BAUVORHABEN: Überbauung Zumikon
Haus C

ADRESSE: Haldenstrasse 5, 8126 Zumikon
Parzelle 2999

dw design & concept

dw design & concept ag
Haldenstrasse 106
8620 Weiskirchen

Tel: +41 (0)43 477 44 33

info@dw-dc.ch
www.dw-dc.ch

Phase
EG

Plannummer
116A

Planinhalt
Grundrisse
Kubische Berechnung

Plangröße	Name	Datum	Massstab
1:100	Michael O. Suter	2023.07.27	

Dieser Plan ist urheberrechtlich geschützt.
Geistiges Eigentum der dw design & concept ag.
Kopieren und Weiterverbreiten ist verboten.

BAUEINGABE

gezeichnet
geprüft
freigegeben

1:100