


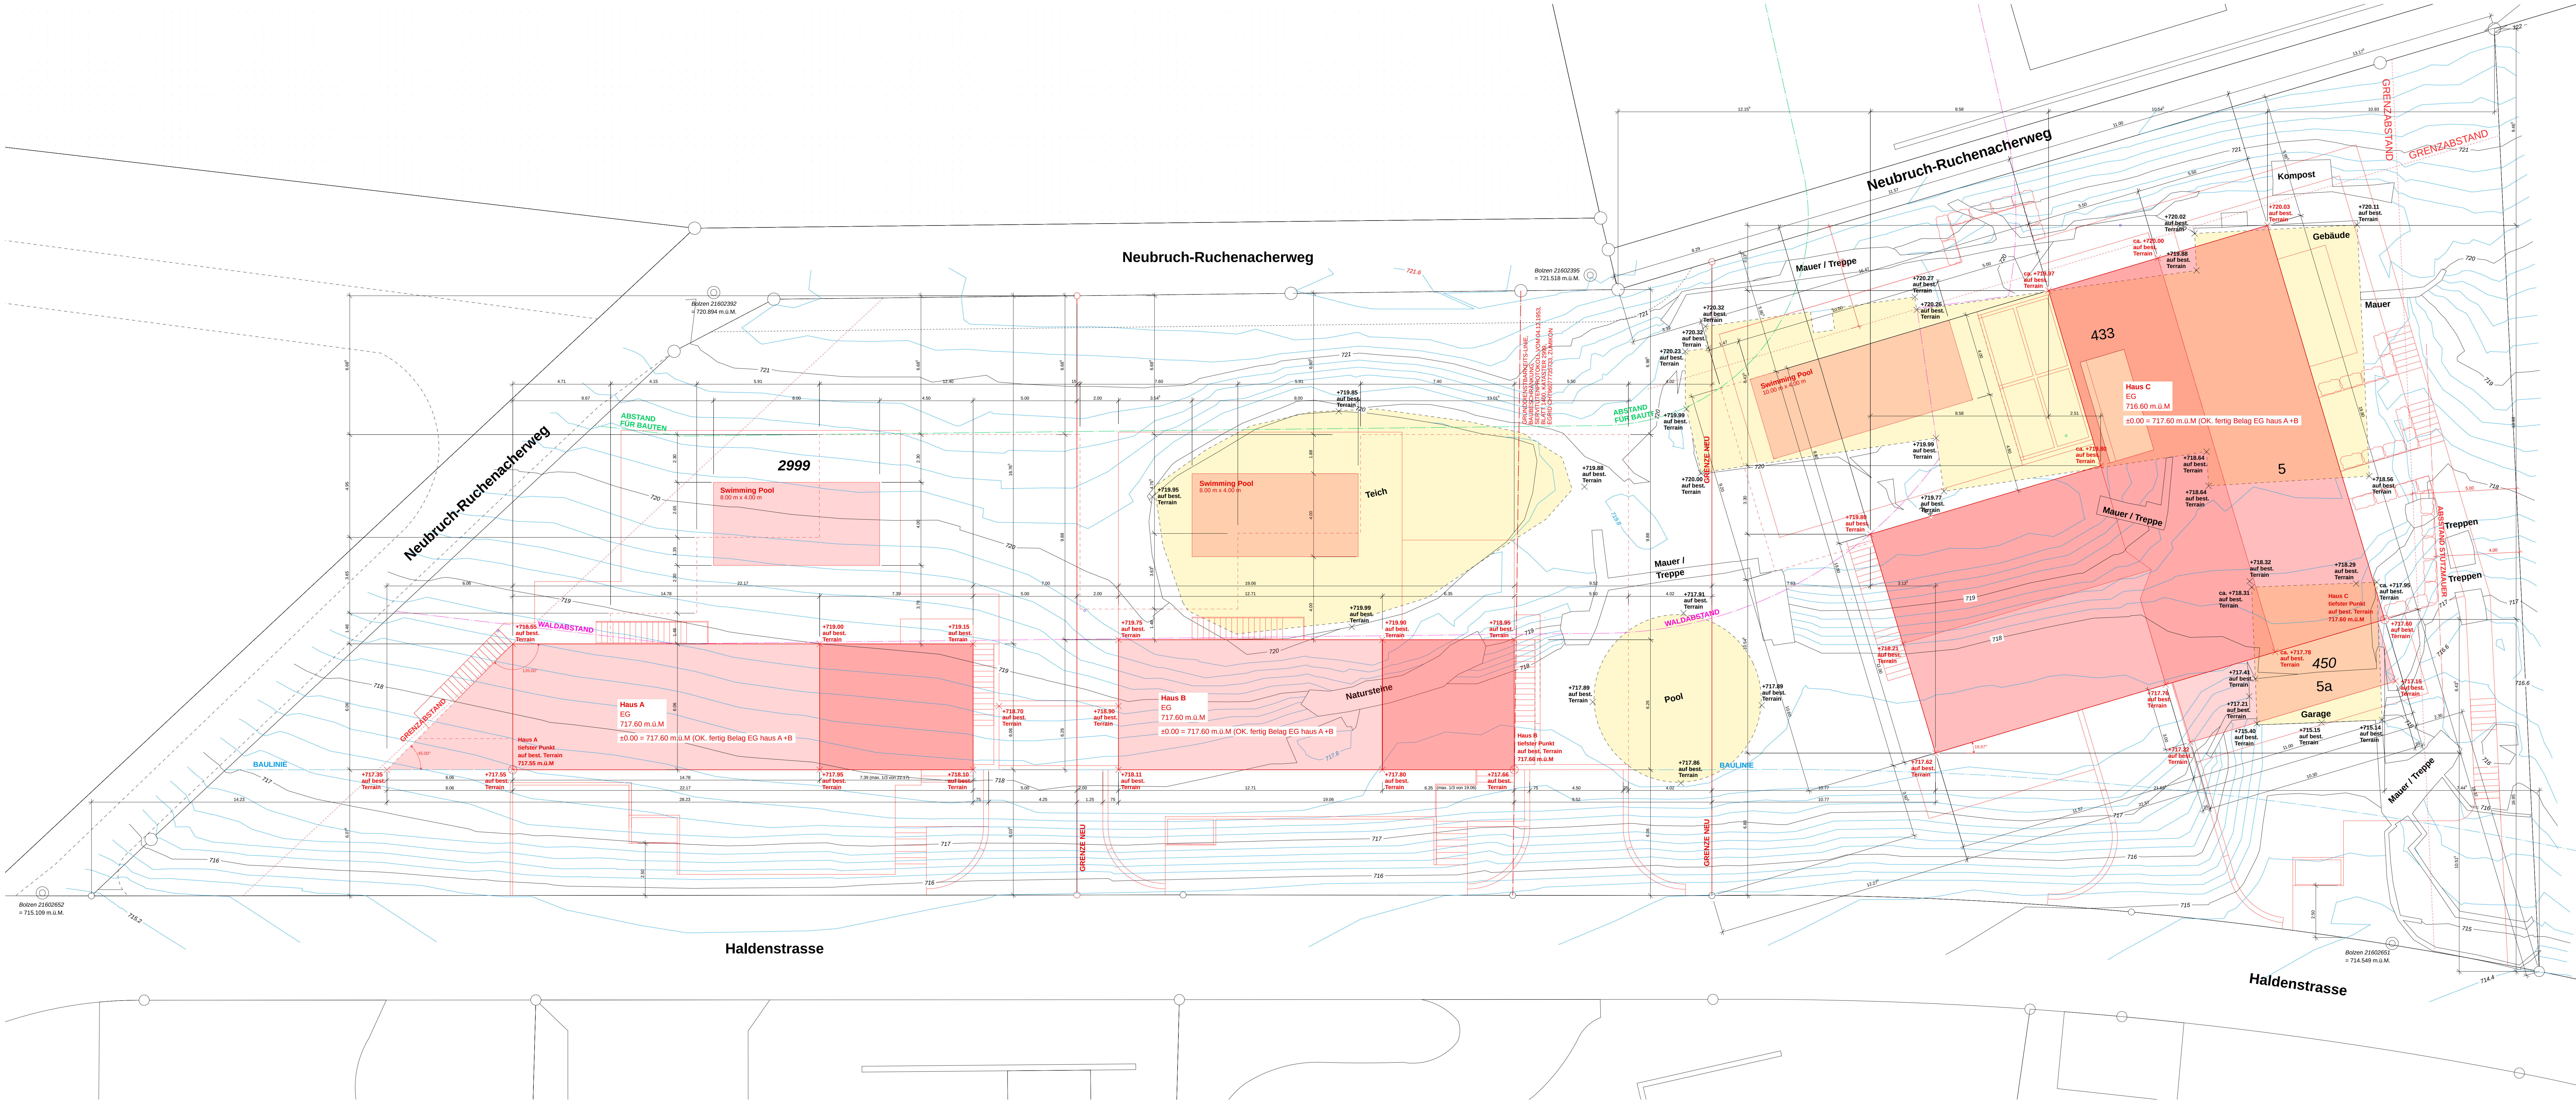

Projektverfasser:

dw design & concept ag
Haldenstrasse 106
8620 Wetzikon

Bauherr / Grundeigentümer:

dw Immobilien ag
Haldenstrasse 106
8620 Wetzikon

Unterschrift Projektverfasser

Unterschrift Bauherr / Grundeigentümer

Legende:

Projektirtes Bauvorhaben an der Haldenstrasse 5, 8126 Zumikon, Parzelle 2999

Abbruch der bestehenden Bauten (Gebäude, Garage, Pool, Teich).

Bestehende Höhenkoten Gew. Terrain (Jetziges Terrain bestehend).

Bestehende Höhenlinien gemäss amtlicher Vermessung der Gossweiler Ingenieure AG, Dorfplatz 1, 8126 Zumikon.

±0.00 = 717.60 m.ü.M (OK Fertigbelag EG Haus A und B)

Alle Masse sind vom Unternehmer vor der Ausführung am Bau zu nehmen, bzw. zu kontrollieren. Alltägliche Differenzen sind unverzüglich mit der Bauleitung zu klären. Falls nicht anders vermerkt sind die Fensterhöhen von OK fertig Boden bis UK Sturz gemessen. Türhöhen sind von OK fertig Boden oder Schwelle bis UK roher Sturz gemessen.

Index	Datum	Gedändert von	Änderung

BAUVORHABEN: Überbauung Zumikon

ADRESSE: Haldenstrasse 5, 8126 Zumikon
Parzelle 2999

dw design & concept

dw design & concept ag
Haldenstrasse 106
8620 Wetzikon

Tel: +41 (0)43 477 44 33

info@dw-dc.ch
www.dw-dc.ch

Dieser Plan ist urheberrechtlich geschützt!
Copyright Eigentum der dw design & concept ag.
Kopieren und weiterverkaufen verboten!

Phase	BAUEINGABE		
Plannummer	121		
Planinhalt	Bestehende Höhenkurven mit eingezeichnetem Bauvorhaben		
Plangröße	147x60		
Name	Datum	Maßstab	
gezeichnet	Michael Di Stefano	2023-06-30	1:100
geprüft			
freigegeben			