


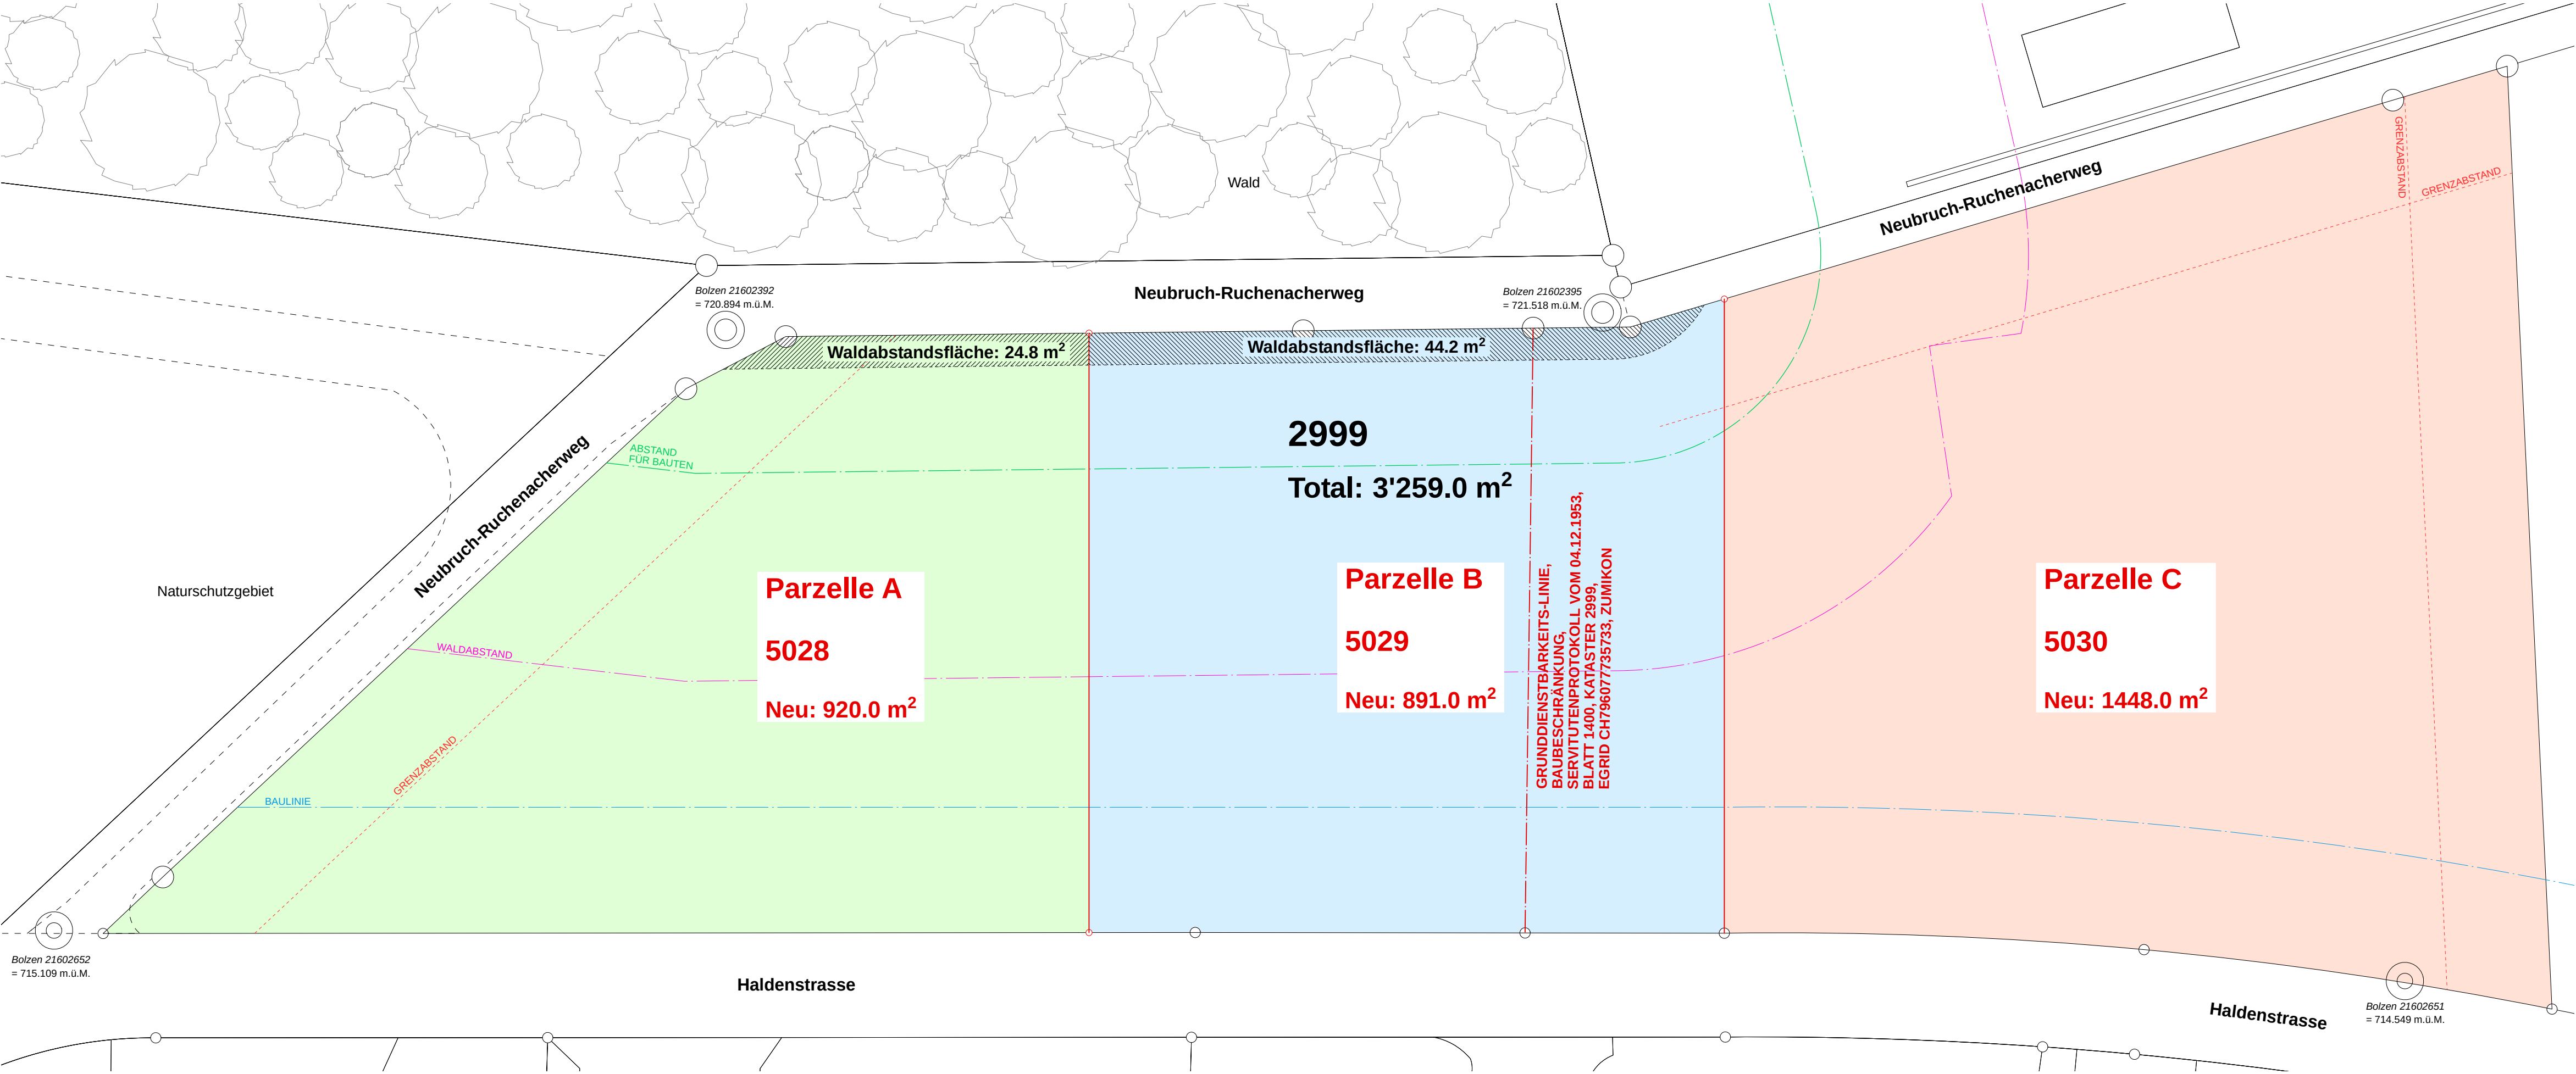

Projektverfasser:

dw design & concept ag
Hofstrasse 106
8620 Wetzikon

Unterschrift Projektverfasser

Bauherr / Grundeigentümer:

rlw immobilien ag
Hofstrasse 106
8620 Wetzikon

Unterschrift Bauherr / Grundeigentümer


±0.00 = 717.60 m.ü.M (OK Fertigbelag EG Haus A und B)

Alle Masse sind vom Unternehmer vor der Ausführung am Bau zu nehmen, bzw. zu kontrollieren. Allfällige Differenzen sind unverzüglich mit der Bauleitung zu klären. Falls nicht anderst vermerkt sind die Fensterhöhen von OK fertig Boden bis UK Sturz gemessen. Türhöhen sind von OK fertig Boden oder Schwelle bis UK roher Sturz gemessen.

Index	Datum	Geändert von	Änderung
A	05.10.2023	MDS	Aufteilung und Grundstücksflächen nach Gossweiler Ingenieure AG angepasst.

BAUVORHABEN: Überbauung Zumikon

ADRESSE: Haldenstrasse 5, 8126 Zumikon
Parzelle 2999

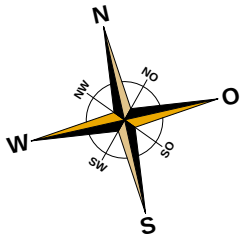

dw design & concept ag dw design & concept ag Hofstrasse 106 8620 Wetzikon Tel: +41 (0)43 477 44 33 info@dw-dc.ch www.dw-dc.ch Dieser Plan ist urheberrechtlich geschützt! Geistiges Eigentum der dw design & concept ag. Kopieren und weiterverkaufen verboten!	Phase	BAUEINGABE		
	Plannummer	122A		
	Planinhalt	Parzellierungsplan -Aufteilung der Parzelle 2999 in neu 3 Parzellen		
	Plangröße	84x30		
	gezeichnet	Name	Datum	Maßstab
	geprüft	Michael Di Stefano	2023-09-18	1:200
	freigegeben			