


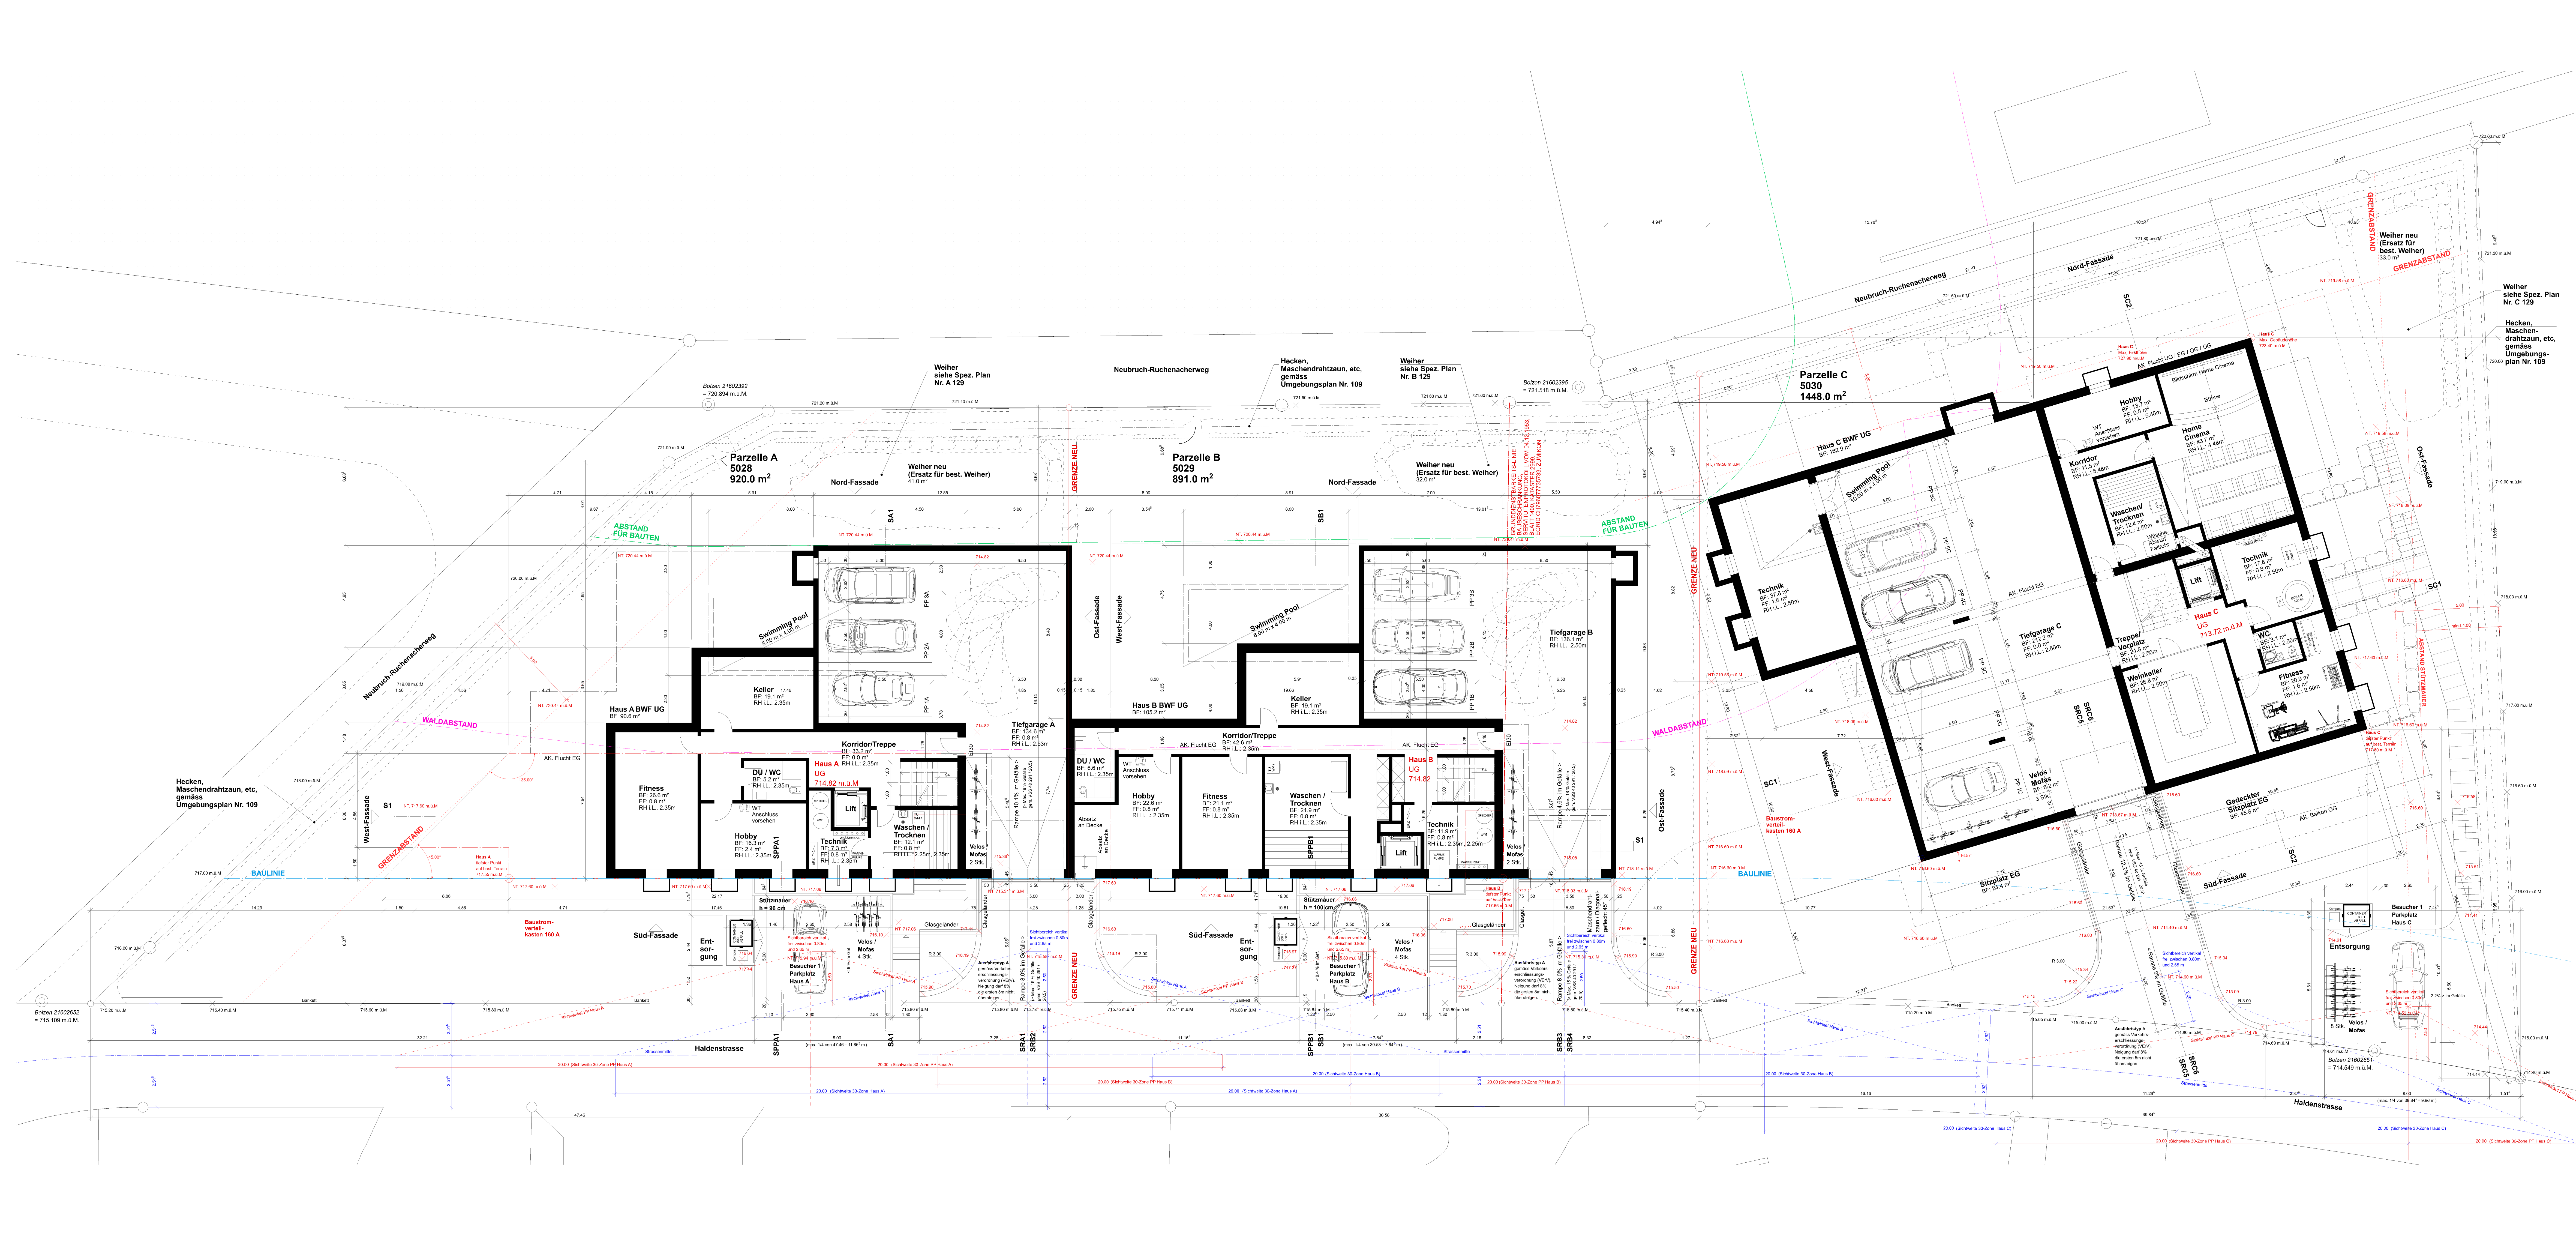

Projektverfasser:

dw design & concept ag
Haldenstrasse 106
8620 Wetzikon

Bauherr / Grundeigentümer:

dw Immobilien ag
Haldenstrasse 106
8620 Wetzikon

Unterschrift Projektverfasser

Unterschrift Bauherr / Grundeigentümer

±0.00 = 717.60 m ü.M. (OK Fertigbelag EG Haus A und B)

Alle Masse sind vom Unternehmer vor der Ausführung am Bau zu nehmen, bzw. zu kontrollieren. Abfällige Differenzen sind unverzüglich mit der Bauleitung zu klären. Falls nicht anders vermerkt sind die Fensterhöhen von OK fertig Boden bis UK Sturz gemessen. Türen sind von OK fertig Boden oder Schwelle bis UK Roh Sturz gemessen.

Index	Datum	Geändert von	Änderung
A	13.02.2023	MDS	Planauwechslung /
B	26.07.2023	MDS	Balkonstutzen / Haus C Format angepasst und Sitzplatz um eine Plattenreihe verkörtzt
C	27.02.2024	MDS	Planauwechslung / Haus B gespiegelt, gelöst und 3 m zu Haus A verschoben.
D	17.06.2024	MDS	Haus C: Keine Stützmauer Ost, parallel mit 4 m Abstand zur Nachbargrenze abgedreht.
E	26.07.2024	MDS	Einfahrtsrampen und Parkplätze angepasst. Garageneinfahrt Haus B bei Keller korrigiert.
F	26.07.2024	MDS	Lichtschacht und Kellerfenster bei Keller Haus A entfernt.
G	26.07.2024	MDS	Weiler A / B / C eingezeichnet.

BAUVORHABEN: Überbauung Zumikon

ADRESSE: Haldenstrasse 5, 8126 Zumikon
Parzelle 2999

dw design & concept
ag

dw design & concept ag
Haldenstrasse 106
8620 Wetzikon

Tel: +41 (0)43 477 44 33

info@dw-do.ch
www.dw-do.ch

Dieser Plan ist urheberrechtlich geschützt!
Geistiges Eigentum der dw design & concept ag.
Kopieren und weiterverbreiten verboten!

Phase

Plannummer

Planinhalt

Plangröße

gezeichnet

freigegeben

BAUFREIGABE

102E

Revidierter
Grundriss
Untergeschoss

Name	Datum	Maßstab
Michael D. Suter	2022-11-17	1:100