


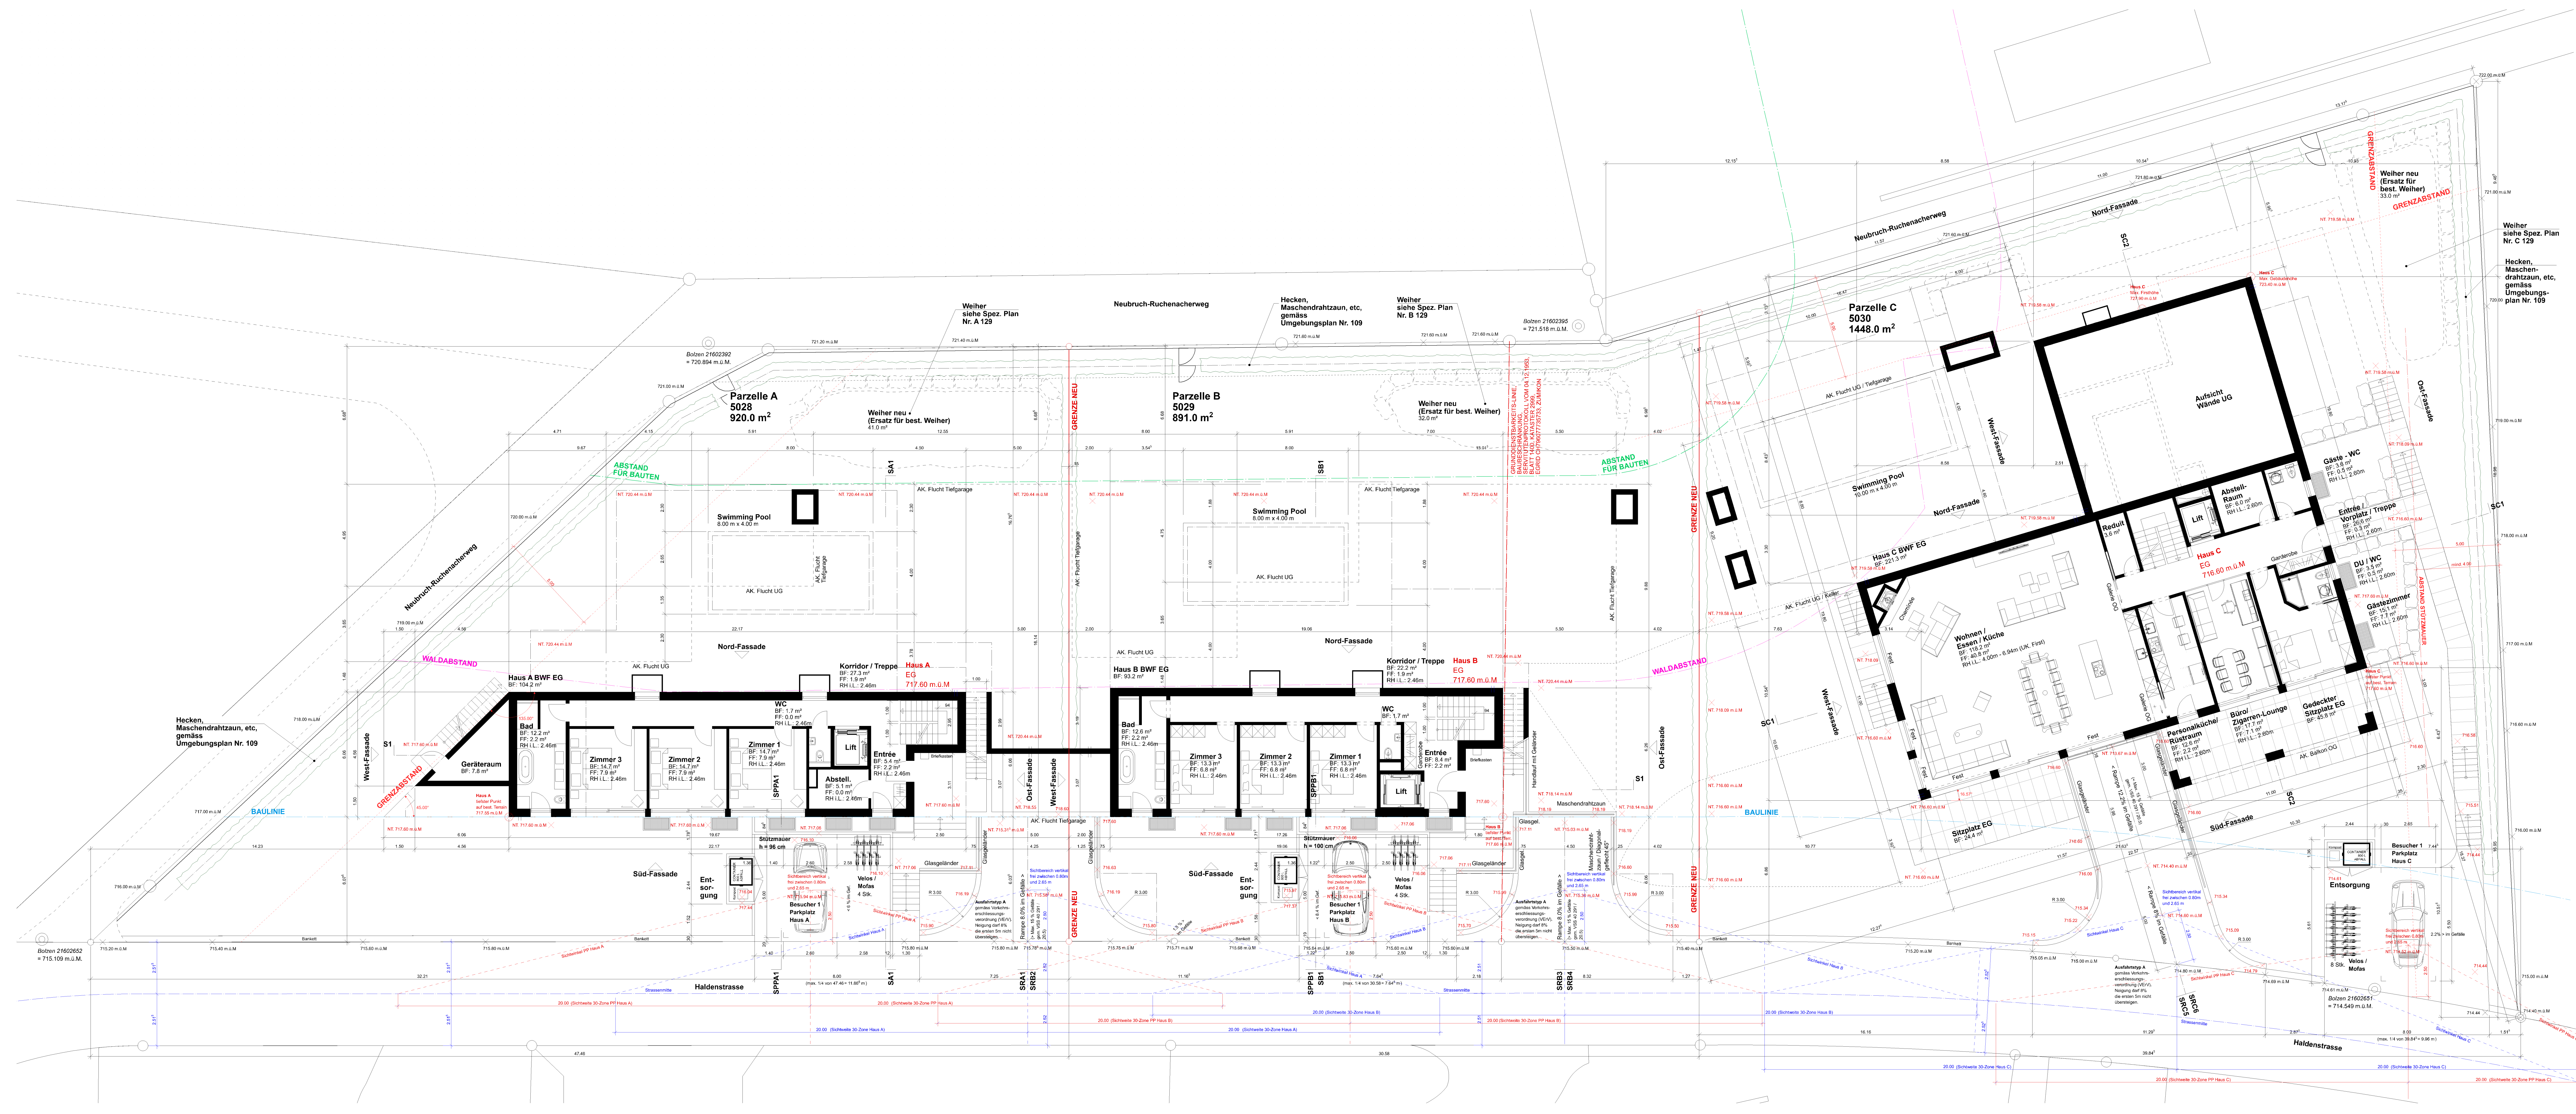

Projektverfasser:

dw design & concept ag
Haldenstrasse 106
8620 Wetzikon

Bauherr / Grundeigentümer:

dw Immobilien ag
Haldenstrasse 106
8620 Wetzikon

Unterschrift Projektverfasser

Unterschrift Bauherr / Grundeigentümer

±0.00 = 717.60 m.ü.M (OK Fertigbelag EG Haus A und B)

Alle Masse sind vom Unternehmer vor der Ausführung am Bau zu nehmen, bzw. zu kontrollieren. Abfällige Differenzen sind unverzüglich mit der Bauleitung zu klären. Falls nicht anders vermerkt sind die Fensterhöhen von OK fertig Boden bis UK Sturz gemessen. Türenhöhen sind von OK fertig Boden oder Schwelle bis UK ohne Sturz gemessen.

Index	Datum	Geändert von	Änderung
A	13.02.2023	MDS	Planwechsel /
B	26.07.2023	MDS	Balkonstufen / Haus C Format angepasst und Sitzplatz um eine Plattenreihe verköhrt
C	27.02.2024	MDS	Planwechsel / Haus B gespiegelt, gelöst und 3 m zu Haus A verschoben.
D	26.07.2024	MDS	Haus C: keine Stützmauer Ost, parallel mit 4 m Abstand zur Nachbargrenze abgedingt.
			Einfahrtstrampen und Parkplatz angepasst. Garagenflucht Haus B bei Keller geneigt.
			Weiler A / B / C eingezeichnet.

BAUVORHABEN: Überbauung Zumikon

ADRESSE: Haldenstrasse 5, 8126 Zumikon
Parzelle 2999

dw design & concept ag

Phase

Plannummer

Planinhalt

Plangröße

gezeichnet

geprüft

freigegeben

BAUFREIGABE

103D

Revidierter Grundriss Erdgeschoss

Name

Datum

Maßstab

1:100

dw design & concept ag
Haldenstrasse 106
8620 Wetzikon

Tel: +41 (0)43 477 44 33

info@dw-do.ch
www.dw-do.ch

Dieser Plan ist urheberrechtlich geschützt!
Copyright Eigentum der dw design & concept ag.
Kopieren und weiterverbreiten verboten!