


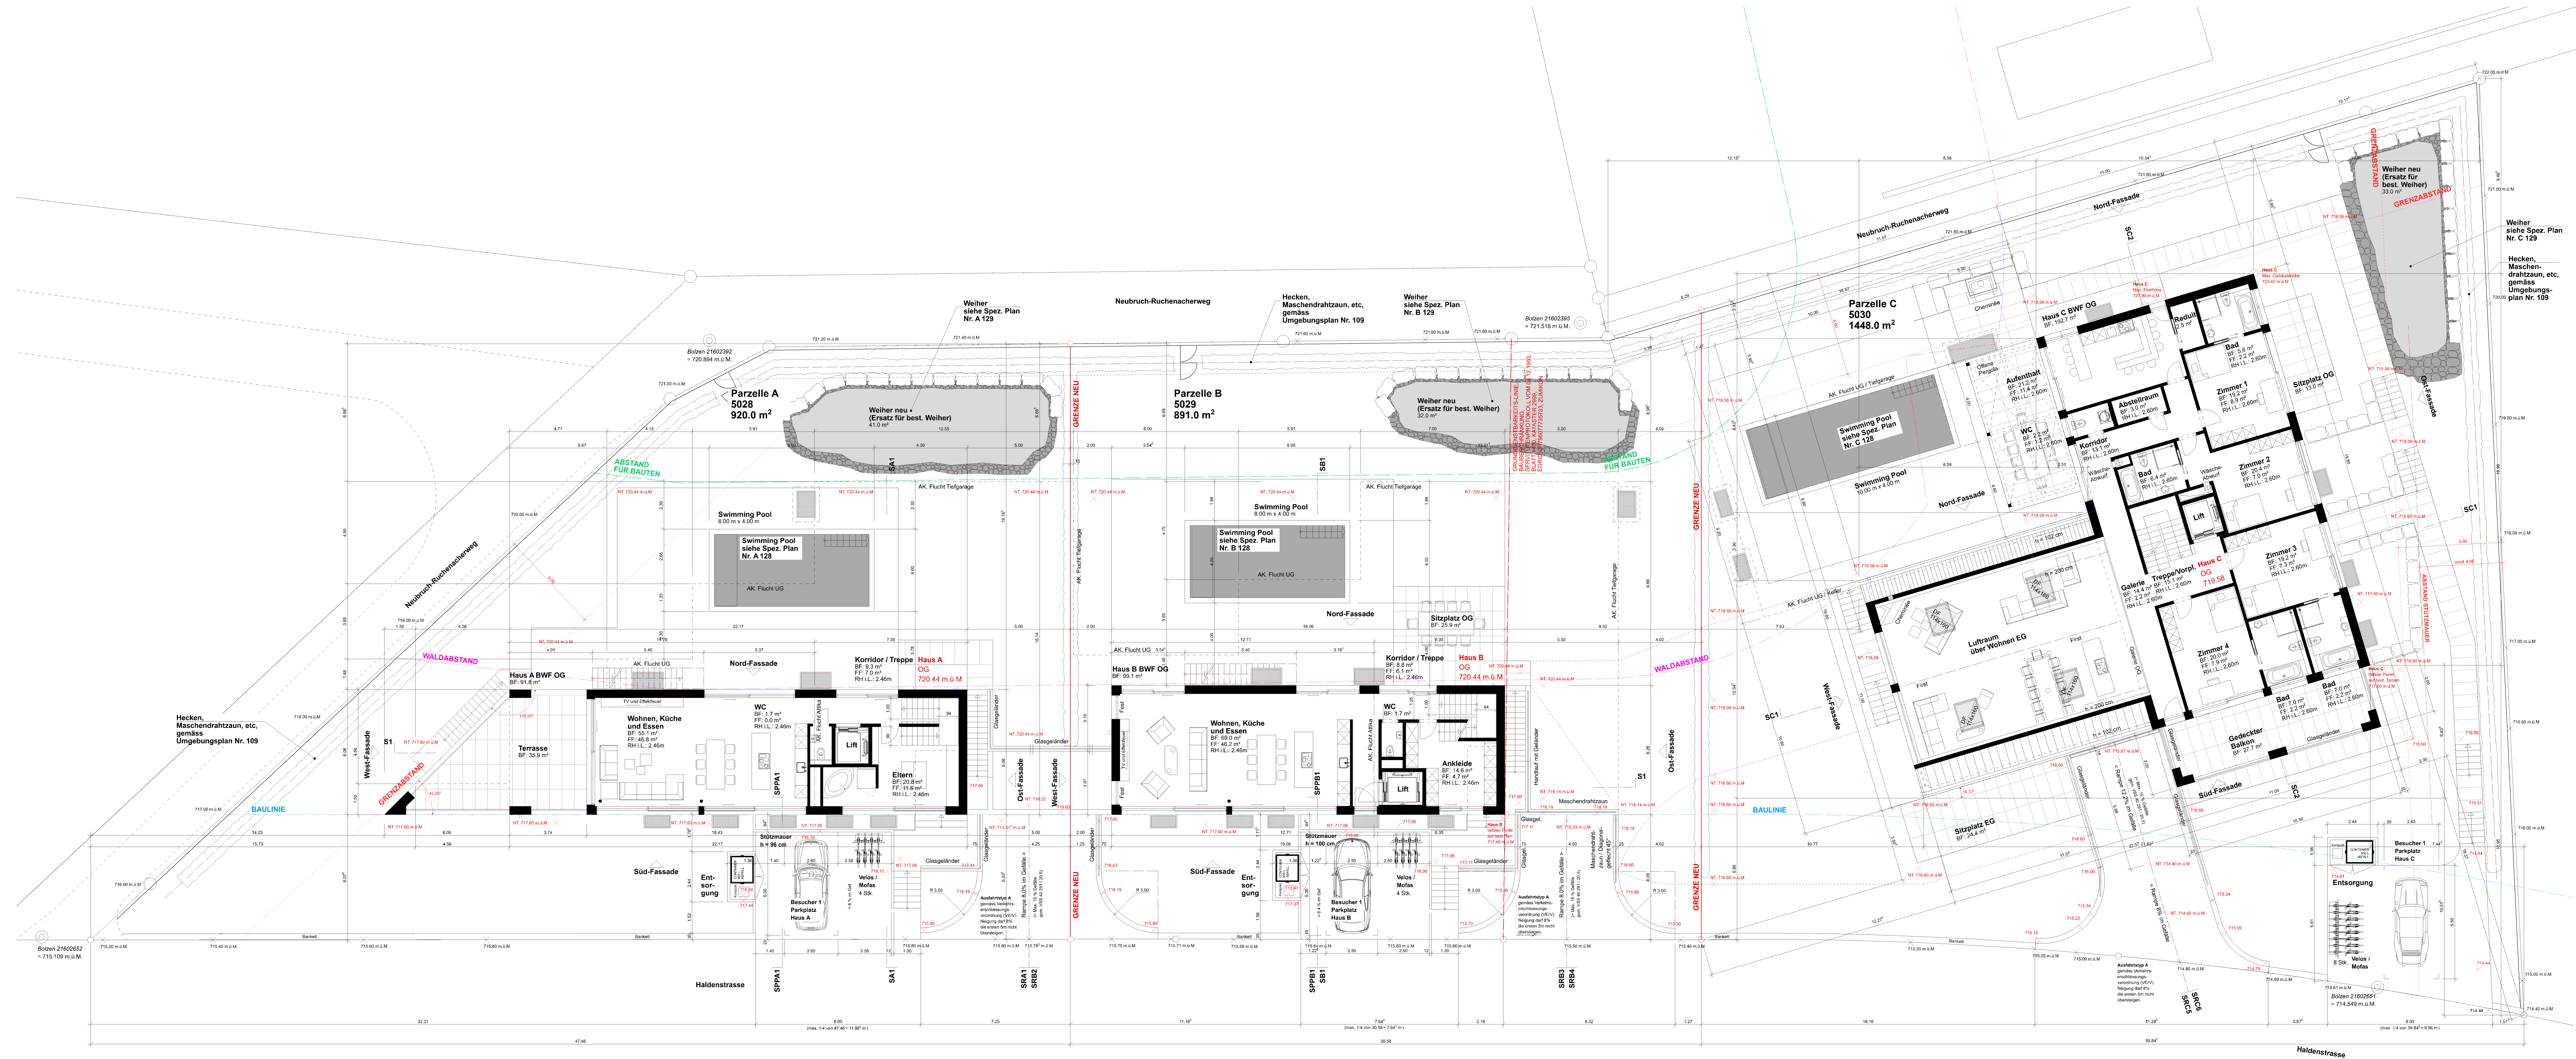

**Projektverfasser:**

dw design & concept ag  
Haldenstrasse 106  
8620 Wetzikon

**Bauherr / Grundeigentümer:**

dw Immobilien ag  
Haldenstrasse 106  
8620 Wetzikon

Unterschrift Projektverfasser

Unterschrift Bauherr / Grundeigentümer

±0.00 = 717.60 m ü.M (OK Fertigbelag EG Haus A und B)

Alle Masse sind vom Unternehmer vor der Ausführung am Bau zu nehmen, bzw. zu kontrollieren. Abfällige Differenzen sind unverzüglich mit der Bauleitung zu klären. Falls nicht anders vermerkt sind die Fensterhöhen von OK fertig Boden bis UK Sturz gemessen. Türen sind von OK fertig Boden oder Schwelle bis UK roher Sturz gemessen.

| Index | Datum      | Geändert von | Änderung   |
|-------|------------|--------------|---|
| A     | 13.02.2023 | MDS          | Planauswechslung / Balkonsstützen Haus C Format angepasst und Stützpl. um eine Plattform verkörtzt   |
| B     | 26.07.2023 | MDS          | Erdeplätze im OG bei Terrasse Haus A angepasst<br>Planauswechslung / Haus B gespiegelt, gestützt und 3 m zu Haus A verschoben.<br>Haus C: keine Stützmauer Ost, parallel mit 4 m Abstand zur Nachbargrenze abgedreht. |
| C     | 05.10.2023 | MDS          | Planauswechslung / Grundstück: angepasst, kleine Vergrösserung Abstell. Übergesch. Haus C   |
| D     | 27.02.2024 | MDS          | Einfahrtsrampen und Parkplätze angepasst. Garageneinfahrt Haus B bei Keller korrigiert.   |
| E     | 26.07.2024 | MDS          | Weilher A / B / C eingezeichnet.   |

**BAUVORHABEN:** Überbauung Zumikon

**ADRESSE:**

Haldenstrasse 5, 8126 Zumikon  
Parzelle 2999

**dw design & concept**

ag

dw design & concept ag  
Haldenstrasse 106  
8620 Wetzikon

Tel: +41 (0)43 477 44 33  
info@dw-dc.ch  
www.dw-dc.ch

**BAUFREIGABE**

Plannummer: 104E  
Planinhalt: Revidierter Grundriss Obergeschoss

| Plangröße | Name             | Datum      | Maßstab |
|-----------|------------------|------------|---------|
| 60147     | Michael D. Suter | 2022-11-17 | 1:100   |

Dieser Plan ist urheberrechtlich geschützt!  
Geistiges Eigentum der dw design & concept ag.  
Kopieren und weiterverbreiten verboten!