


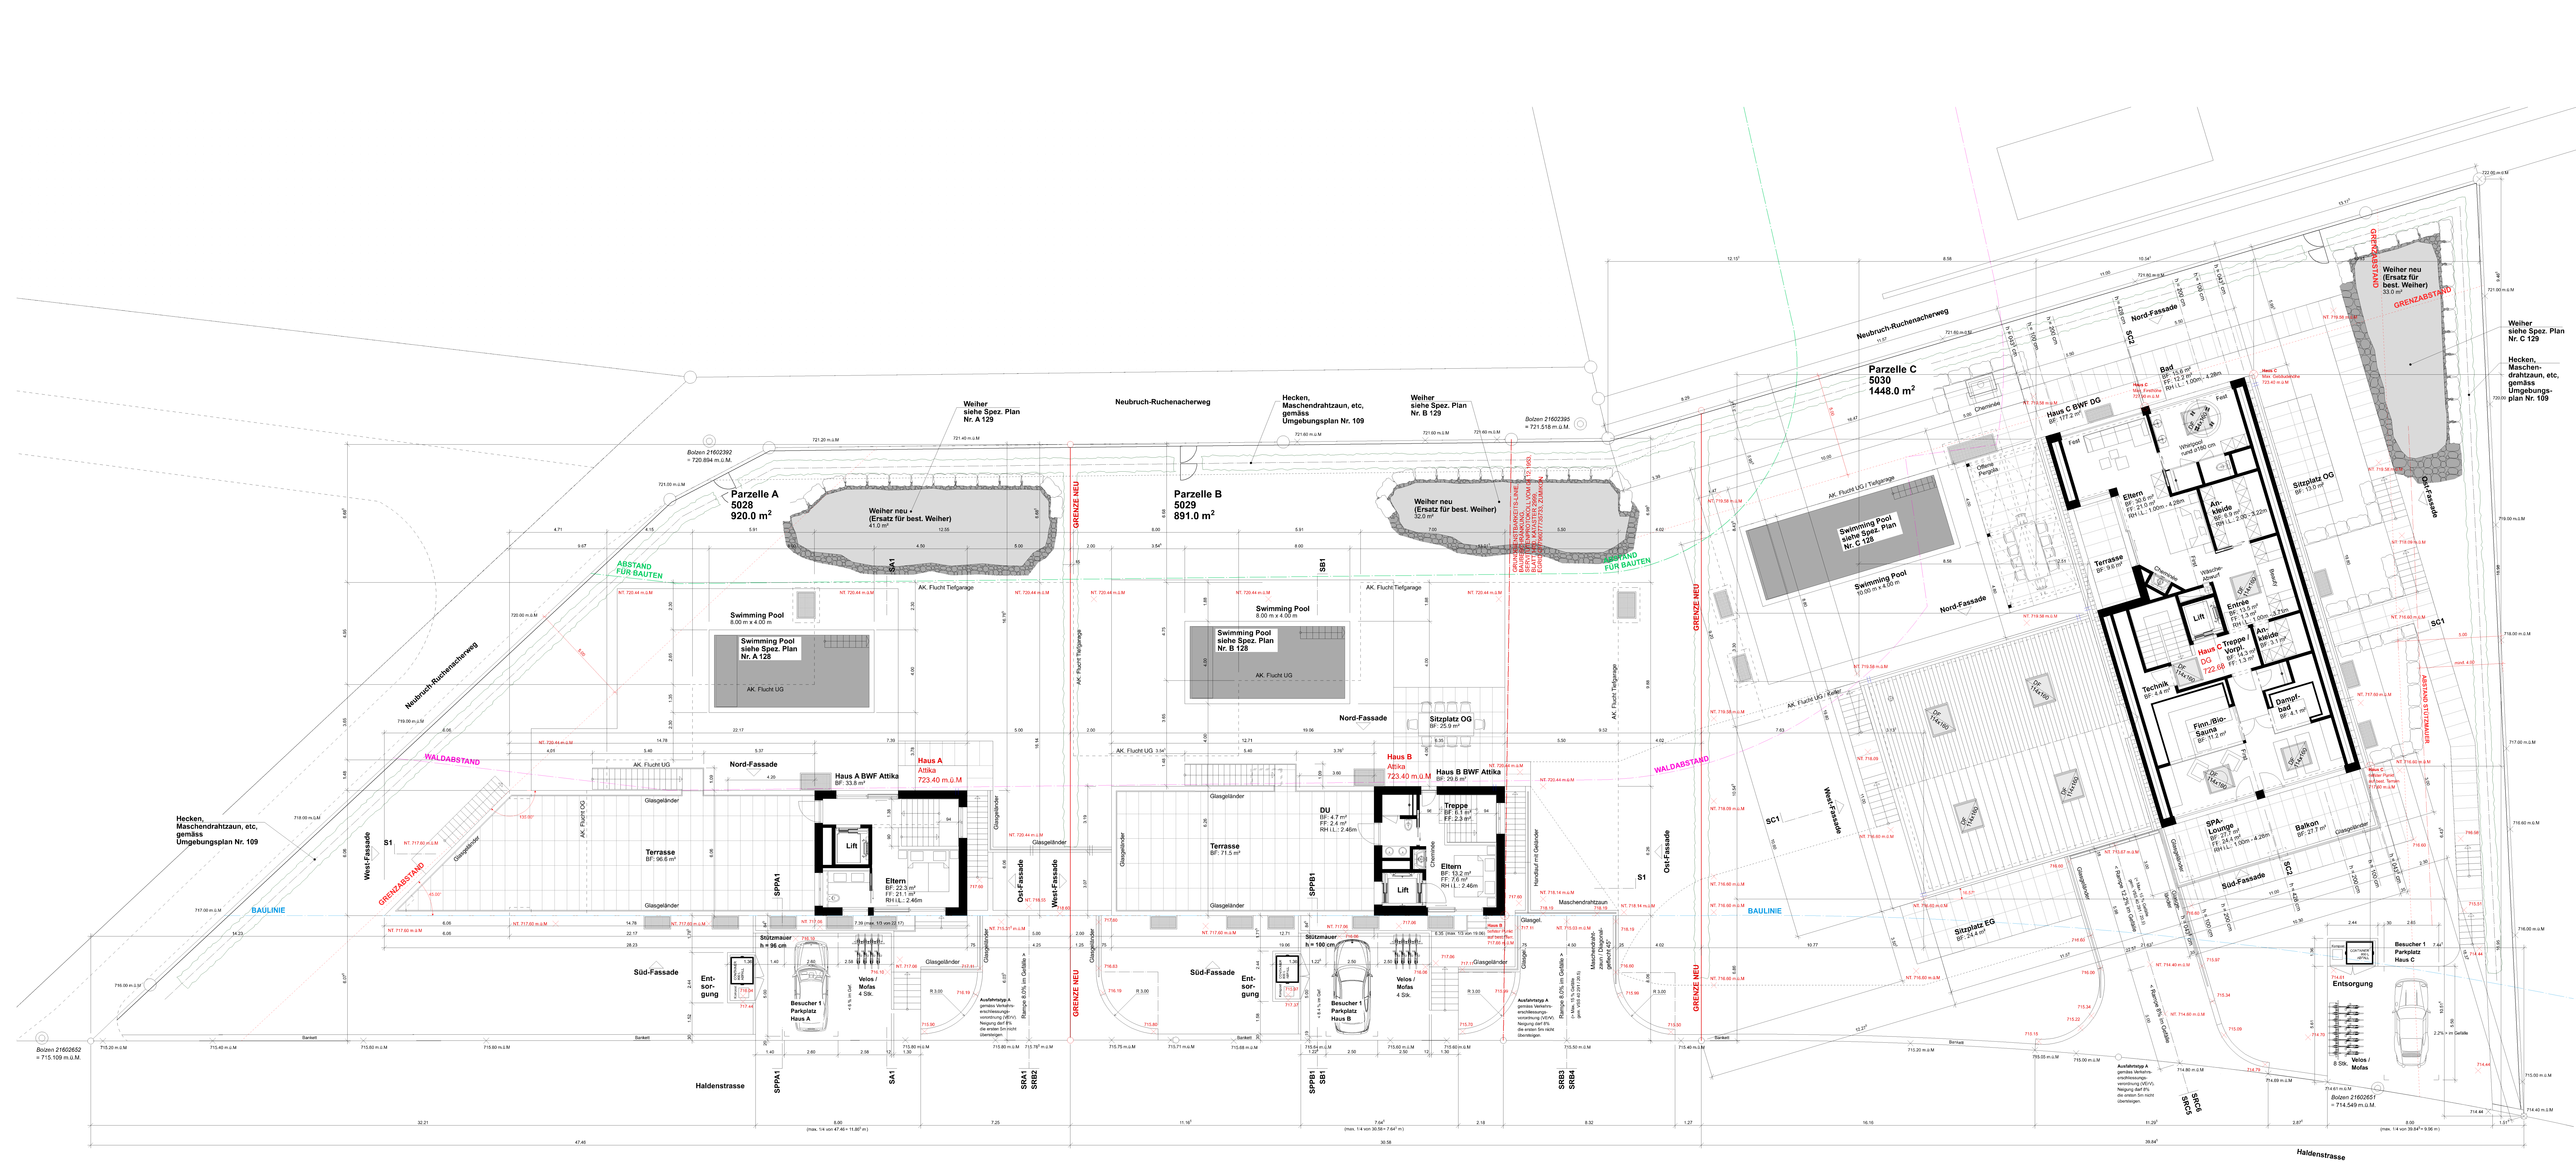

Projektverfasser:
dw design & concept ag
Haldenstrasse 106
8620 Wetzikon

Bauherr / Grundeigentümer:
dw Immobilien ag
Haldenstrasse 106
8620 Wetzikon

Unterschrift Projektverfasser

Unterschrift Bauherr / Grundeigentümer

Index

Index	Datum	Geändert von	Änderung
A	13.02.2023	MDS	Planwechsel / Balkonsterrasse / Haus C Format angepasst und Sitzplatz um eine Plattenreihe verkurzt Eintrittsstütze im OG bei Terrasse Haus A angepasst
B	26.07.2023	MDS	Planwechsel / Haus B gespiegelt, gekürzt und 3 m zu Haus A verschoben. Haus C, kleine Stützmauer Ost, parallel mit 4 m Abstand zur Nachbargrenze abgedruckt.
C	27.02.2024	MDS	Eintrittsrampen und Parkplätze angepasst. Garagenlicht Haus B bei Keller korrigiert.
D	26.07.2024	MDS	Weiter A / B / C eingezeichnet.

BAUVORHABEN: Überbauung Zumikon

ADRESSE:
Haldenstrasse 5, 8126 Zumikon
Parzelle 2999

dw design & concept
ag

dw design & concept ag
Haldenstrasse 106
8620 Wetzikon
Tel: +41 (0)43 477 44 33
info@dw-do.ch
www.dw-do.ch
Dieser Plan ist urheberrechtlich geschützt!
Copyright Eigentum der dw design & concept ag.
Kopieren und Weiterverbreiten verboten!

Phase	Plannummer	Planinhalt	Plangröße	Name	Datum	Maßstab
BAUFREIGABE	105D	Revidierter Grundriss Attika Haus A / B Dachgeschoss Haus C	60147			
		gezeichnet		Michael D. Suter	2022-11-17	
		freigegeben				

1:100