




S1 (Längsschnitt Haus A-B-C)

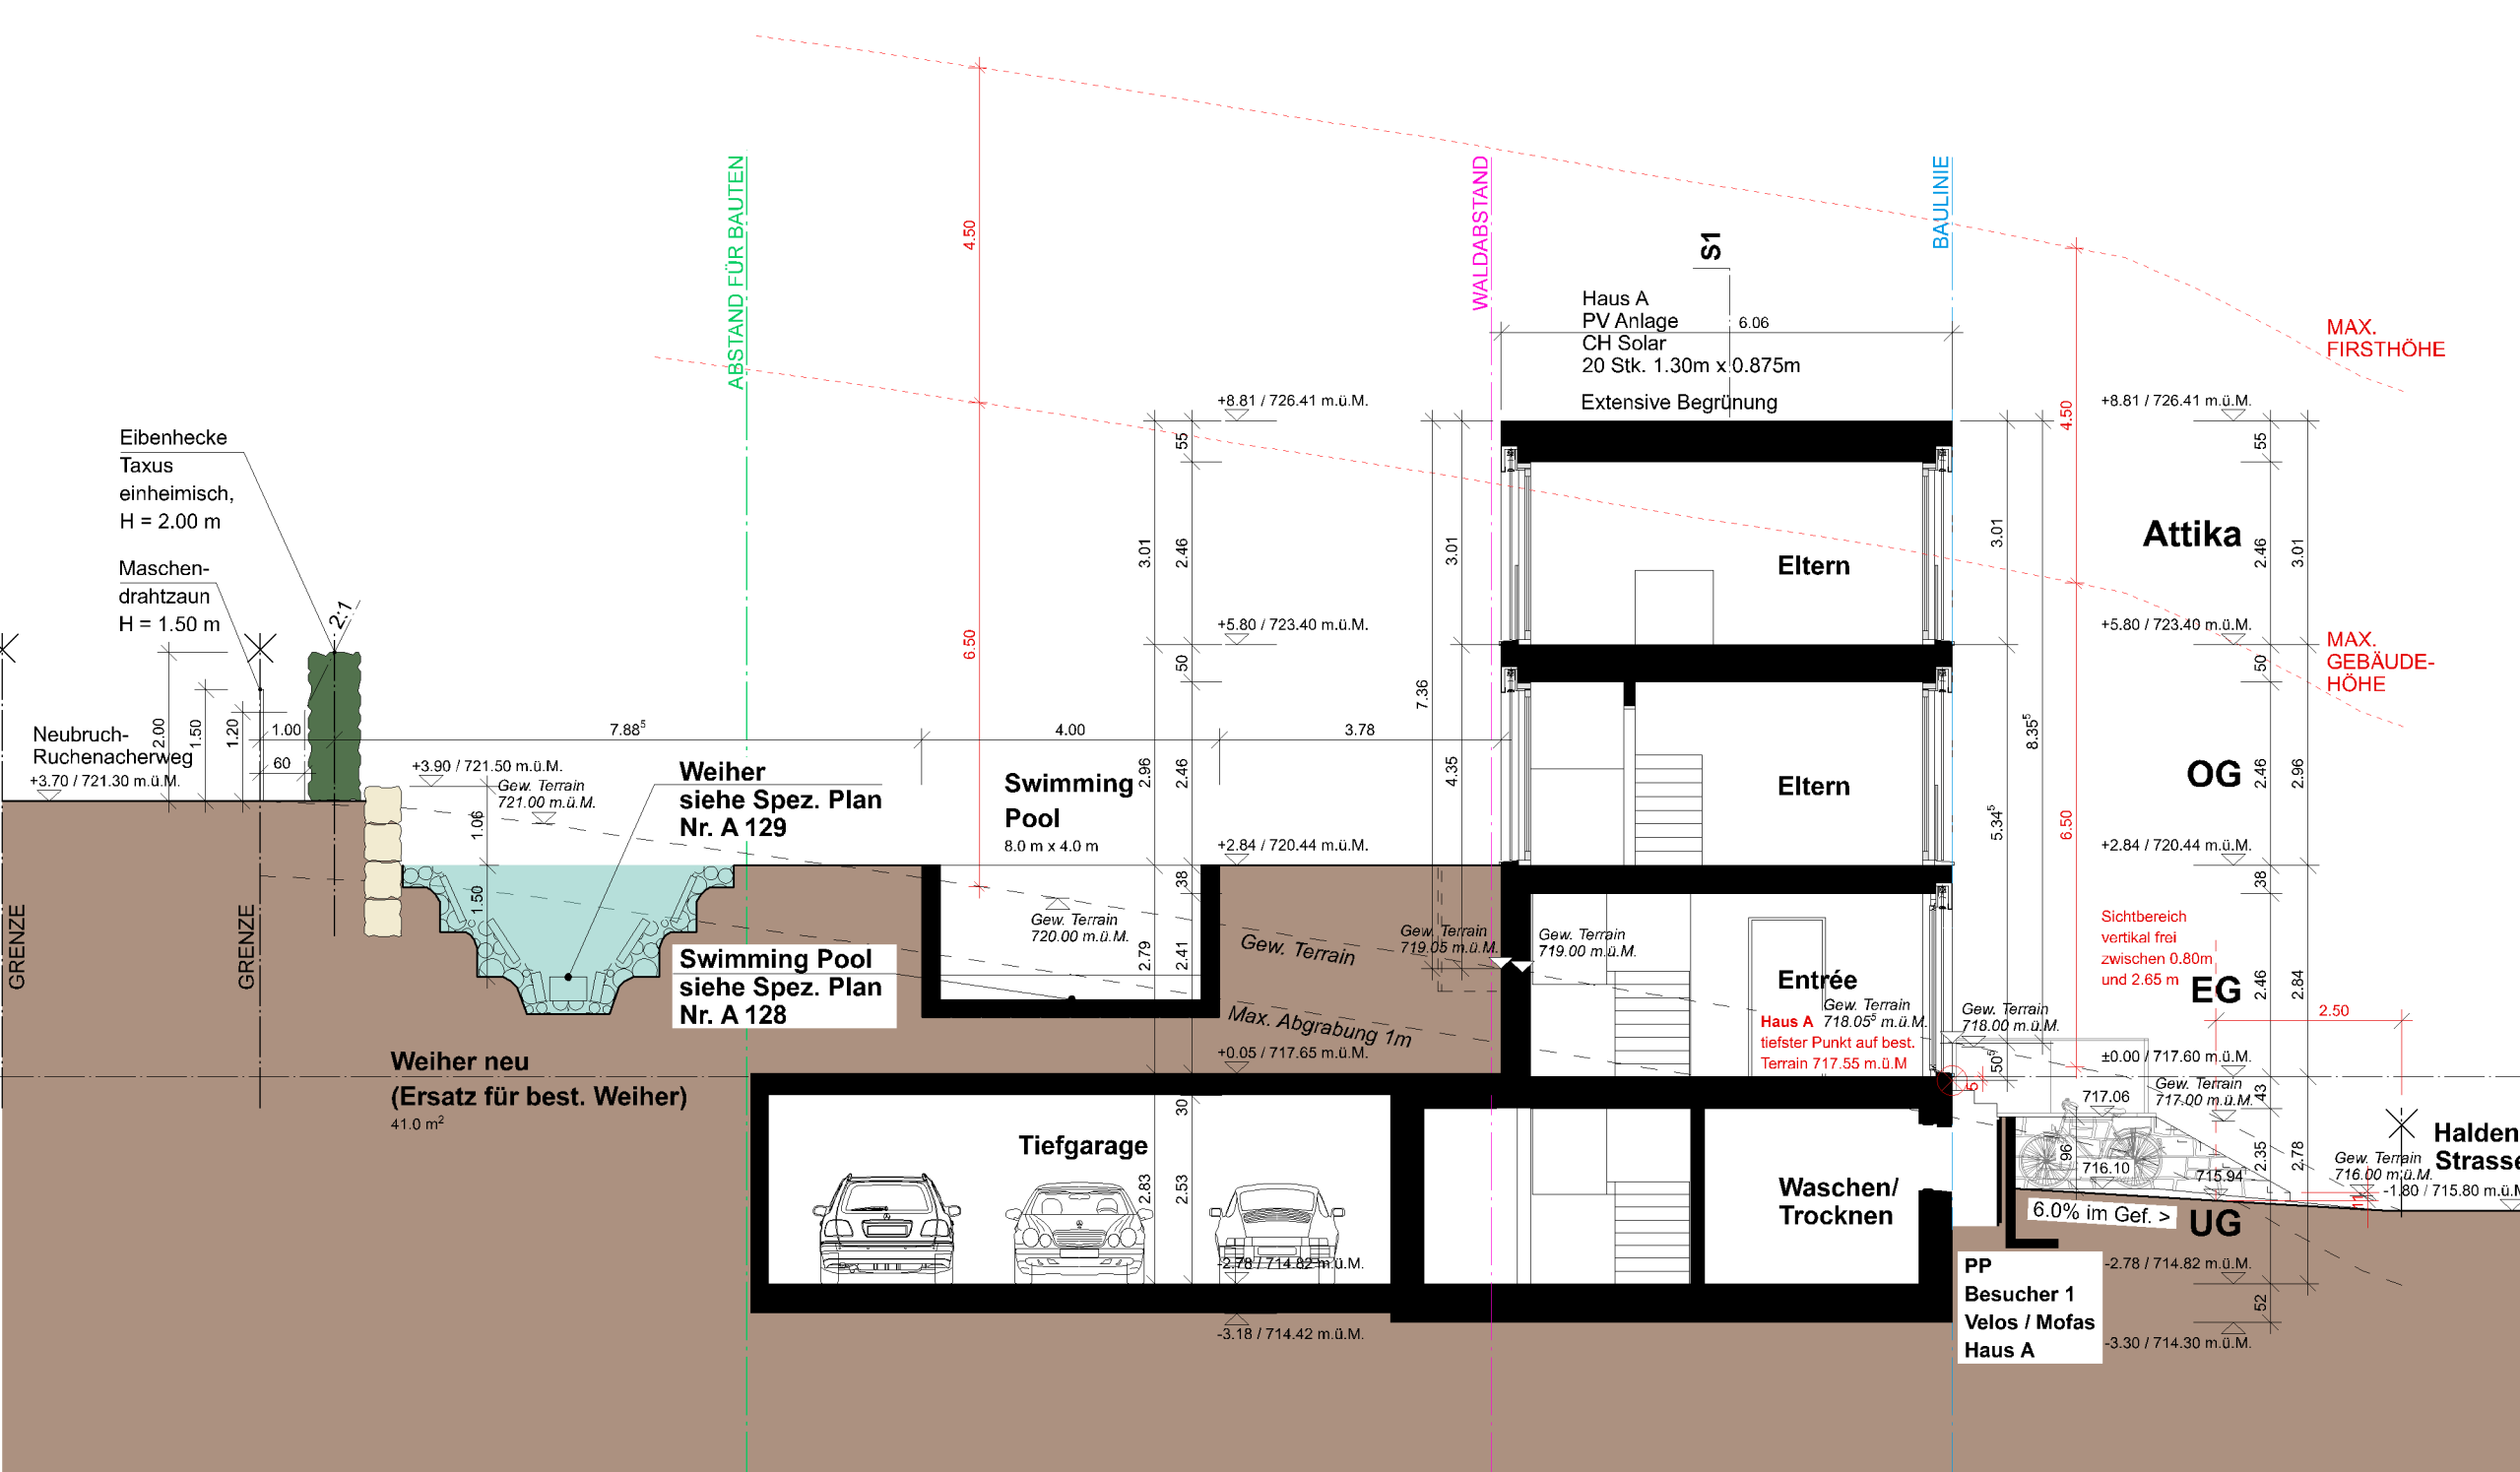

SA1 - Schnitt Haus A

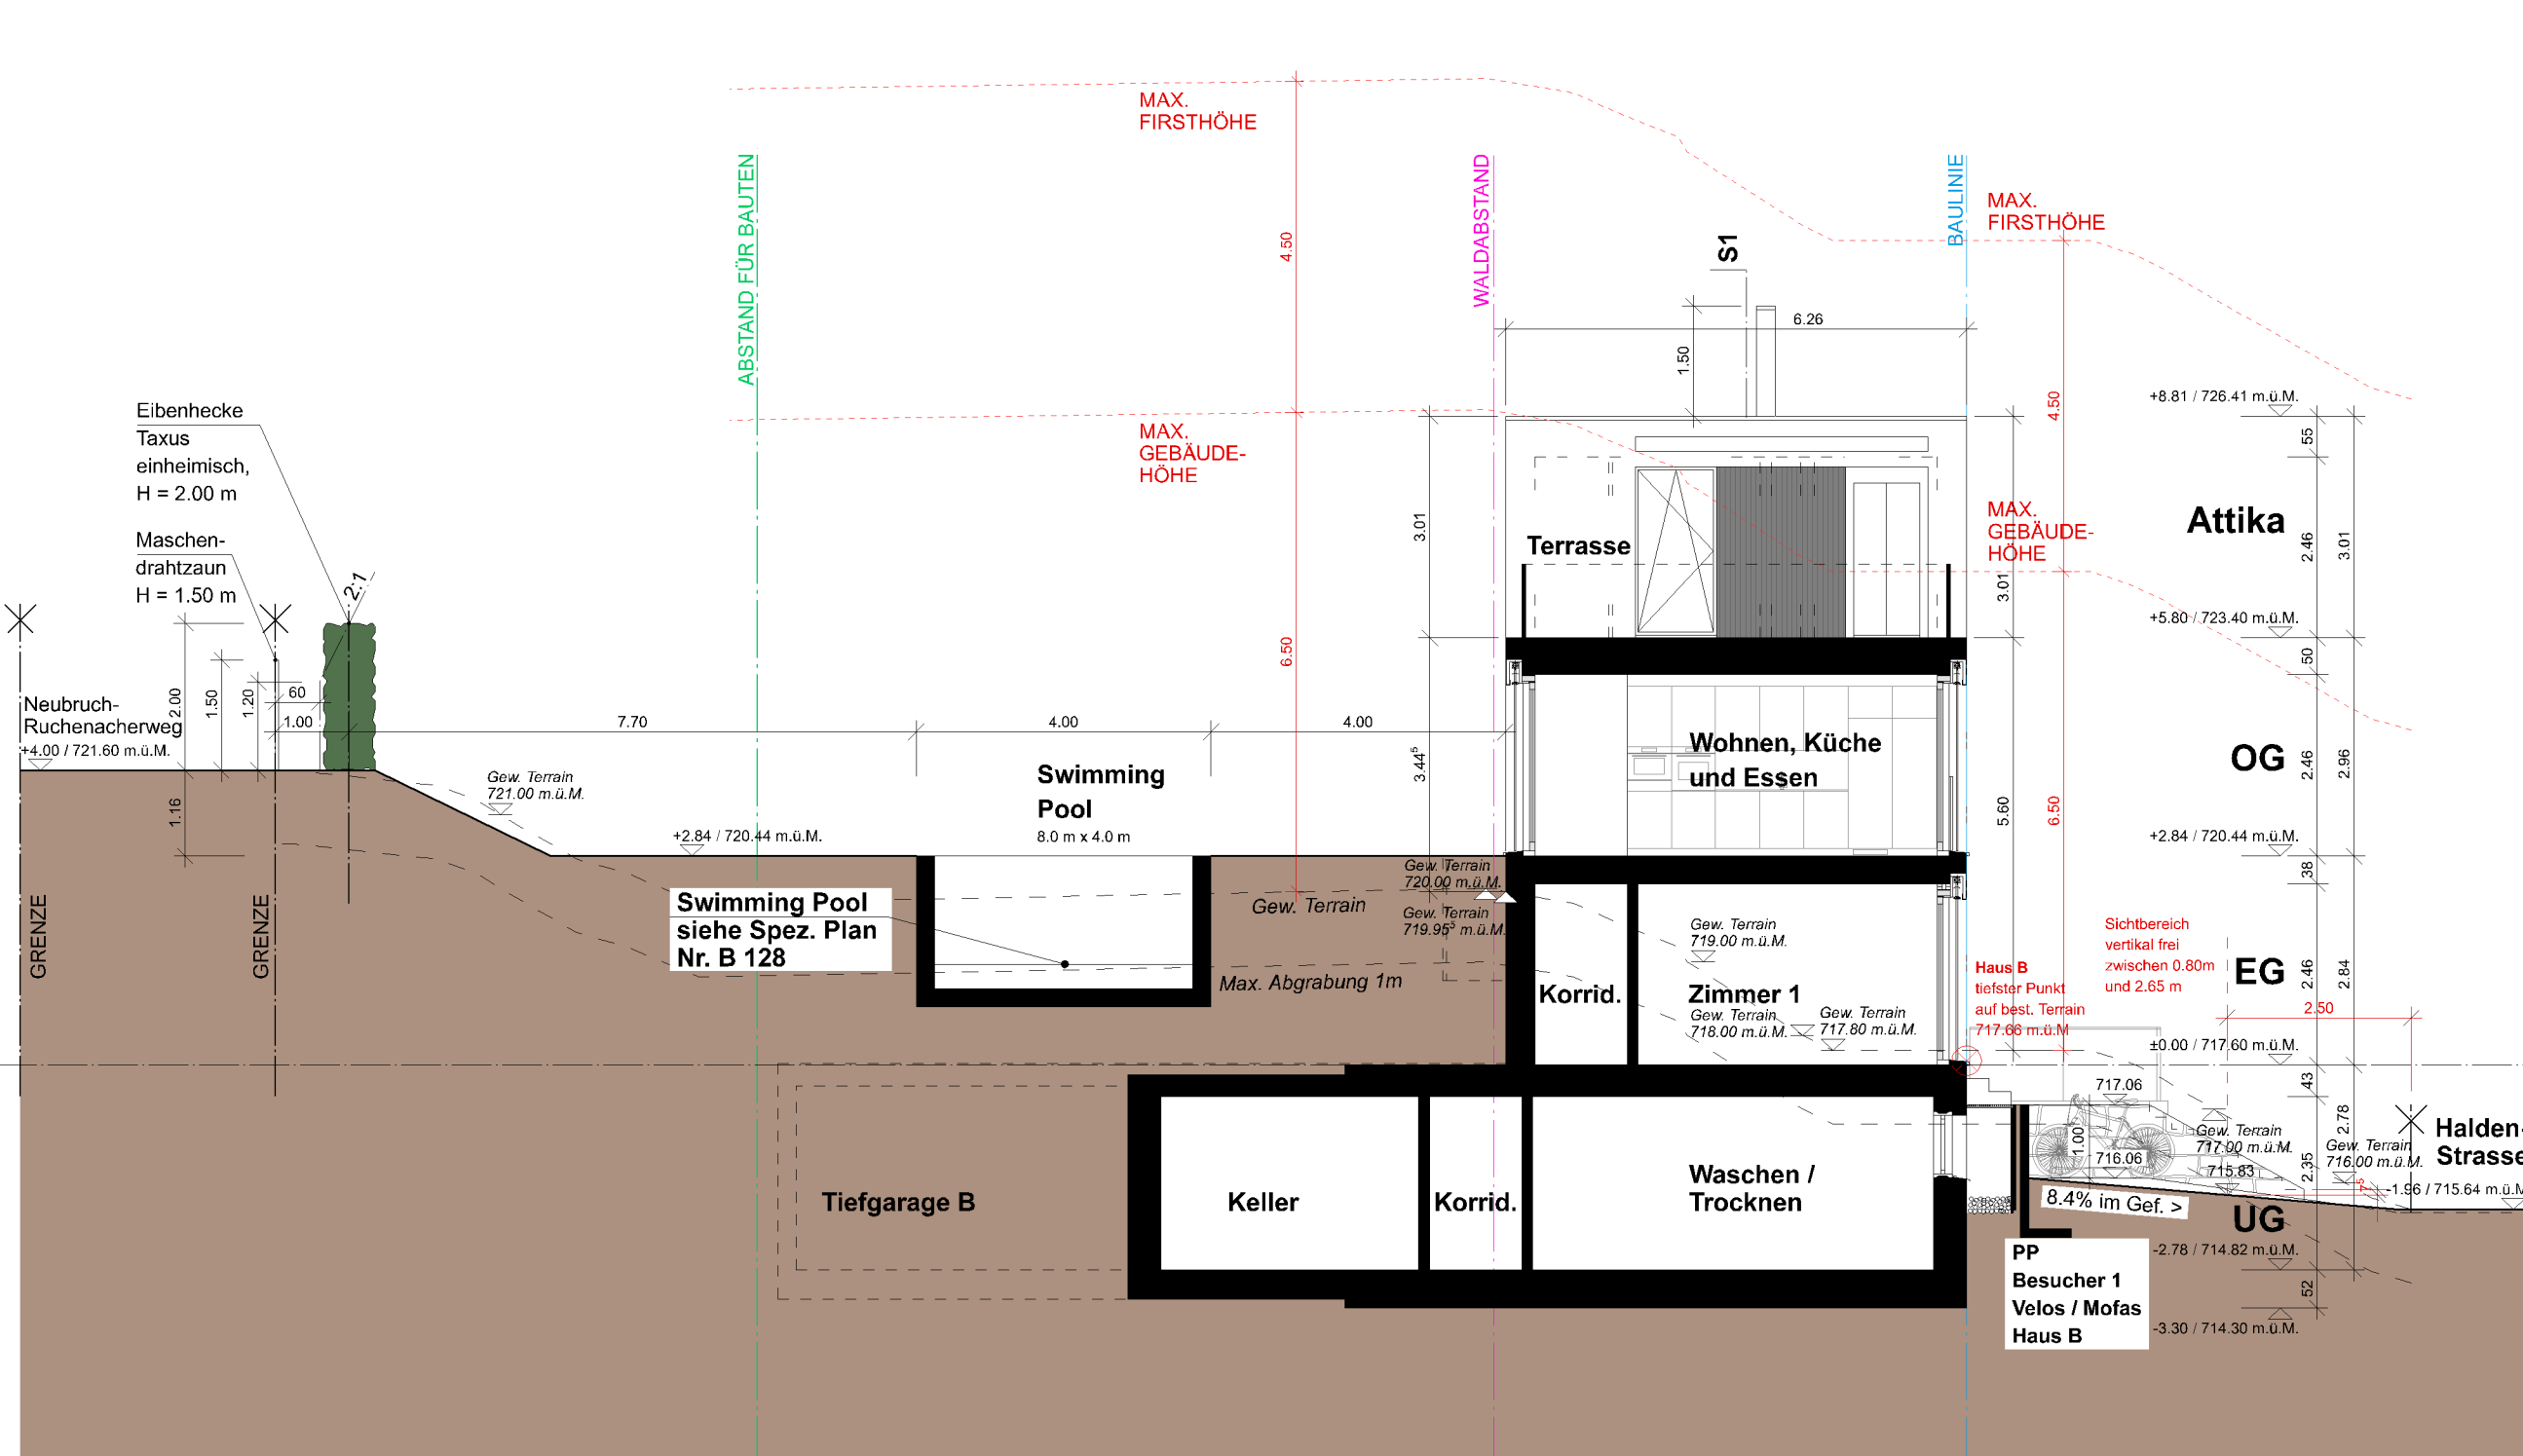

SB1 - Schnitt Haus B

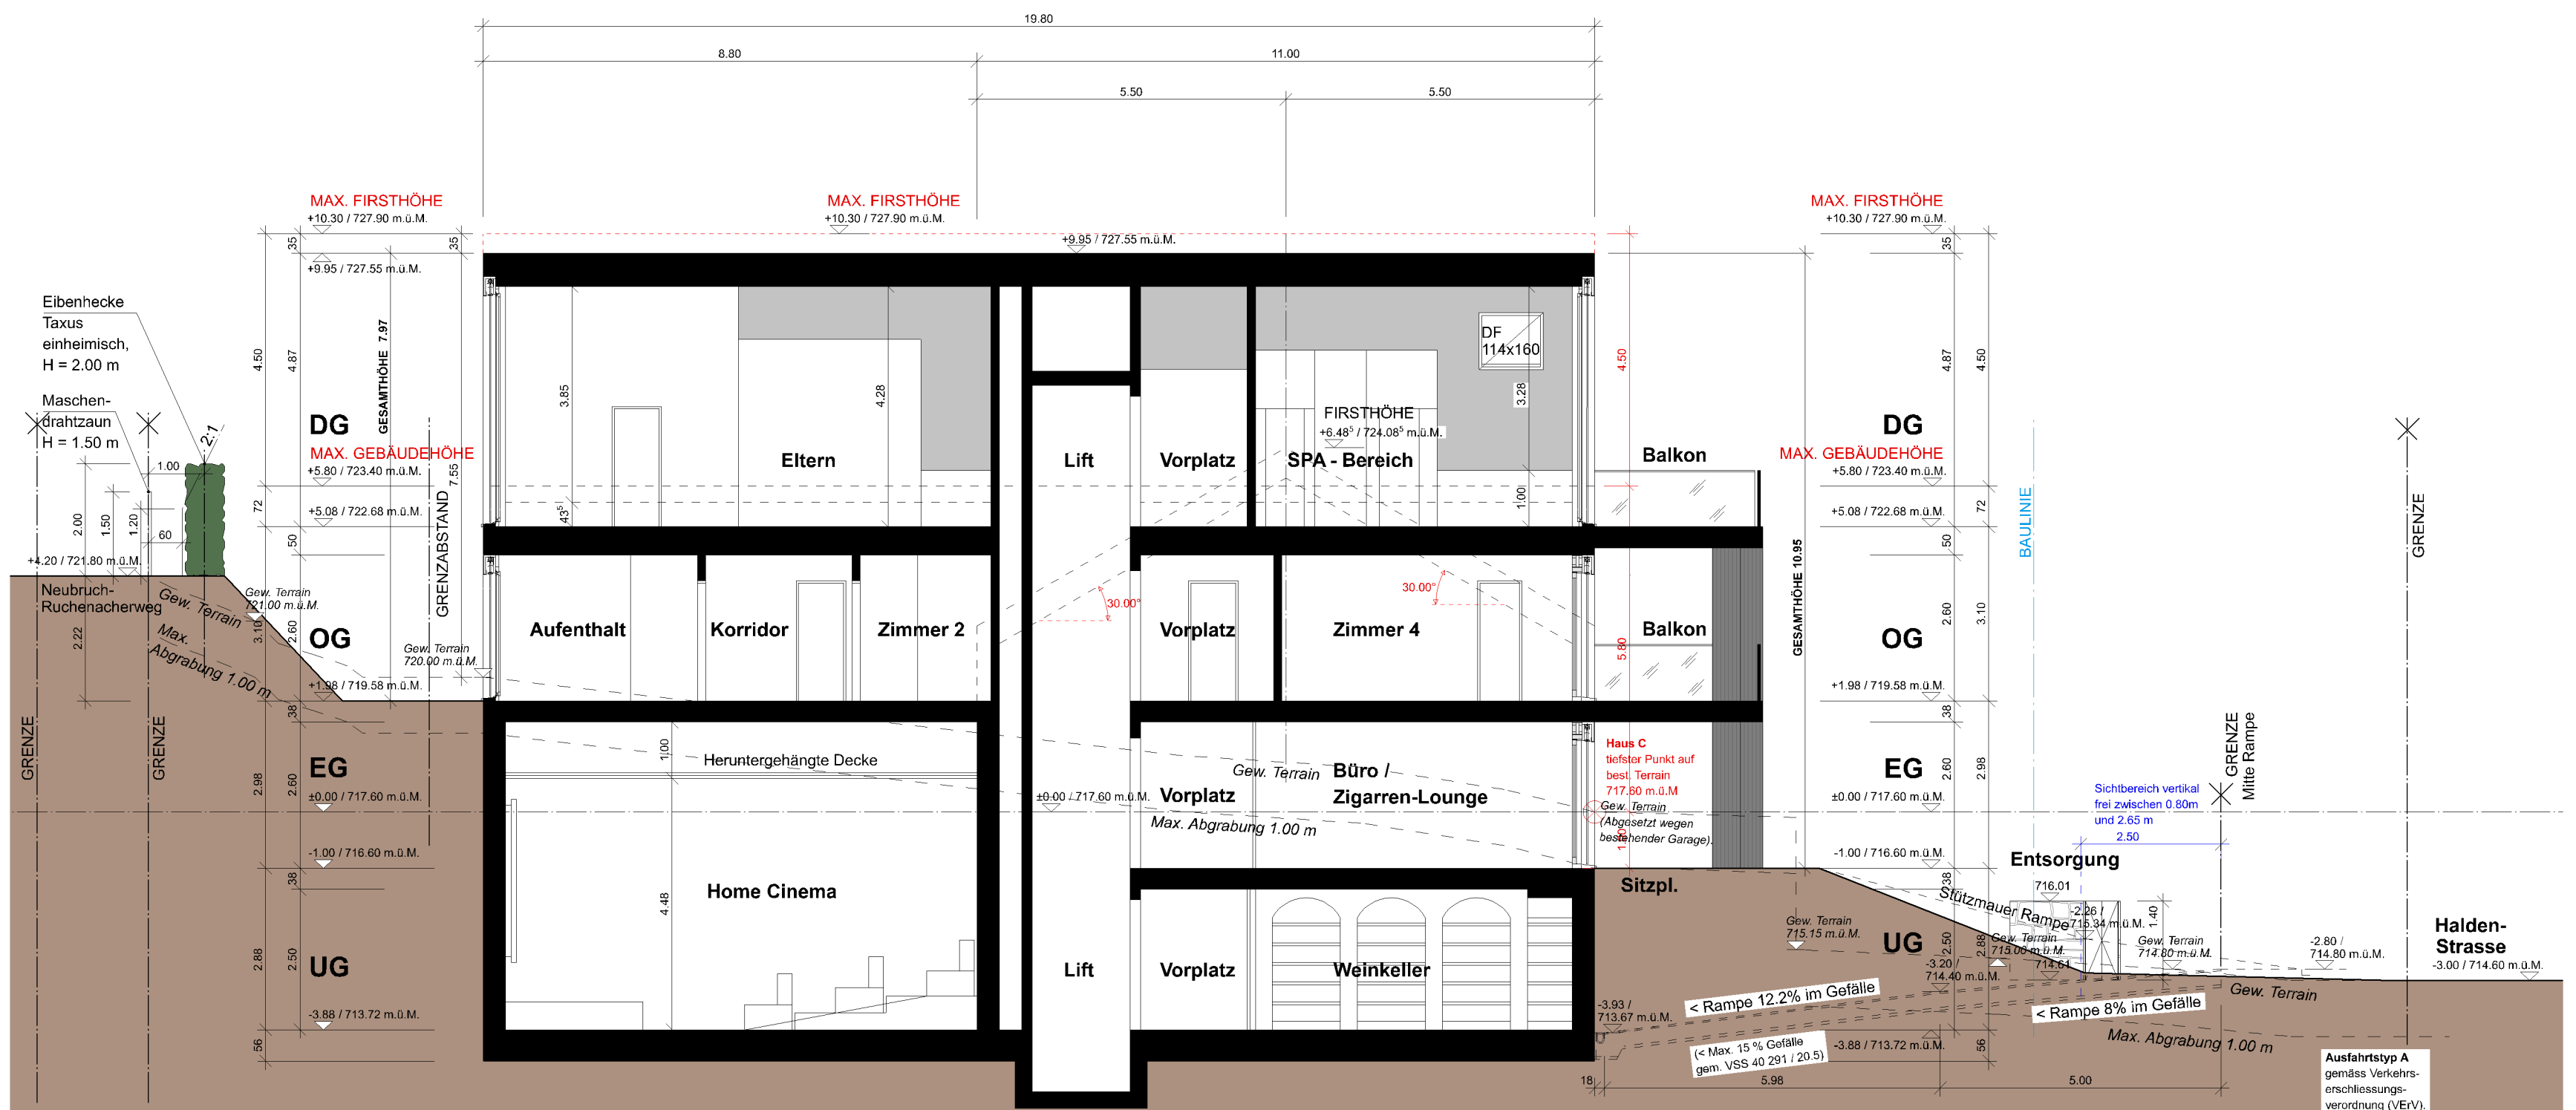

SC2 - Schnitt Haus C

Projektverfasser:

dw design & concept ag
Hofstrasse 106
8620 Wetzikon

Bauherr / Grundeigentümer:

rw immobilien ag
Hofstrasse 106
8620 Wetzikon

Unterschrift Projektverfasser

Unterschrift Bauherr / Grundeigentümer

±0.00 = 717.60 m.ü.M (OK Fertigbelag EG Haus A und B)

Alle Masse sind vom Unternehmer vor der Ausführung am Bau zu nehmen, bzw. zu kontrollieren. Allfällige Differenzen sind unverzüglich mit der Bauleitung zu klären. Falls nicht anders vermerkt sind die Fensterhöhen von OK fertig Boden bis UK Sturz gemessen. Türhöhen sind von OK fertig Boden oder Schwelle bis UK roher Sturz gemessen.

Index	Datum	Geändert von	Änderung
A	13.02.2023	MDS	Auswechslung / Balkonstützen Haus C Format angepasst
B	26.07.2023	MDS	Planauwechslung / Haus B gespiegelt, gekürzt und 3 m zu Haus A verschoben.
C	08.09.2023	MDS	Planauwechslung / Schnitte mit Terrainkoten ergänzt, kontrolliert und kongruent dargestellt.
D	27.02.2024	MDS	Einfahrtsrampe und Parkplätze angepasst, Karminhöhe korrigiert.
E	26.07.2024	MDS	Terrainschnitte ergänzt, Hecke, Pool und Weiher eingezeichnet.

BAUVORHABEN: Überbauung Zumikon

ADRESSE: Haldenstrasse 5, 8126 Zumikon
Parzelle 2999

dw design & concept

ag

BAUFREIGABE

dw design & concept ag
Hofstrasse 106
8620 Wetzikon

Tel: +41 (0)43 477 44 33

info@dw-dc.ch
www.dw-dc.ch

Dieser Plan ist urheberrechtlich geschützt!
Geistiges Eigentum der dw design & concept ag.
Kopieren und weiterverkaufen verboten!

Phase	Plannummer	Planinhalt	Plangröße	Name	Datum	Maßstab
ag	106E	Revidierte Schnitte Haus A, Haus B und Haus C	1370/450	Michael Di Stefano	2022-11-17	1:100
		gezeichnet				
		geprüft				
		freigegeben				