




Südfassade Haus A-B-C

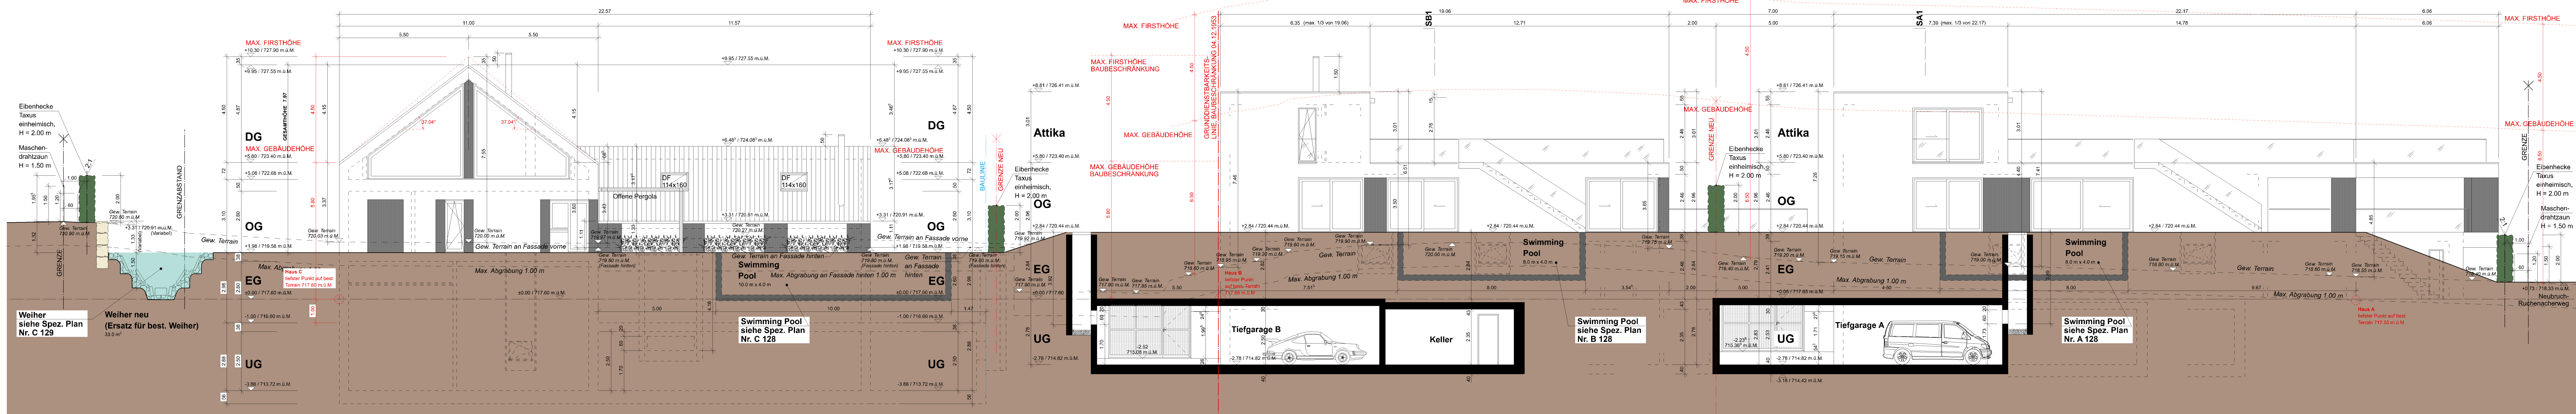


Nordfassade Haus C-B-A

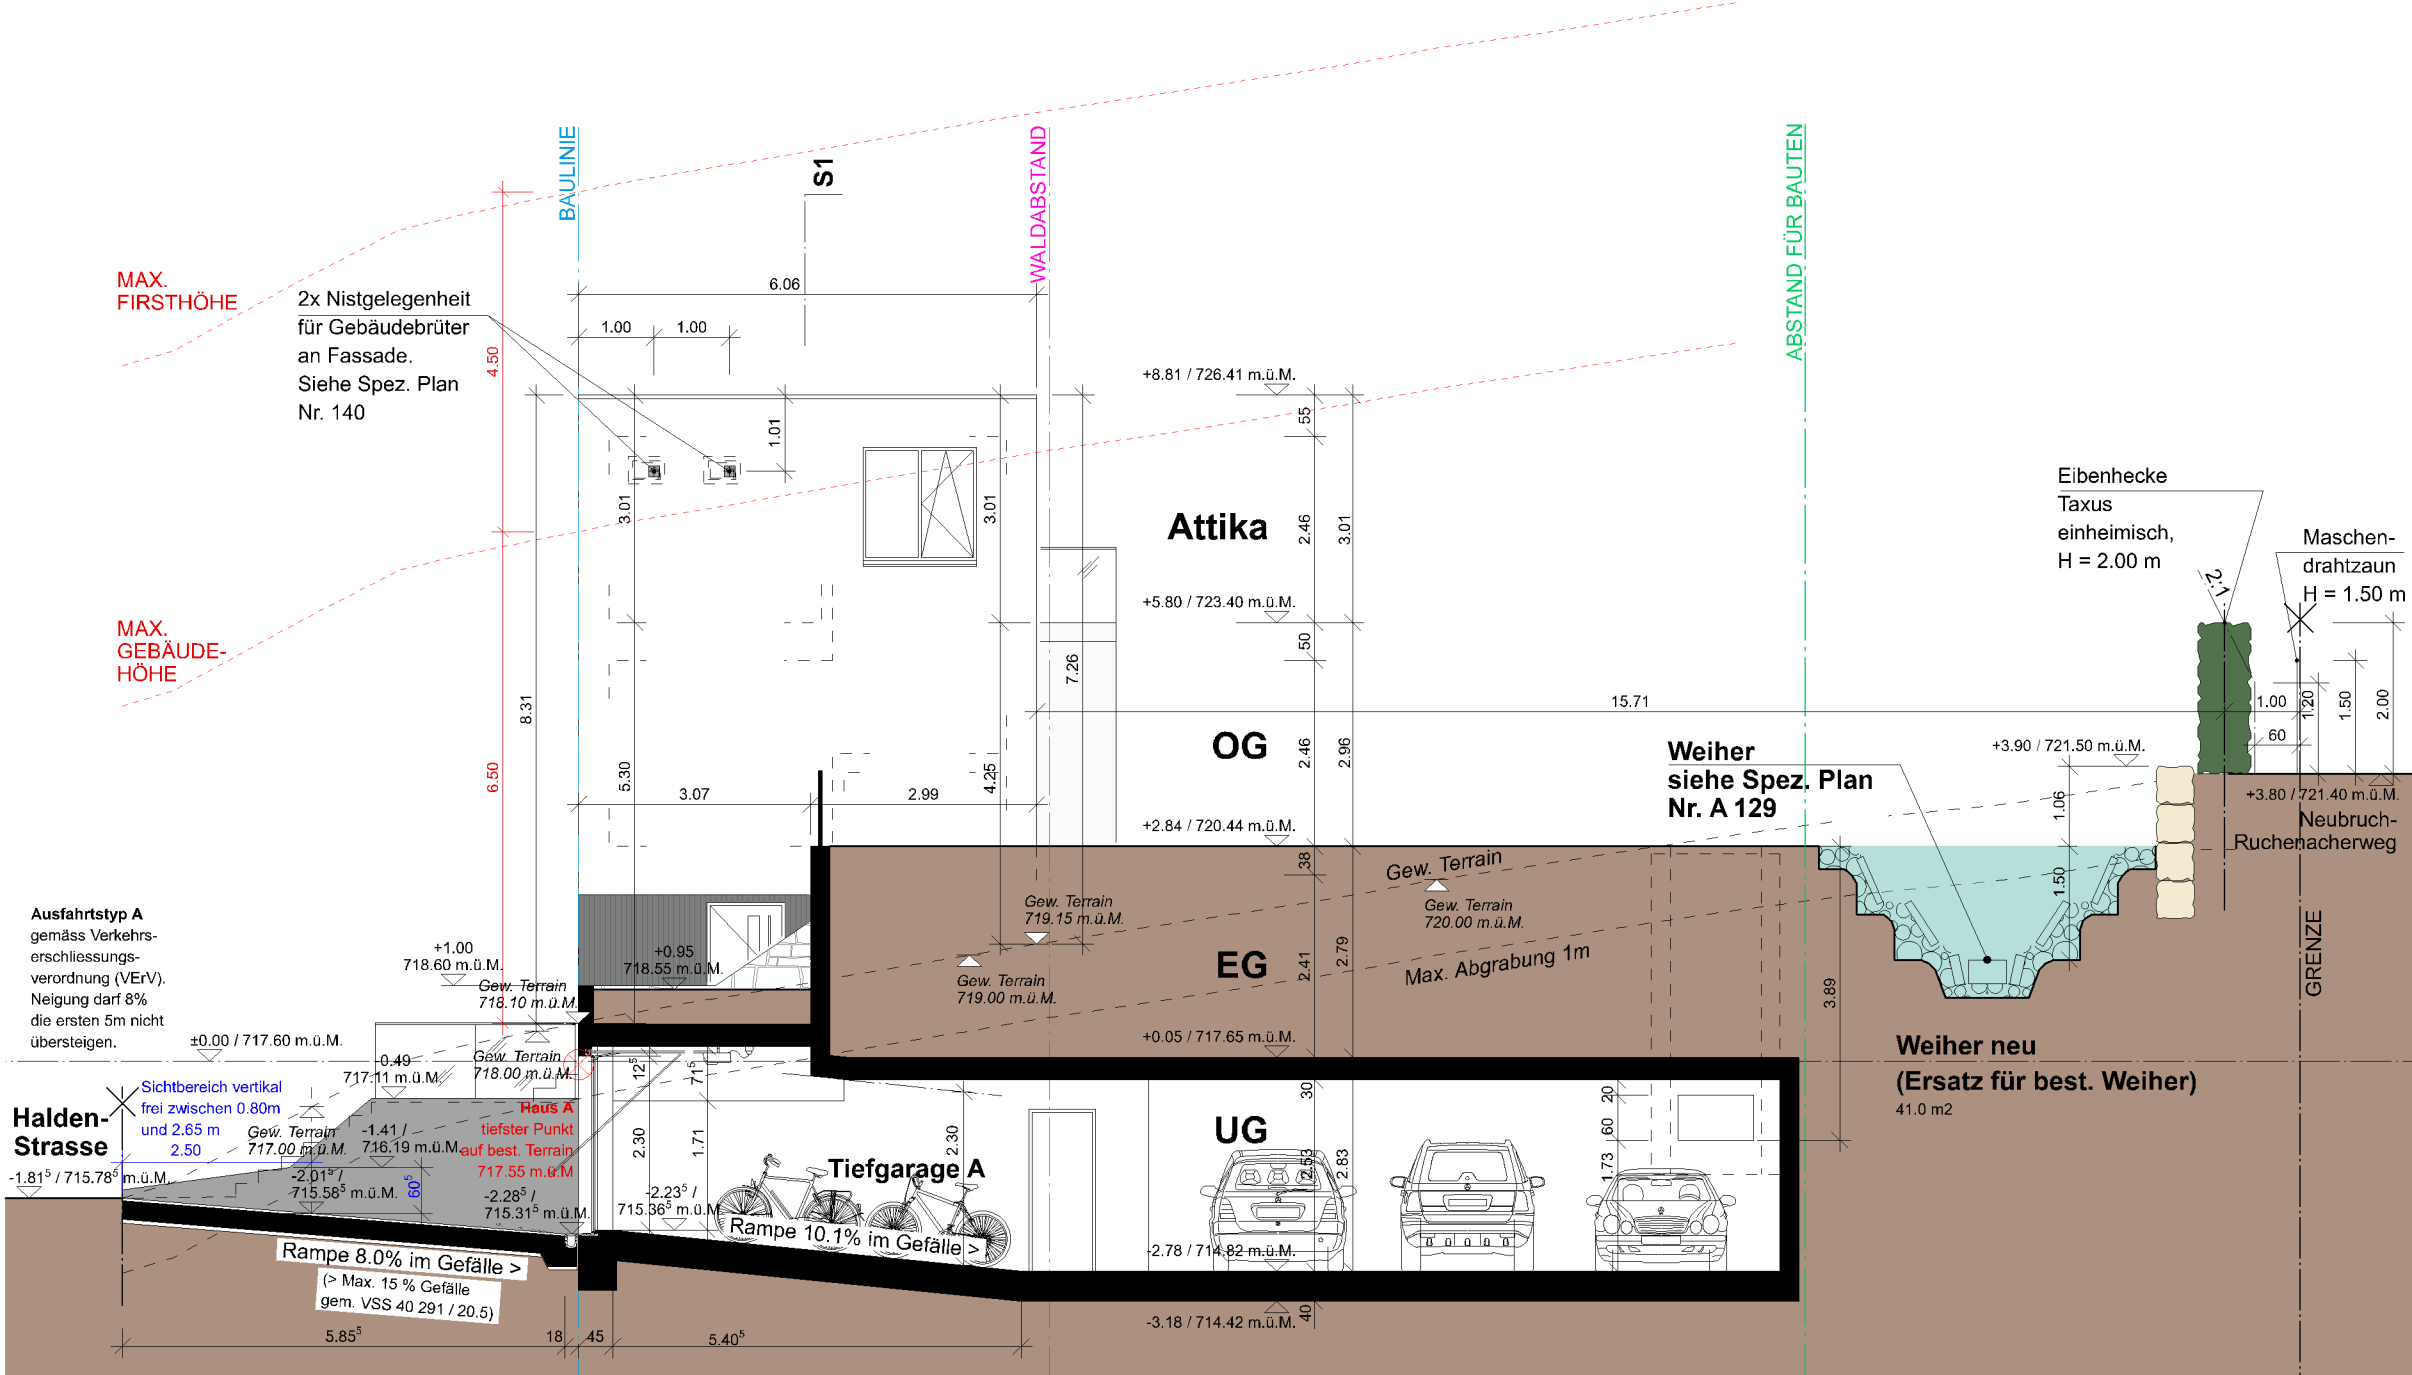


Ostfassade Haus A

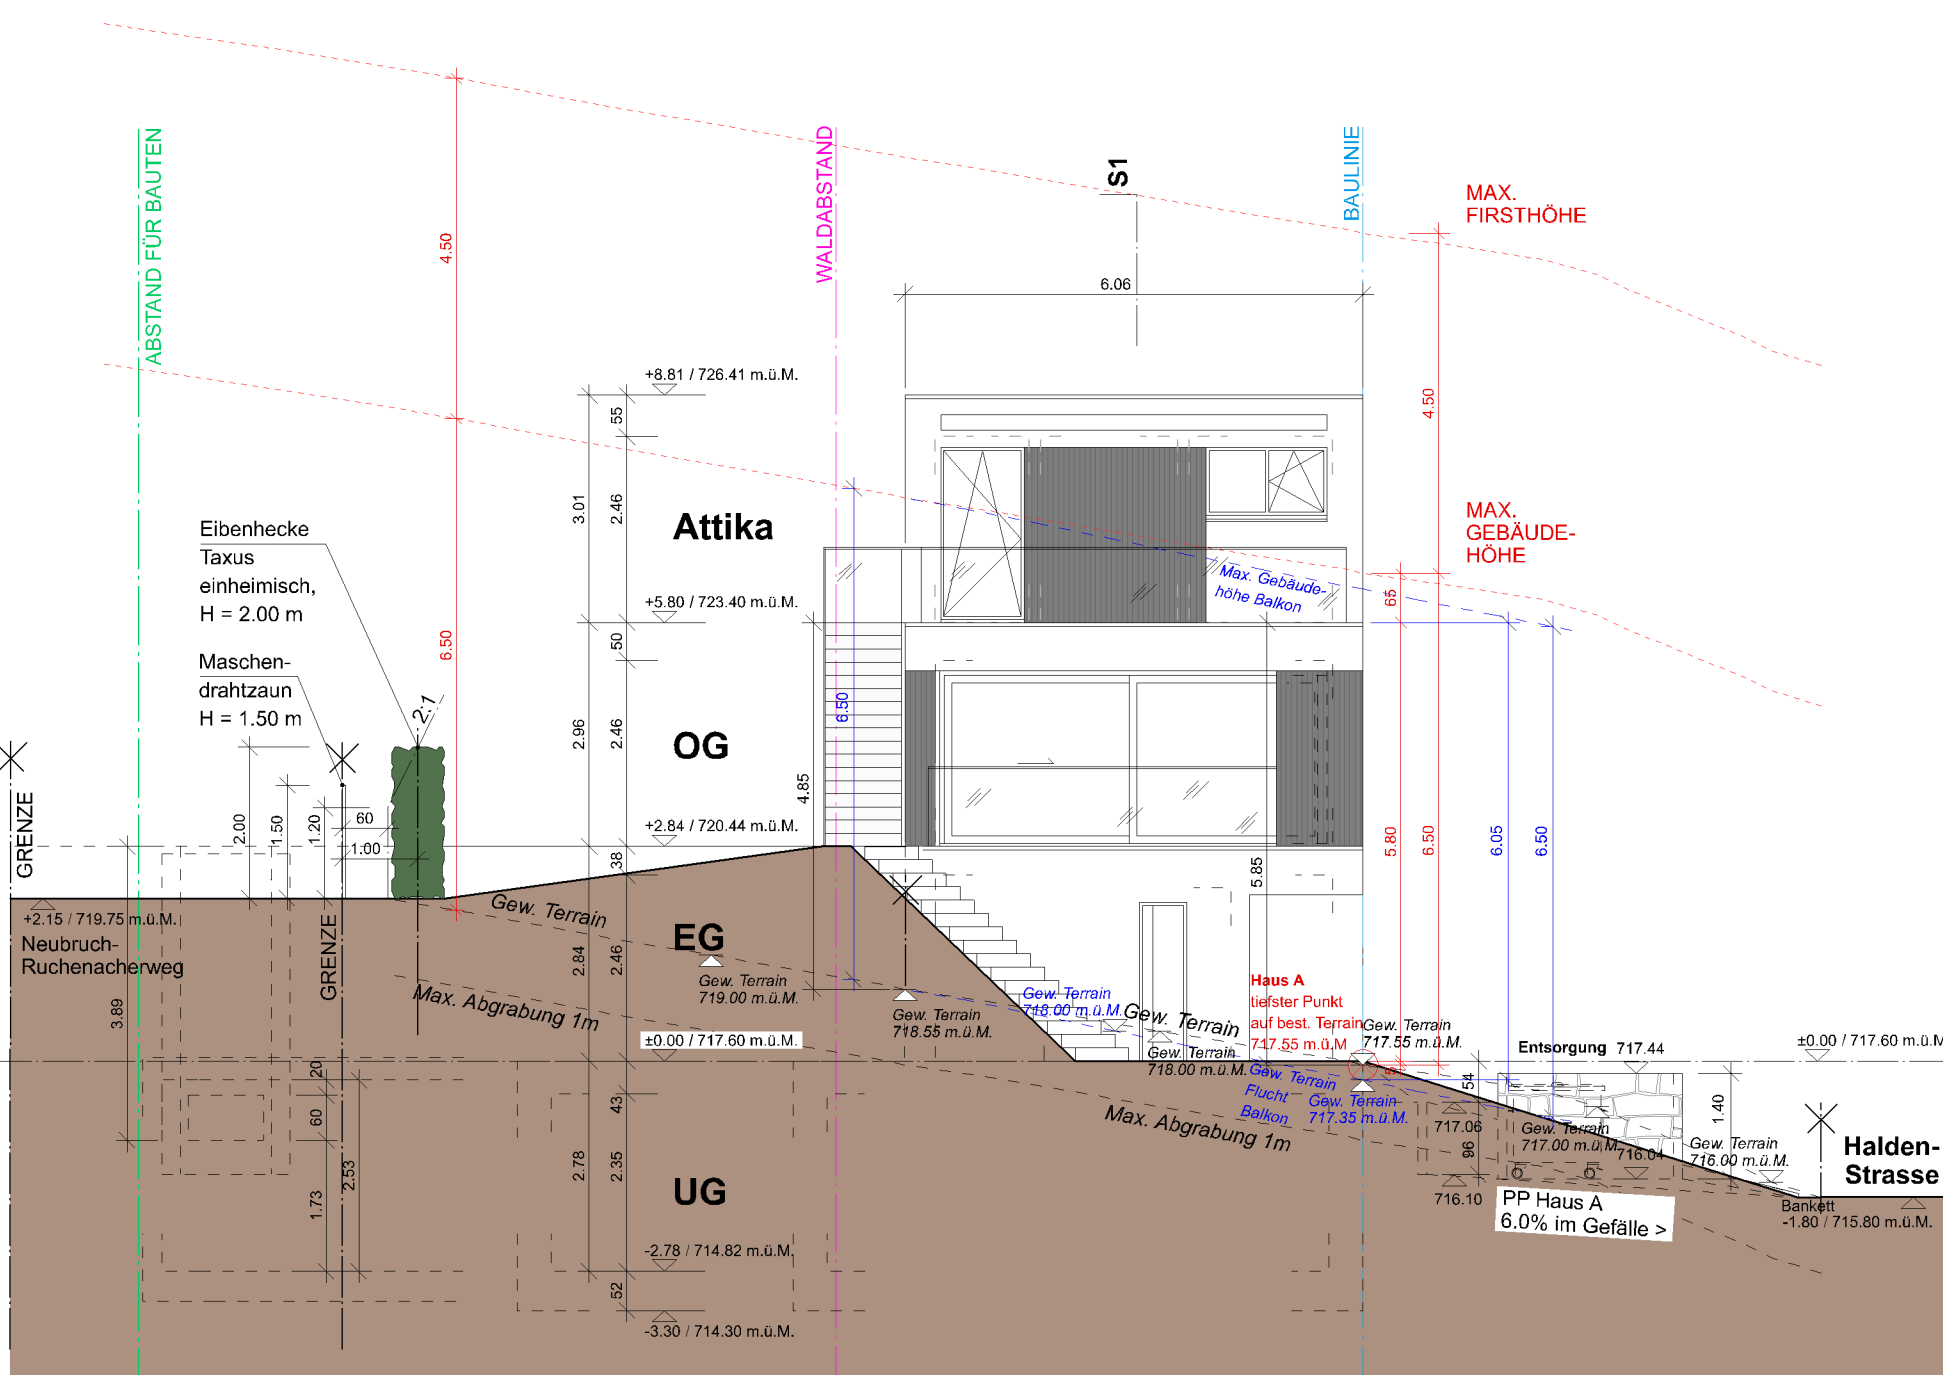


Westfassade Haus A

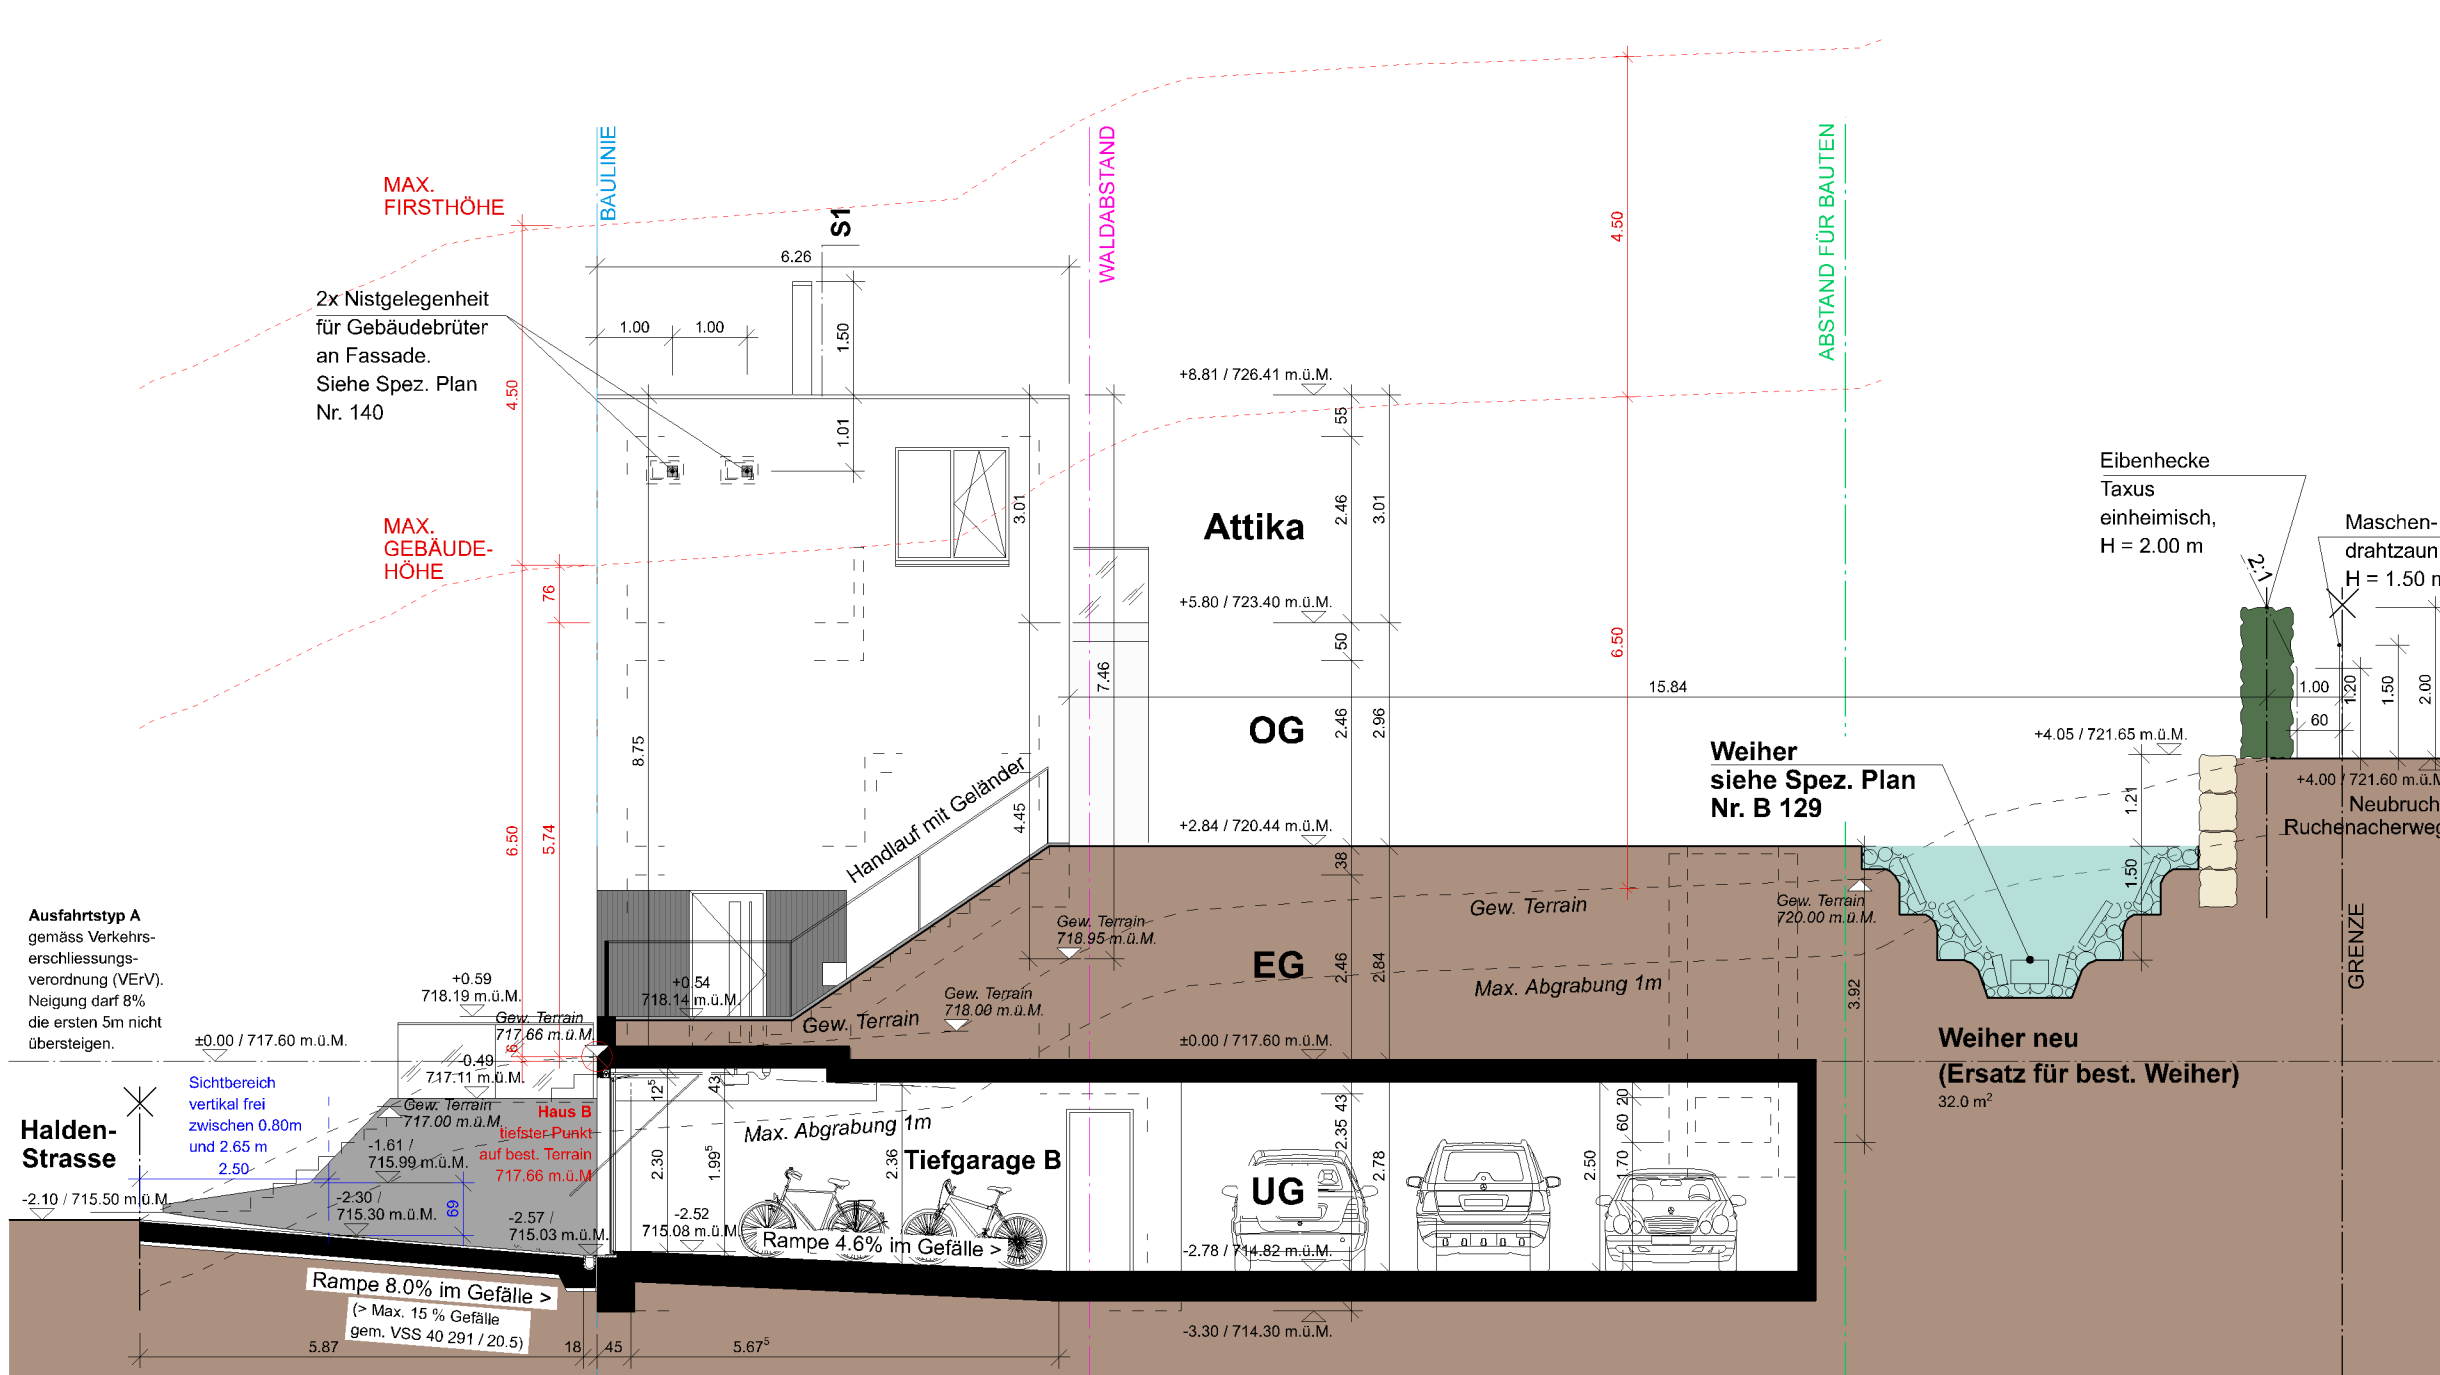


Ostfassade Haus B

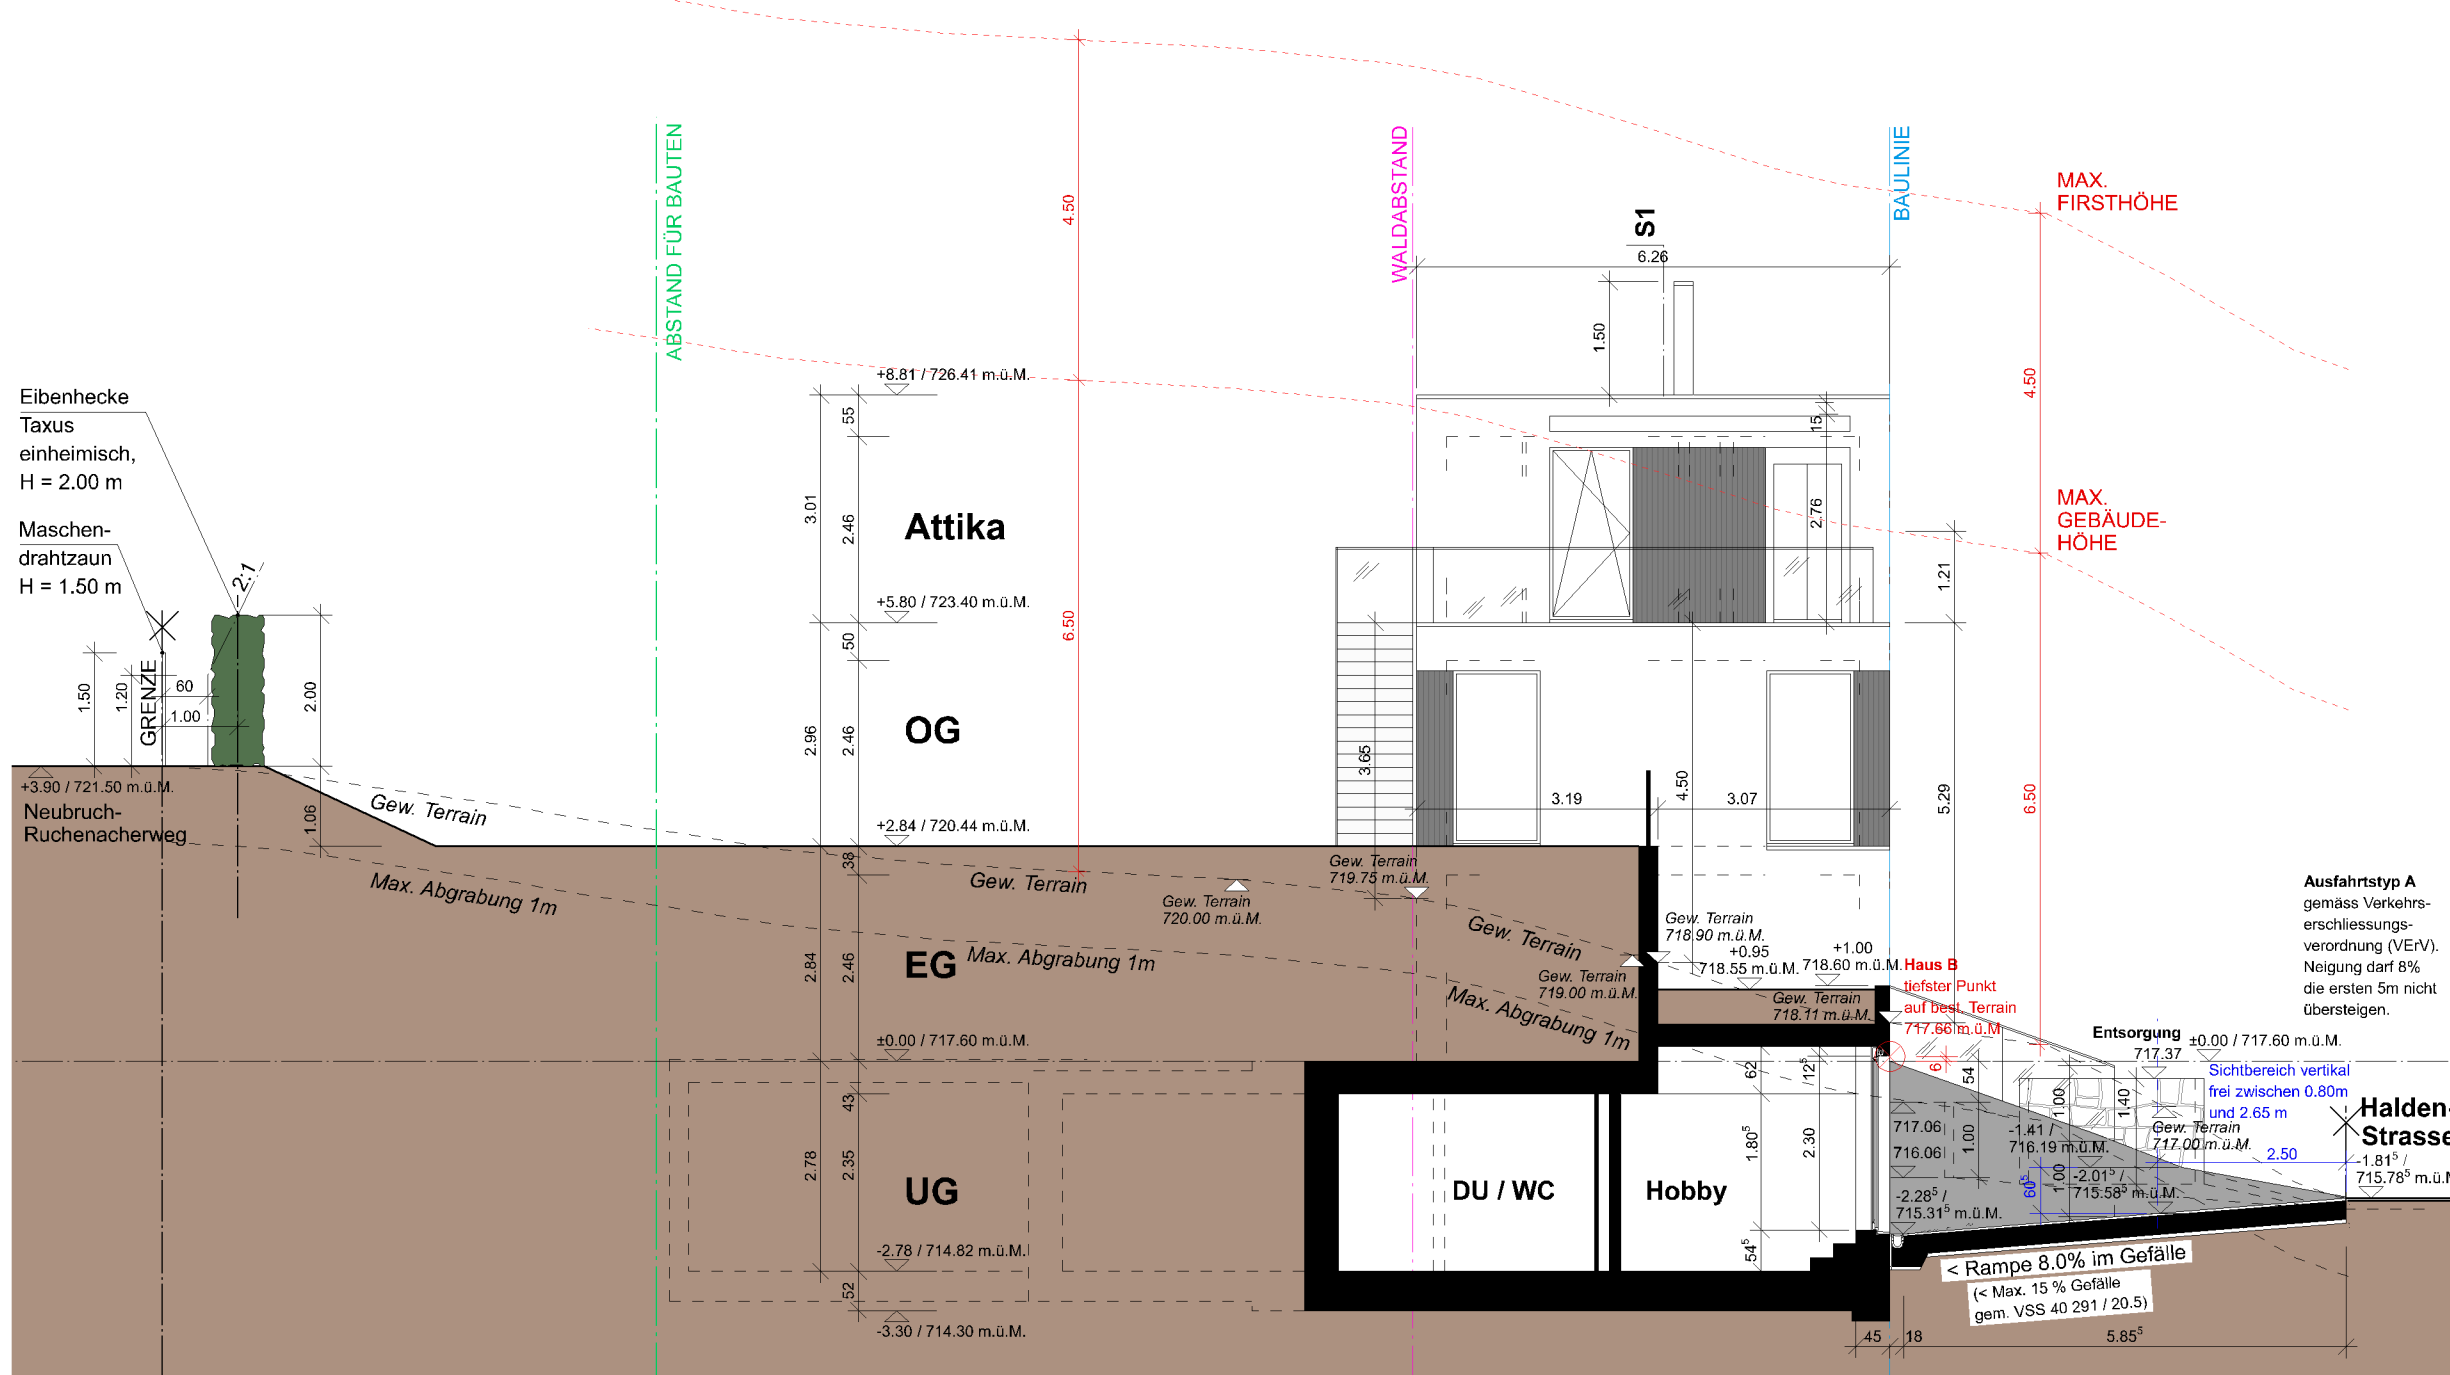

Westfassade Haus B

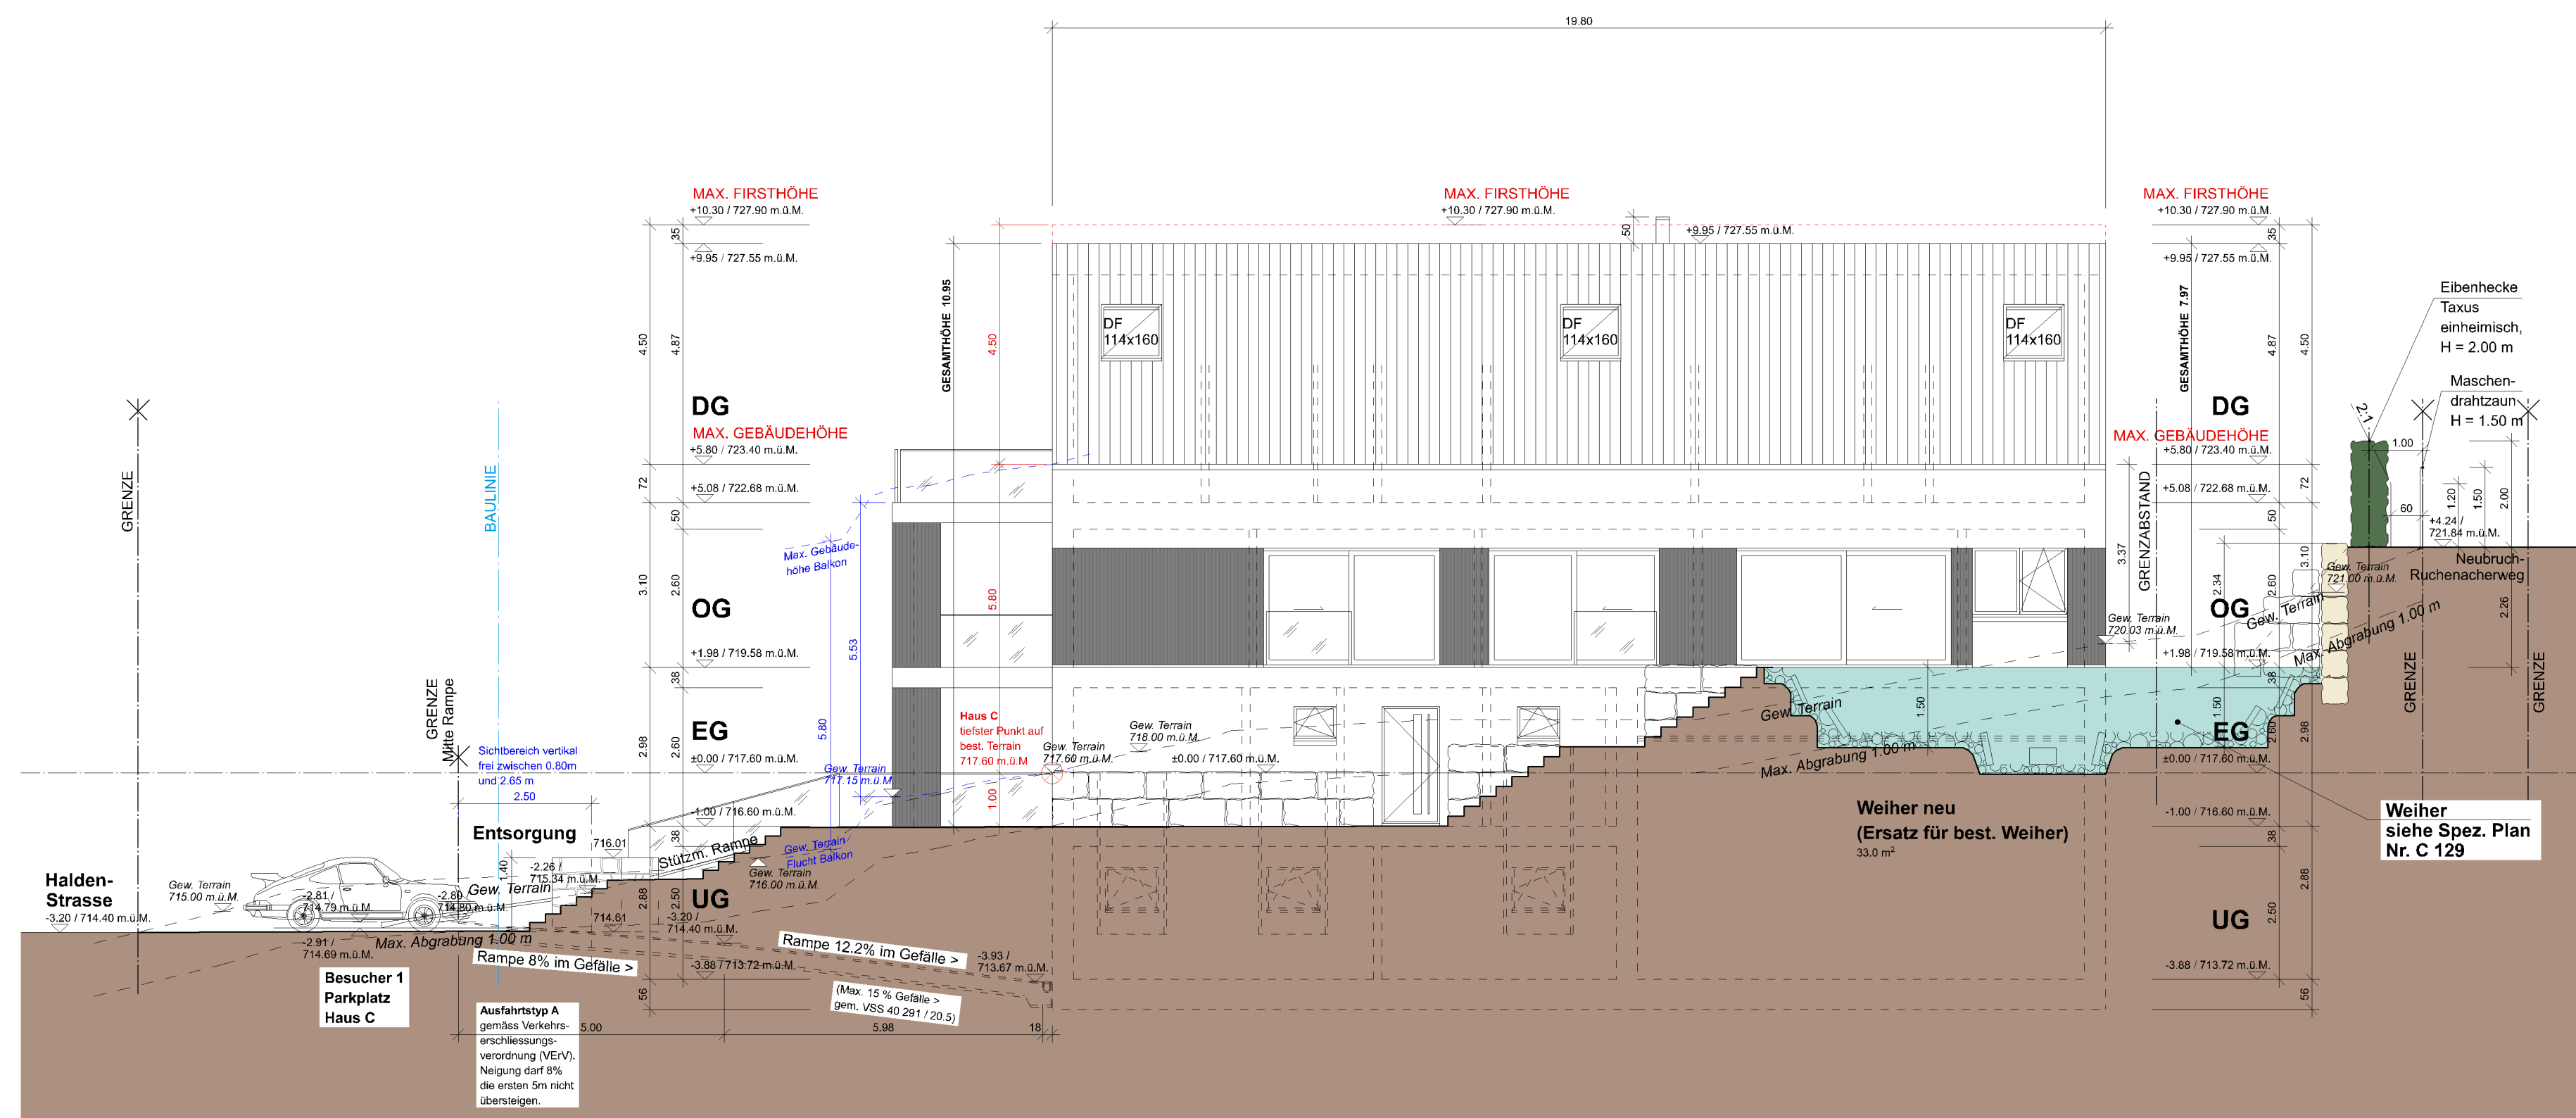

Ostfassade Haus C

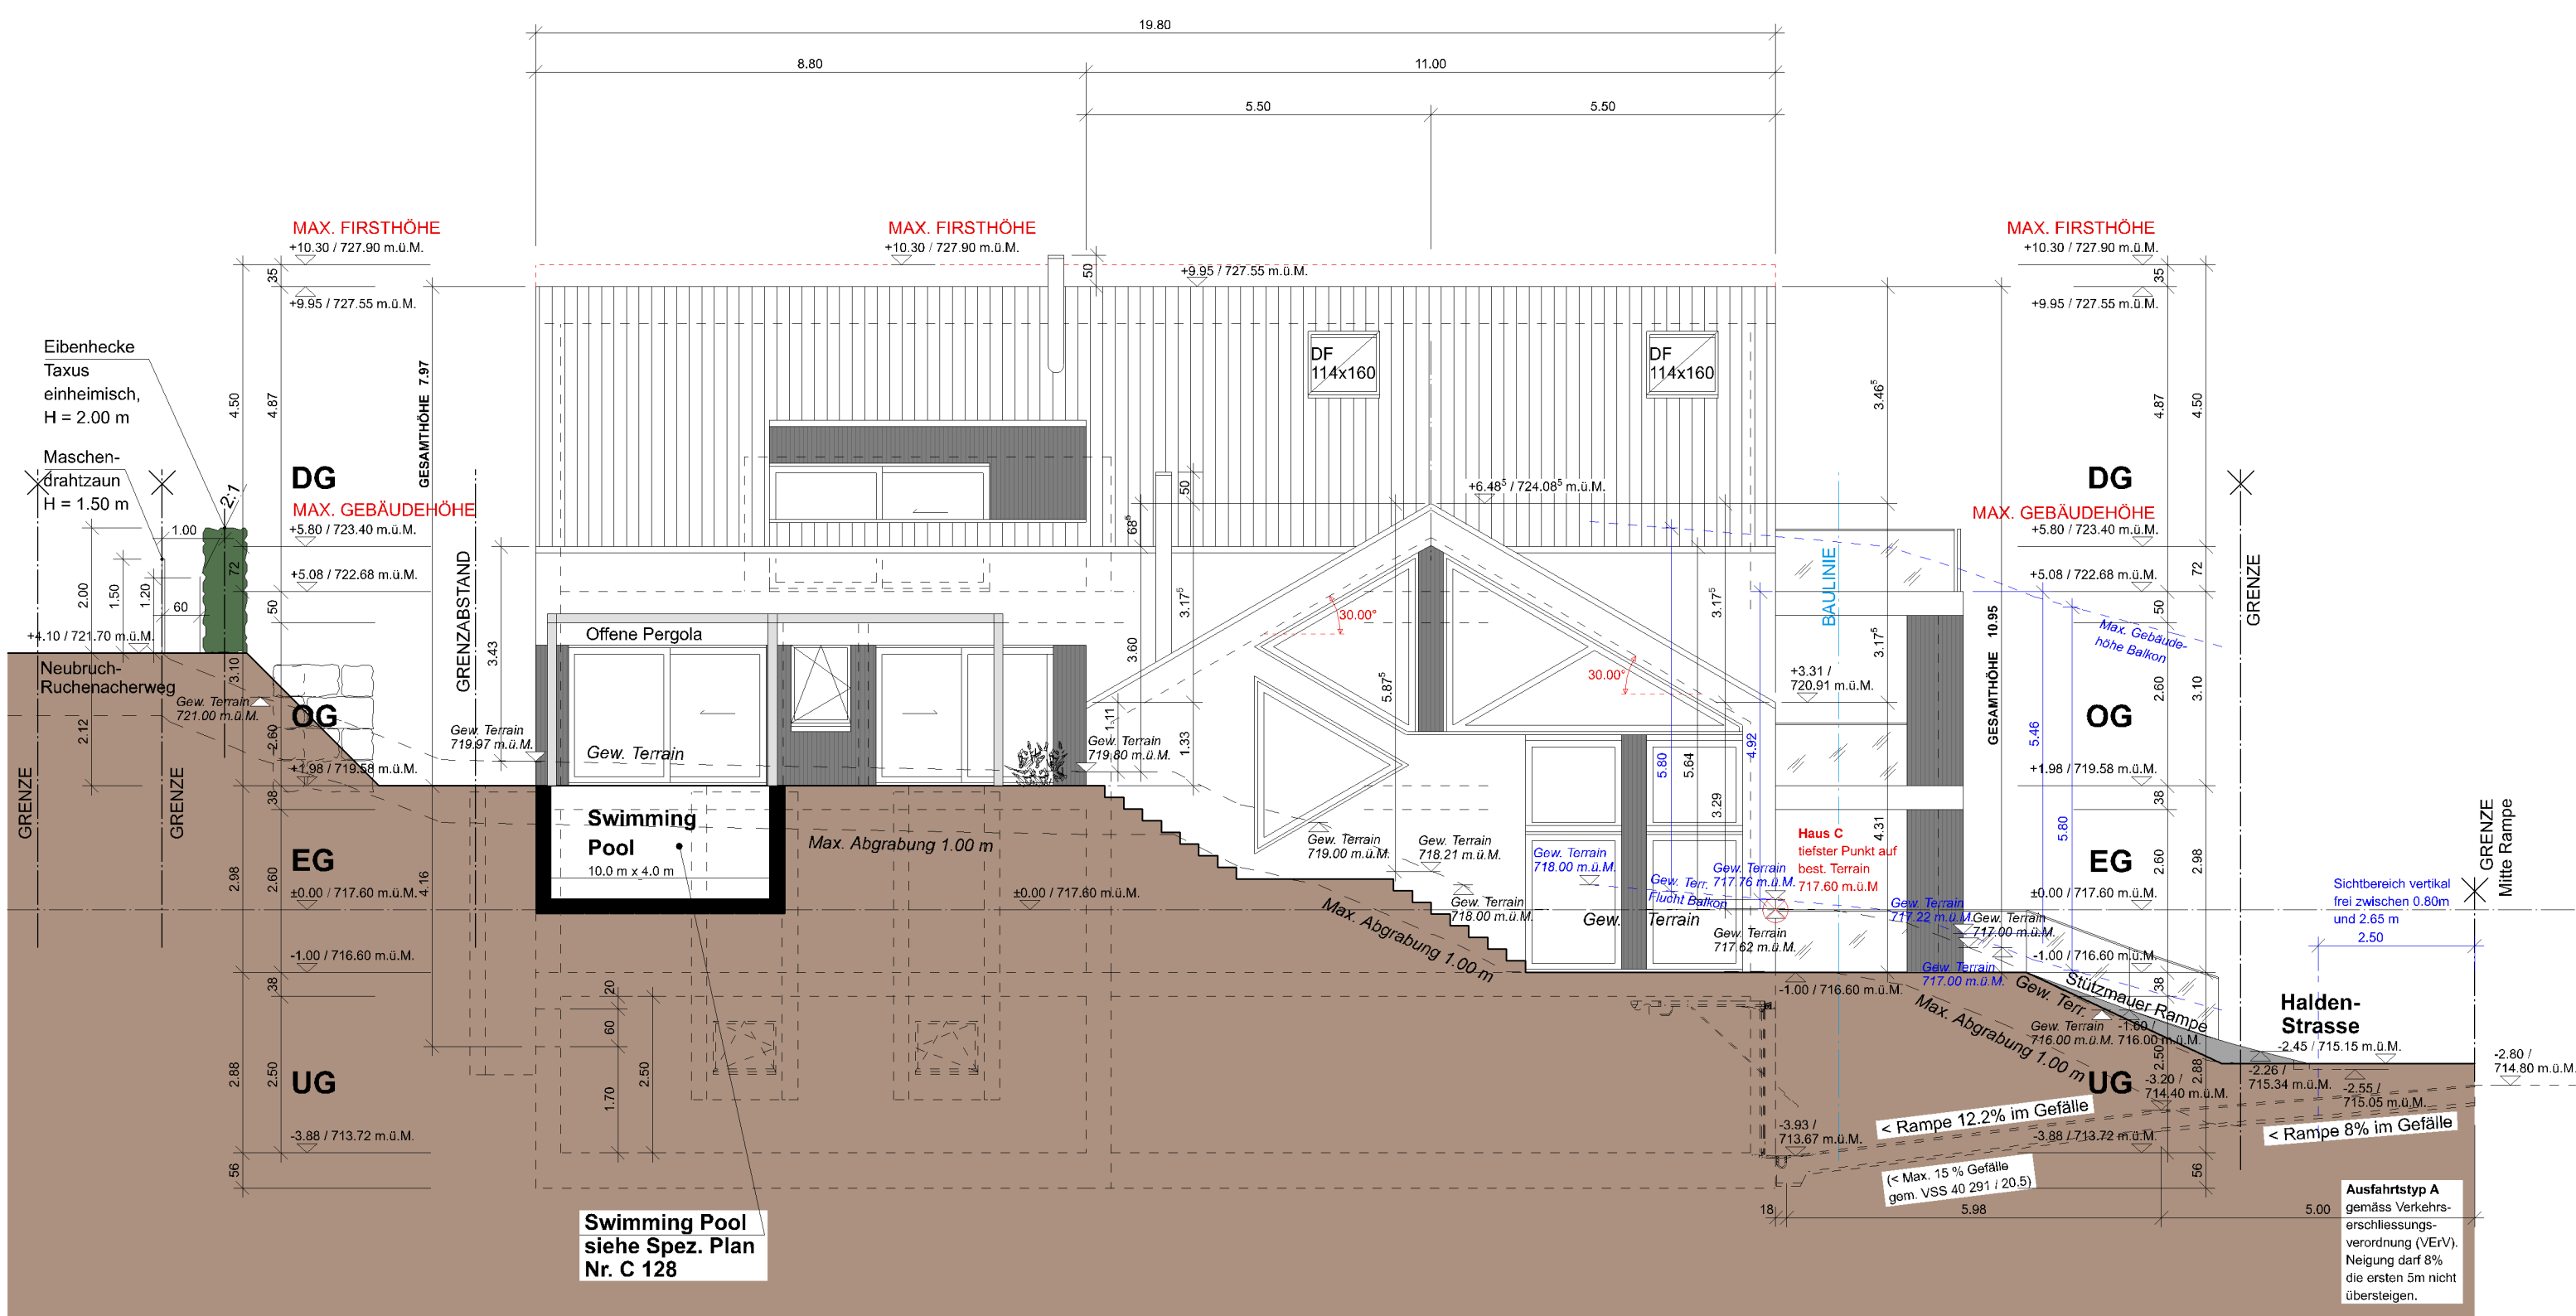

Westfassade Haus C

Projektverfasser: Bauherr / Grundeigentümer:

dw design & concept ag  
Hofstrasse 106  
8620 Wetzikon

die Immobilien ag  
Hofstrasse 106  
8620 Wetzikon

Unterschrift Projektverfasser Unterschrift Bauherr / Grundeigentümer

±0.00 = 717.60 m.ü.M (OK Fertigelag EG Haus A und B)

| Index | Datum      | Geändert von | Änderung                                                                                    |
|-------|------------|--------------|---------------------------------------------------------------------------------------------|
| A     | 13.02.2023 | MDS          | Planumwechselung / Balkonterrassen Haus C Formal angepasst                                  |
| B     | 26.07.2023 | MDS          | Einbauten in OG der Terrasse Haus A angepasst, Terrasse / Balkon Gebäudehöhe eintragen      |
| C     | 08.09.2023 | MDS          | Planumwechselung / Haus B angepasst, gekürzt und 3 m zu Haus A verschoben                   |
| D     | 27.02.2024 | MDS          | Planumwechselung / Fassaden mit Terrakotten ergänzt, kontrolliert und kongruent dargestellt |
| E     | 12.11.2024 | MDS          | Einbauten und Funktionen angepasst, Kornstrukturen korrigiert                               |
| F     | 26.07.2024 | MDS          | Terrakotten ergänzt, Hecke, Pool und Weiler angepasst                                       |
| F     | 26.07.2024 | MDS          | Nützigenheiten Gebäudehöhen in Ostfassaden Haus A-B ergänzt                                 |

BAUVORHABEN: Überbauung Zumikon

ADRESSE: Haldenstrasse 5, 8126 Zumikon  
Parzelle 2999

| dw design & concept |                    | BAUFREIGABE |                                               |
|---------------------|--------------------|-------------|-----------------------------------------------|
| Phase               | 107F               | Plannummer  | Revidierte Fassaden Haus A, Haus B und Haus C |
| Planmutter          |                    | Planmutter  |                                               |
| Plangröße           | 1300x900           | Name        | Datum                                         |
| gezeichnet          | Michael G. Bredius | Datum       | 2023-11-17                                    |
| geprüft             |                    | geprüft     |                                               |
| freigegeben         |                    | freigegeben |                                               |

Dieser Plan ist urheberrechtlich geschützt  
Geistiges Eigentum der dw design & concept ag  
Kopieren und weiterverbreiten verboten