




Südseite Haus A-B-C

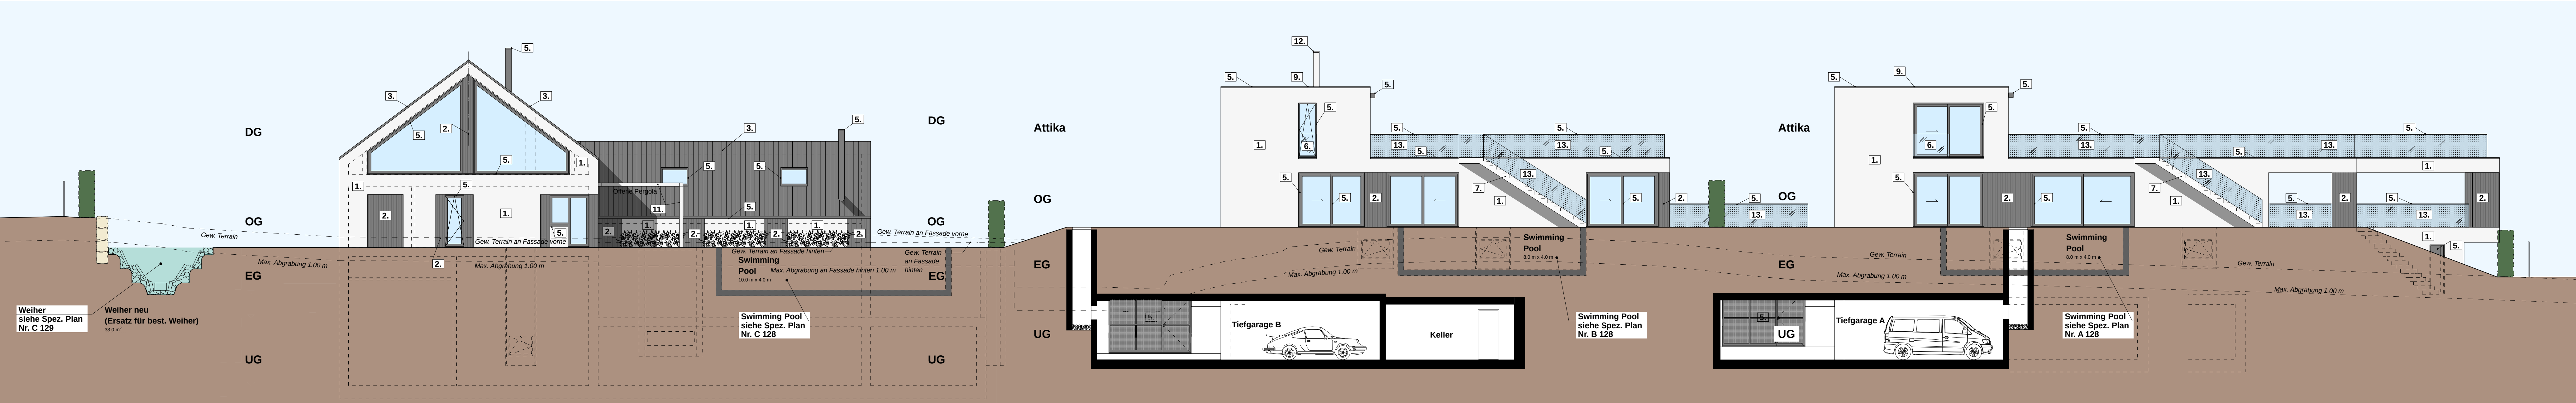


Nordseite Haus C-B-A

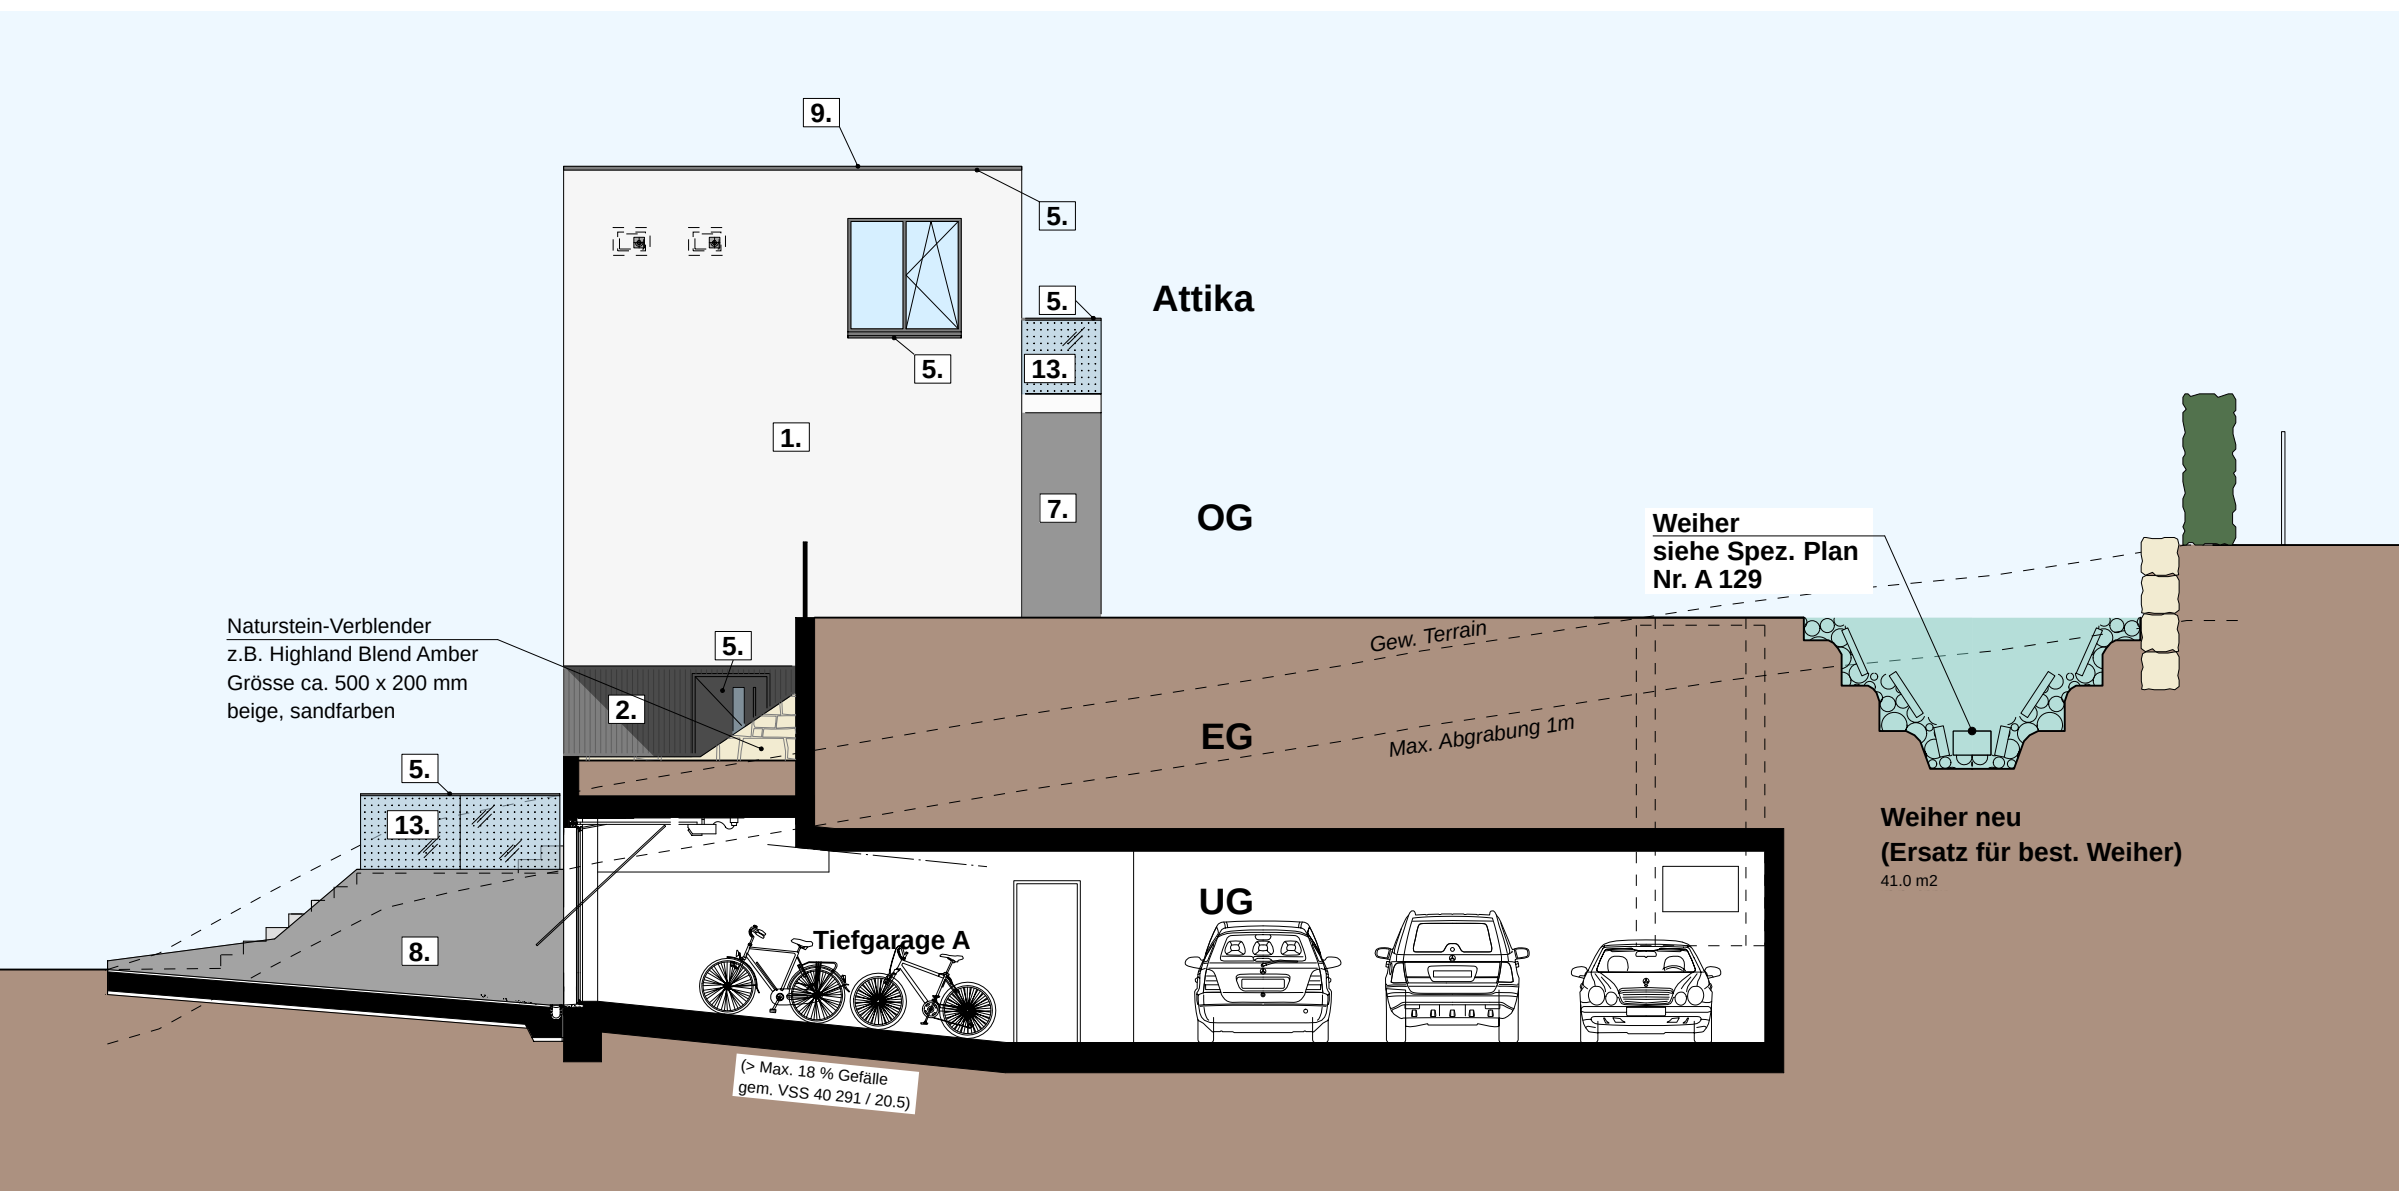


Ostseite Haus A

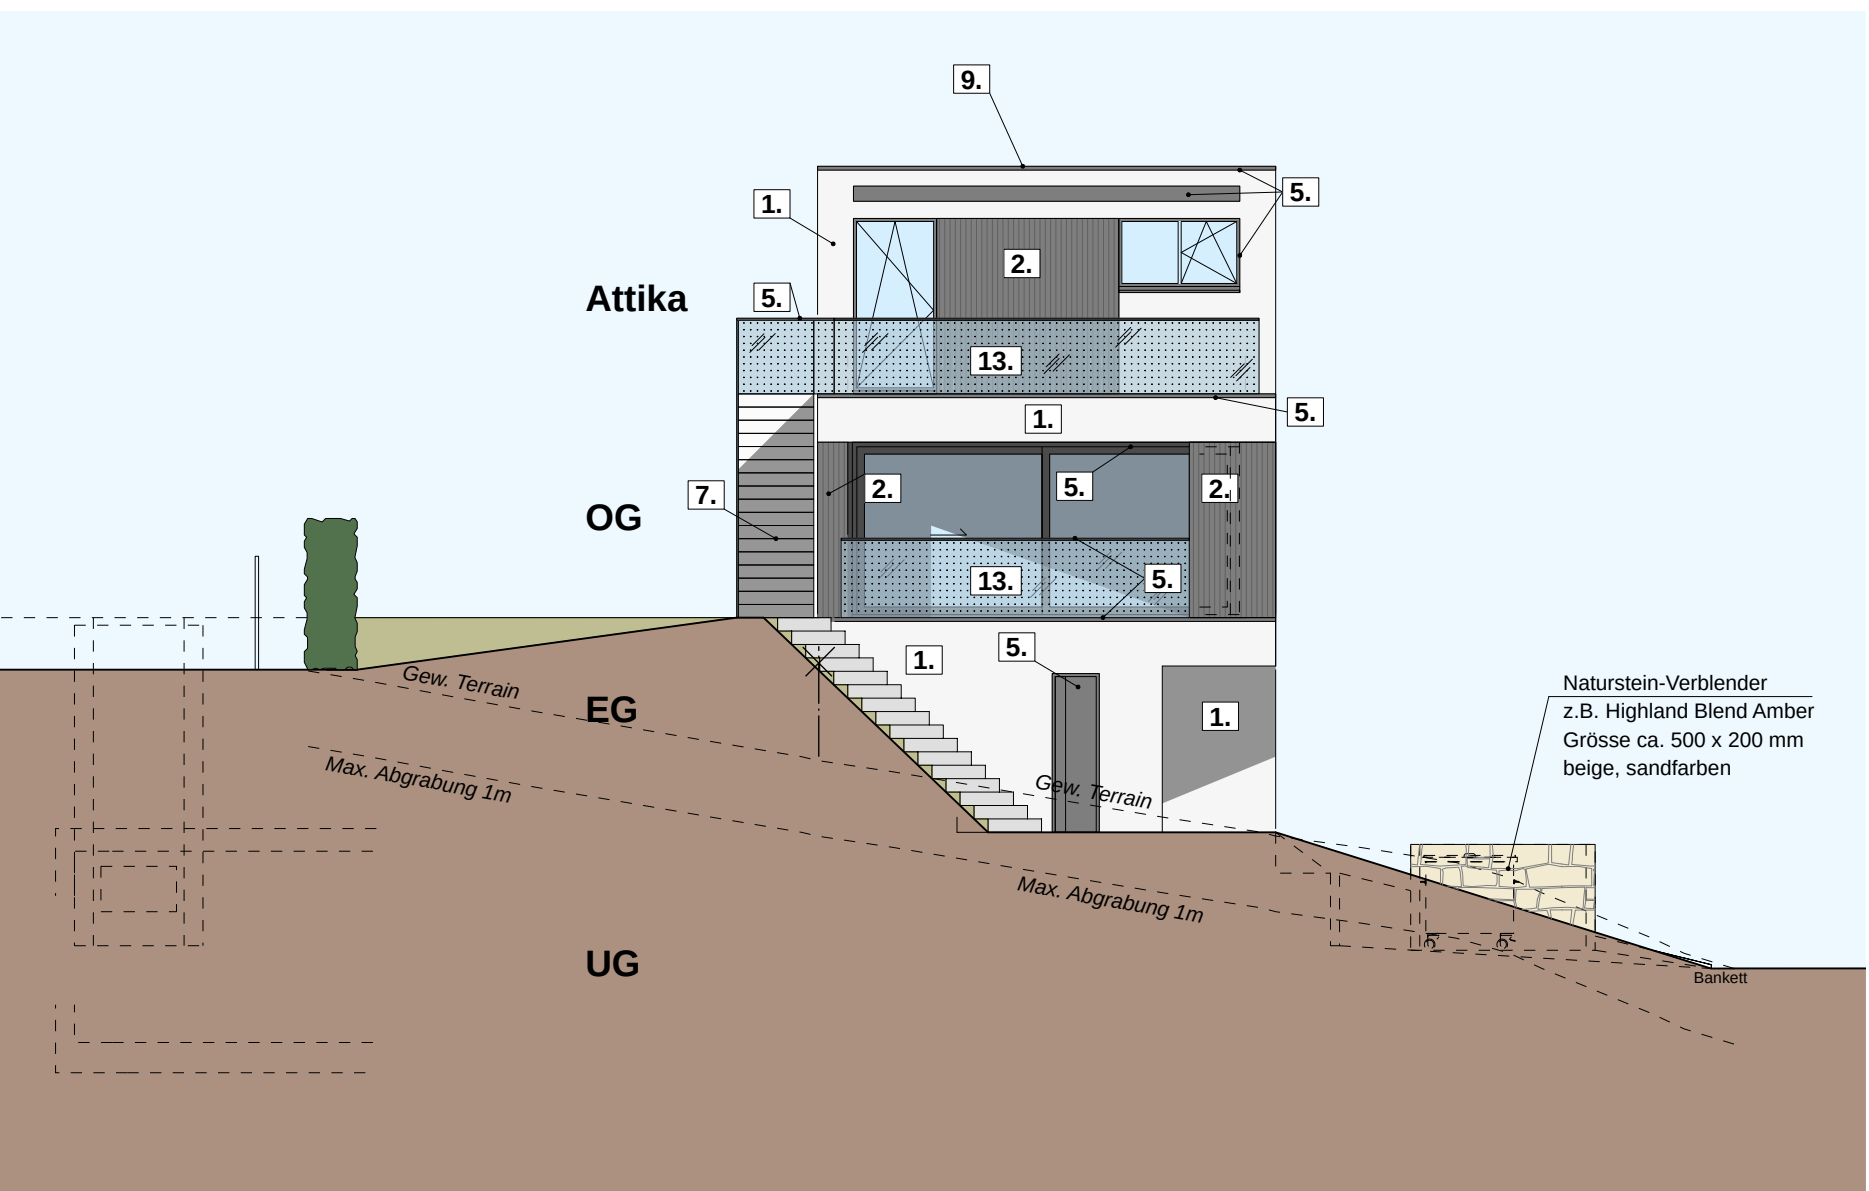

Westseite Haus A

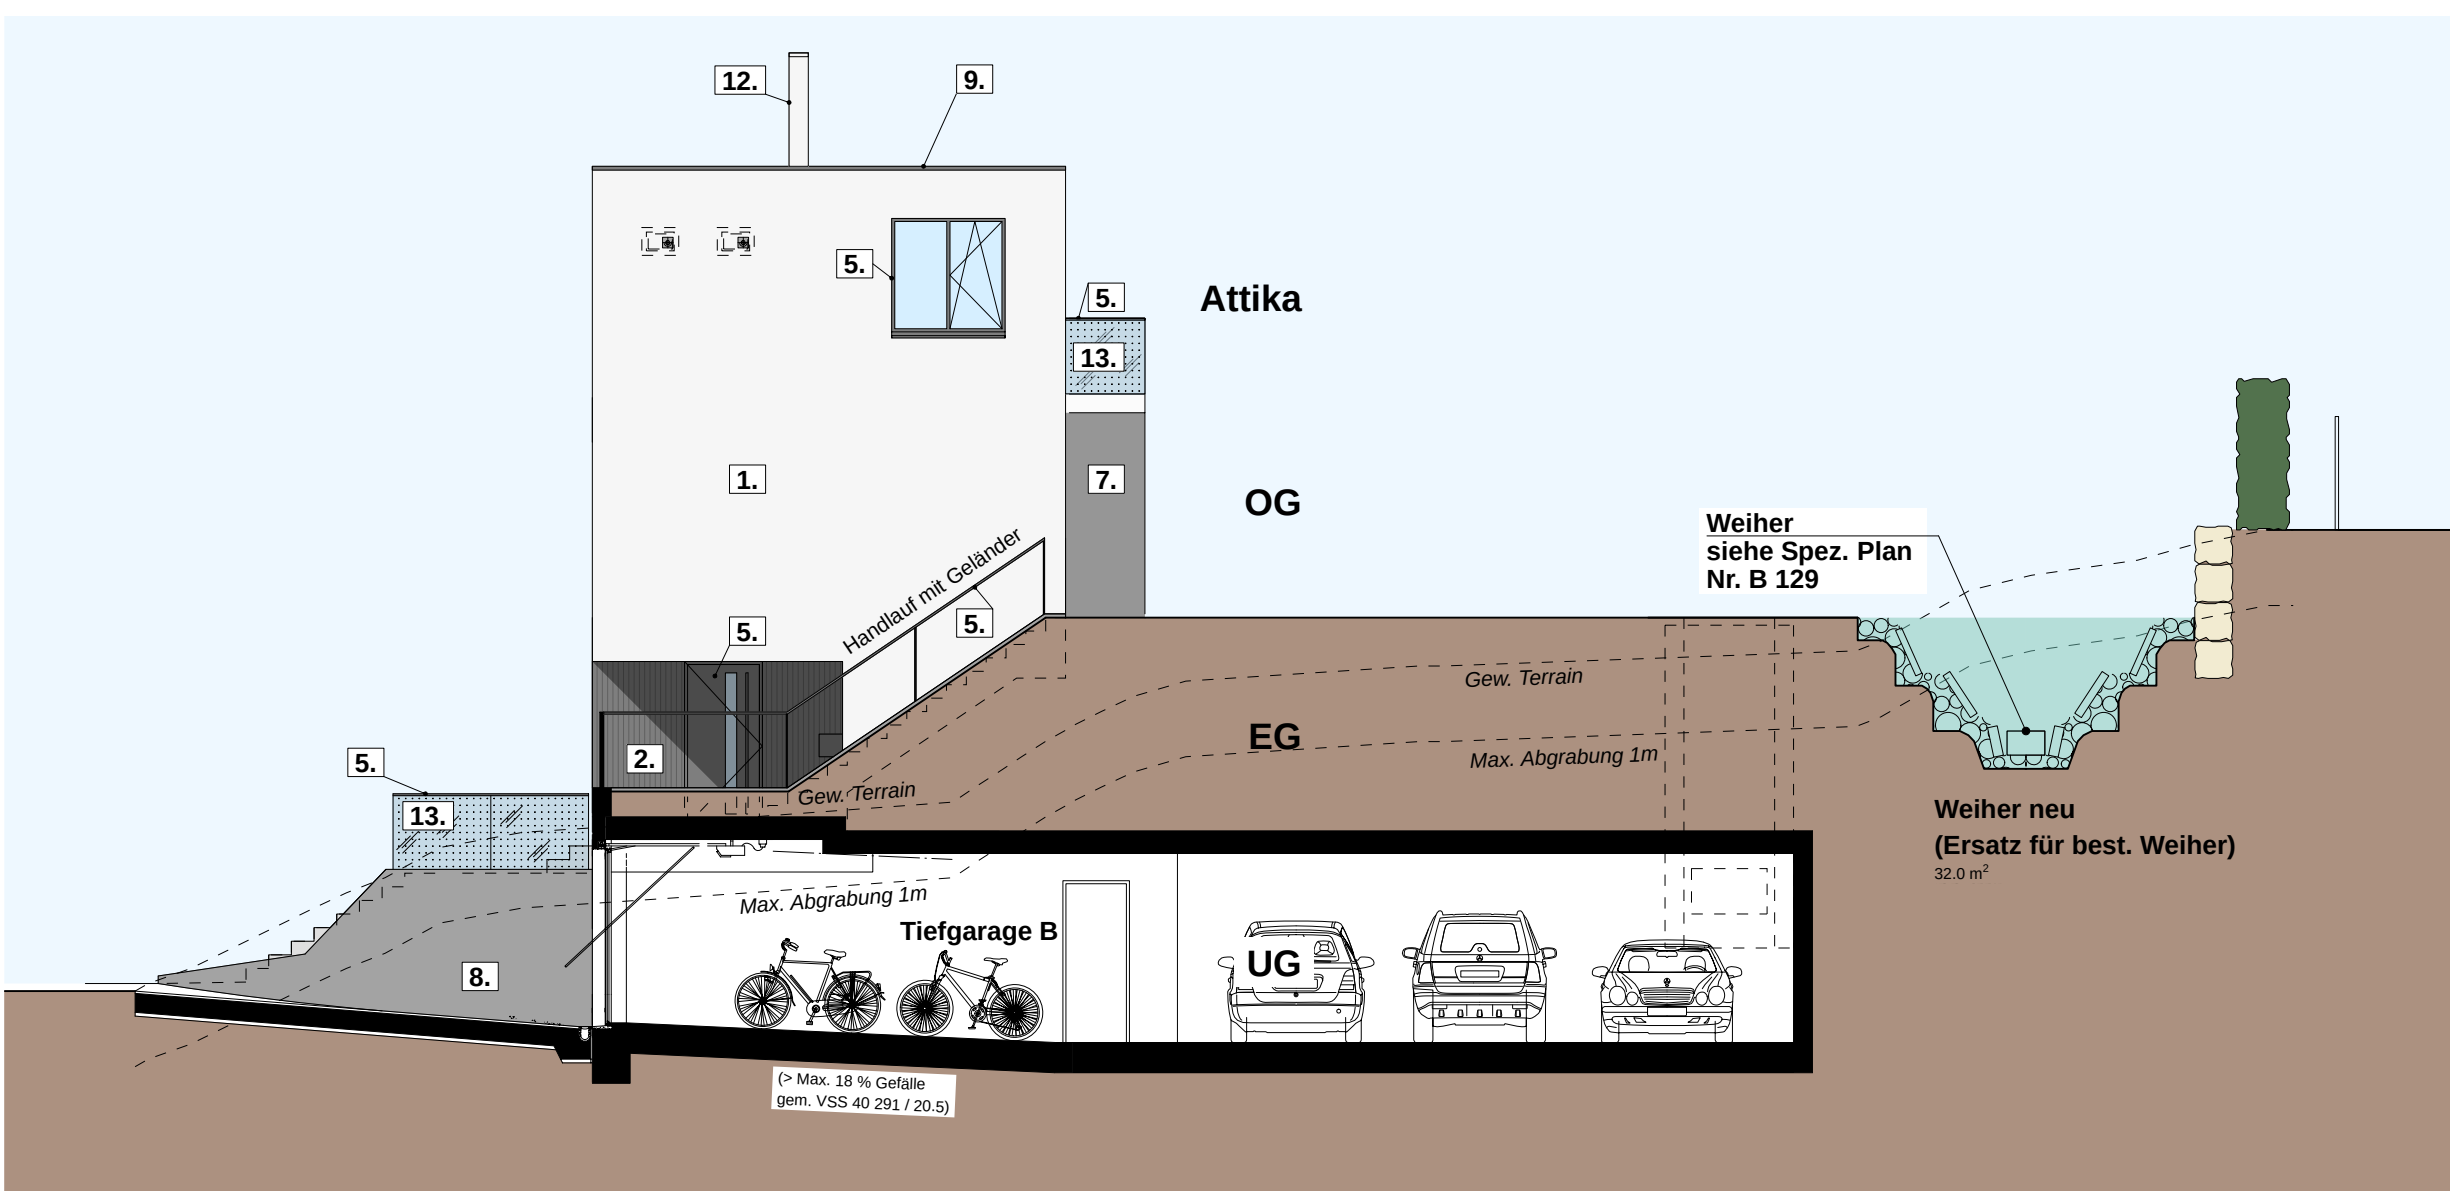

Ostseite Haus B

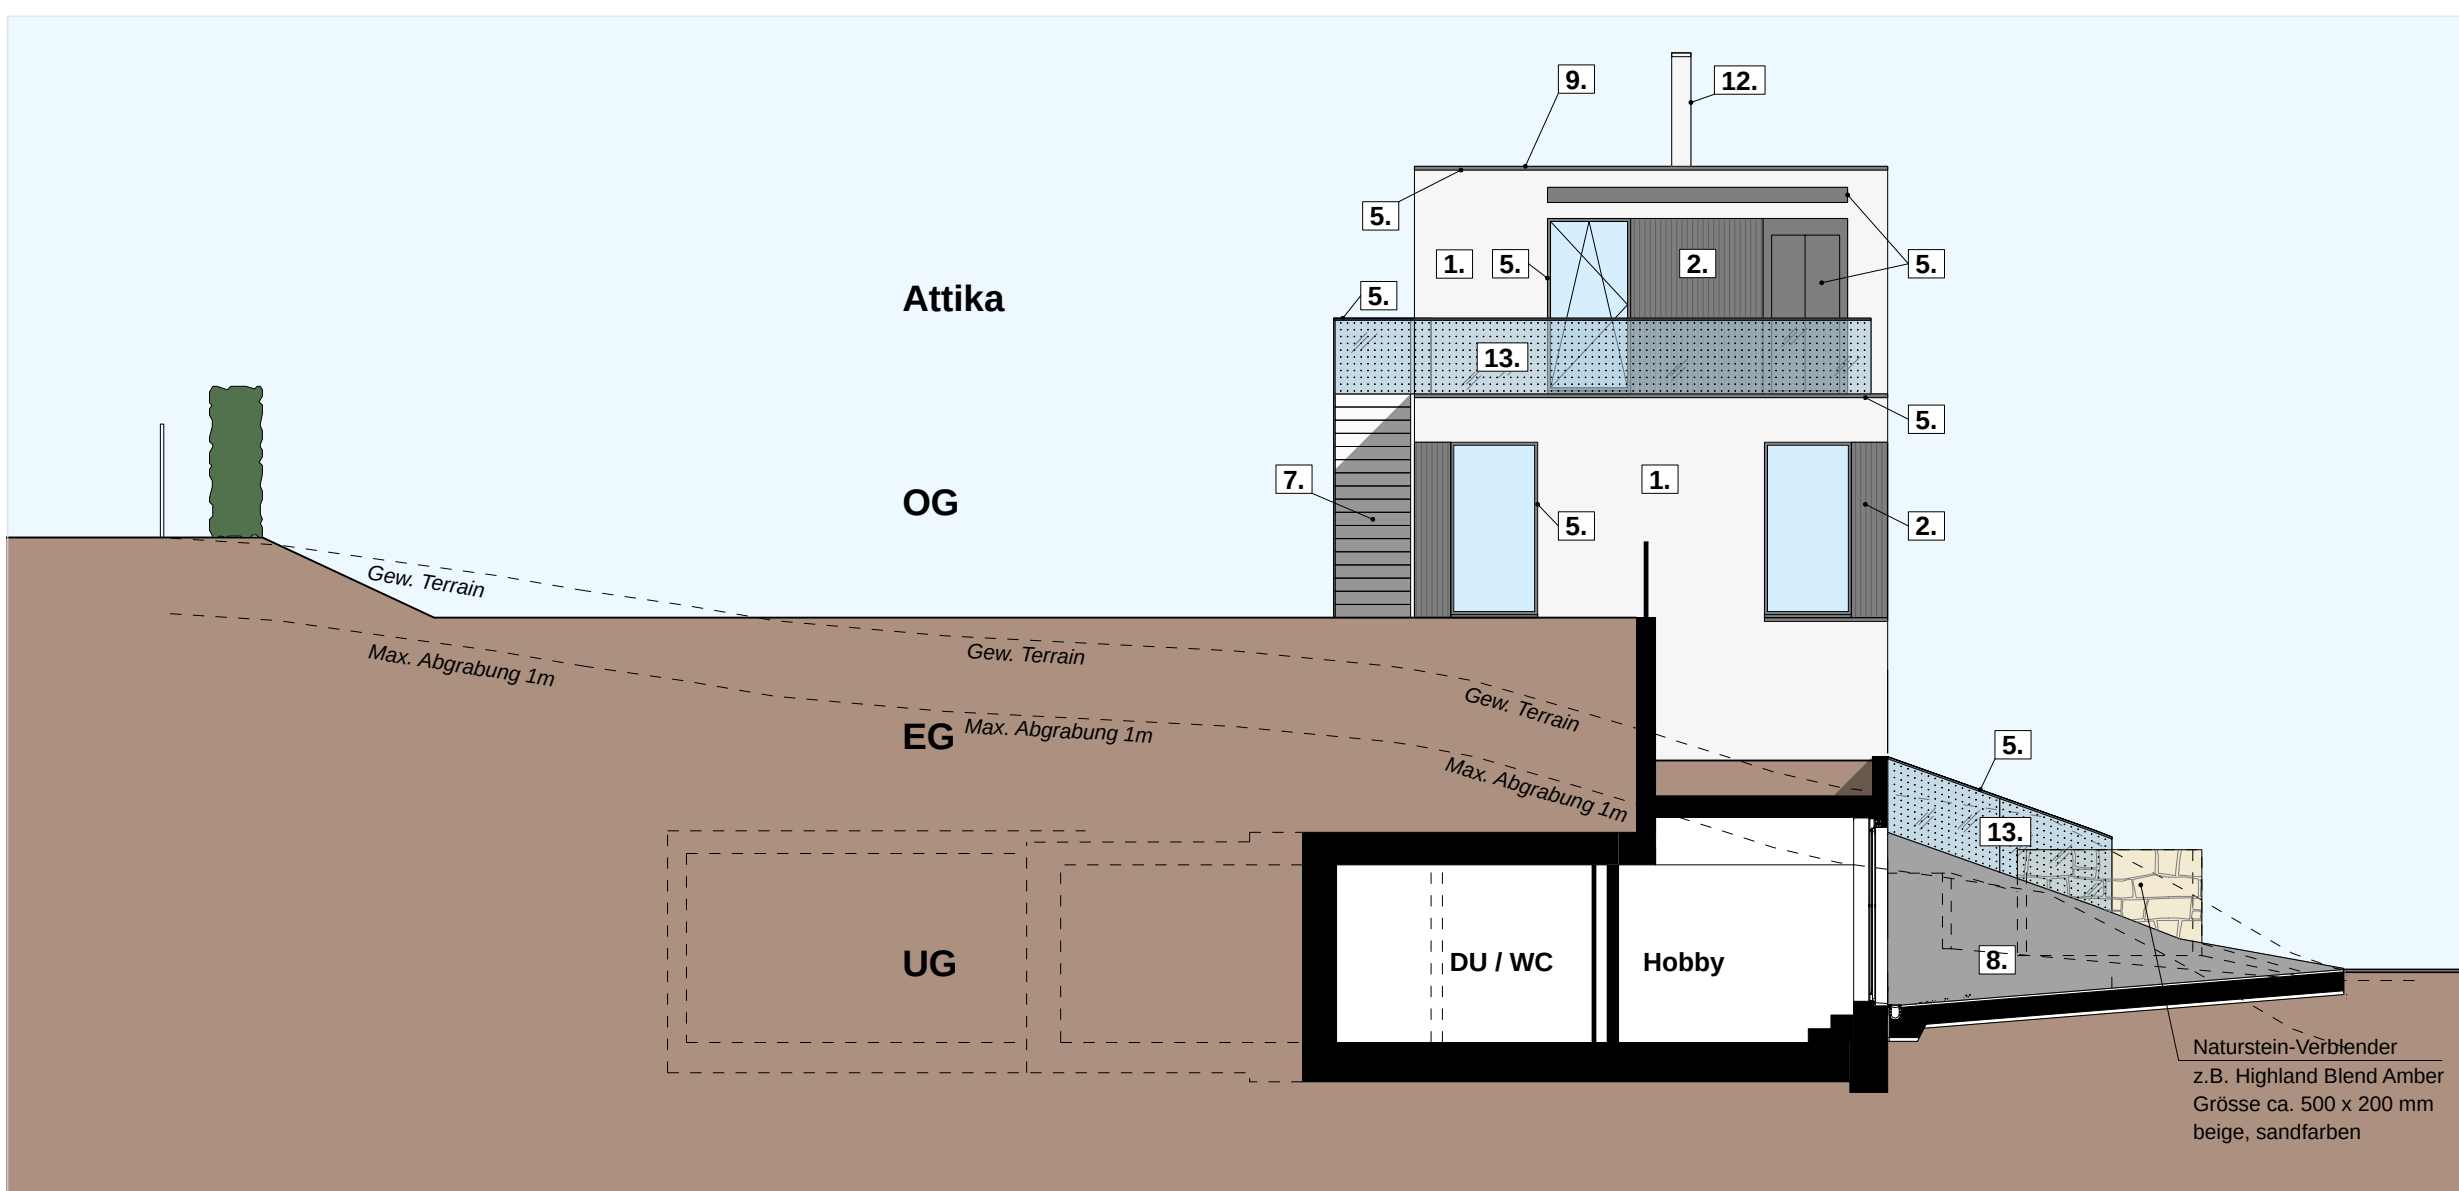

Westseite Haus B

Legende:

- Hauptfläche Fassade - verputzte Aussenwärmedämmung Abrieb 1.5mm
- Metallfassaden-Element - Montana Trapezblech Aluminium teil-geölt
- Glatte Ziegel engobiert - Creaton Domino
- Fenster in Holz-Metall

NCS S 0500-N

schwarz metallisé

schwarz matt

RAL 790-M Effects

- Alle Metallbauteile wie: Fensterbänke, Hauseingangstüren, Briefkästen, Kassettenmarkisen, Lamellenstoren und Führungsschienen, Garagentor, Flachdach-/ Terrassenabschlüsse Spenglerblech, Abschluss U-Profil bei Glasgeländern (Terrassen & Loggien)
- Absturzsicherung vor Fenster

RAL 790-M Effects

Glasbrüstung (Klarglas)
VSG Verbundsicherheitsglas

- Wange Aussentreppe lackiert
- Sichtbeton lasiert, Stocryl V400/V450 Lasur mit
- PV-Anlage
- Balkon-Stirne und Stützen in Metall, pulverbeschichtet

NCS S 0500-N

RAL 790-M Effects


NCS S 0500-N

- Offene Pergola in Metall, pulverbeschichtet
- Kamin in Metall, weiss


NCS S 0500-N

NCS S 0500-N

- VSG Verbundsicherheitsglas, beidseitig reflektive Variante SEEN Shiny dual, Punktraster, Ø 9 mm, Abstand 90 mm, Vogelschutz wird dadurch gewährleistet. Diese Variante wurde von der Biologischen Station Hohenau mit lebenden Vögeln im Flugkanal geprüft und als «hoch effizient» taxiert. Wir können die Verwendung dieser Markierung empfehlen. Bestätigung durch Vogelwarte Sempach Furrer, 30.09.2024.

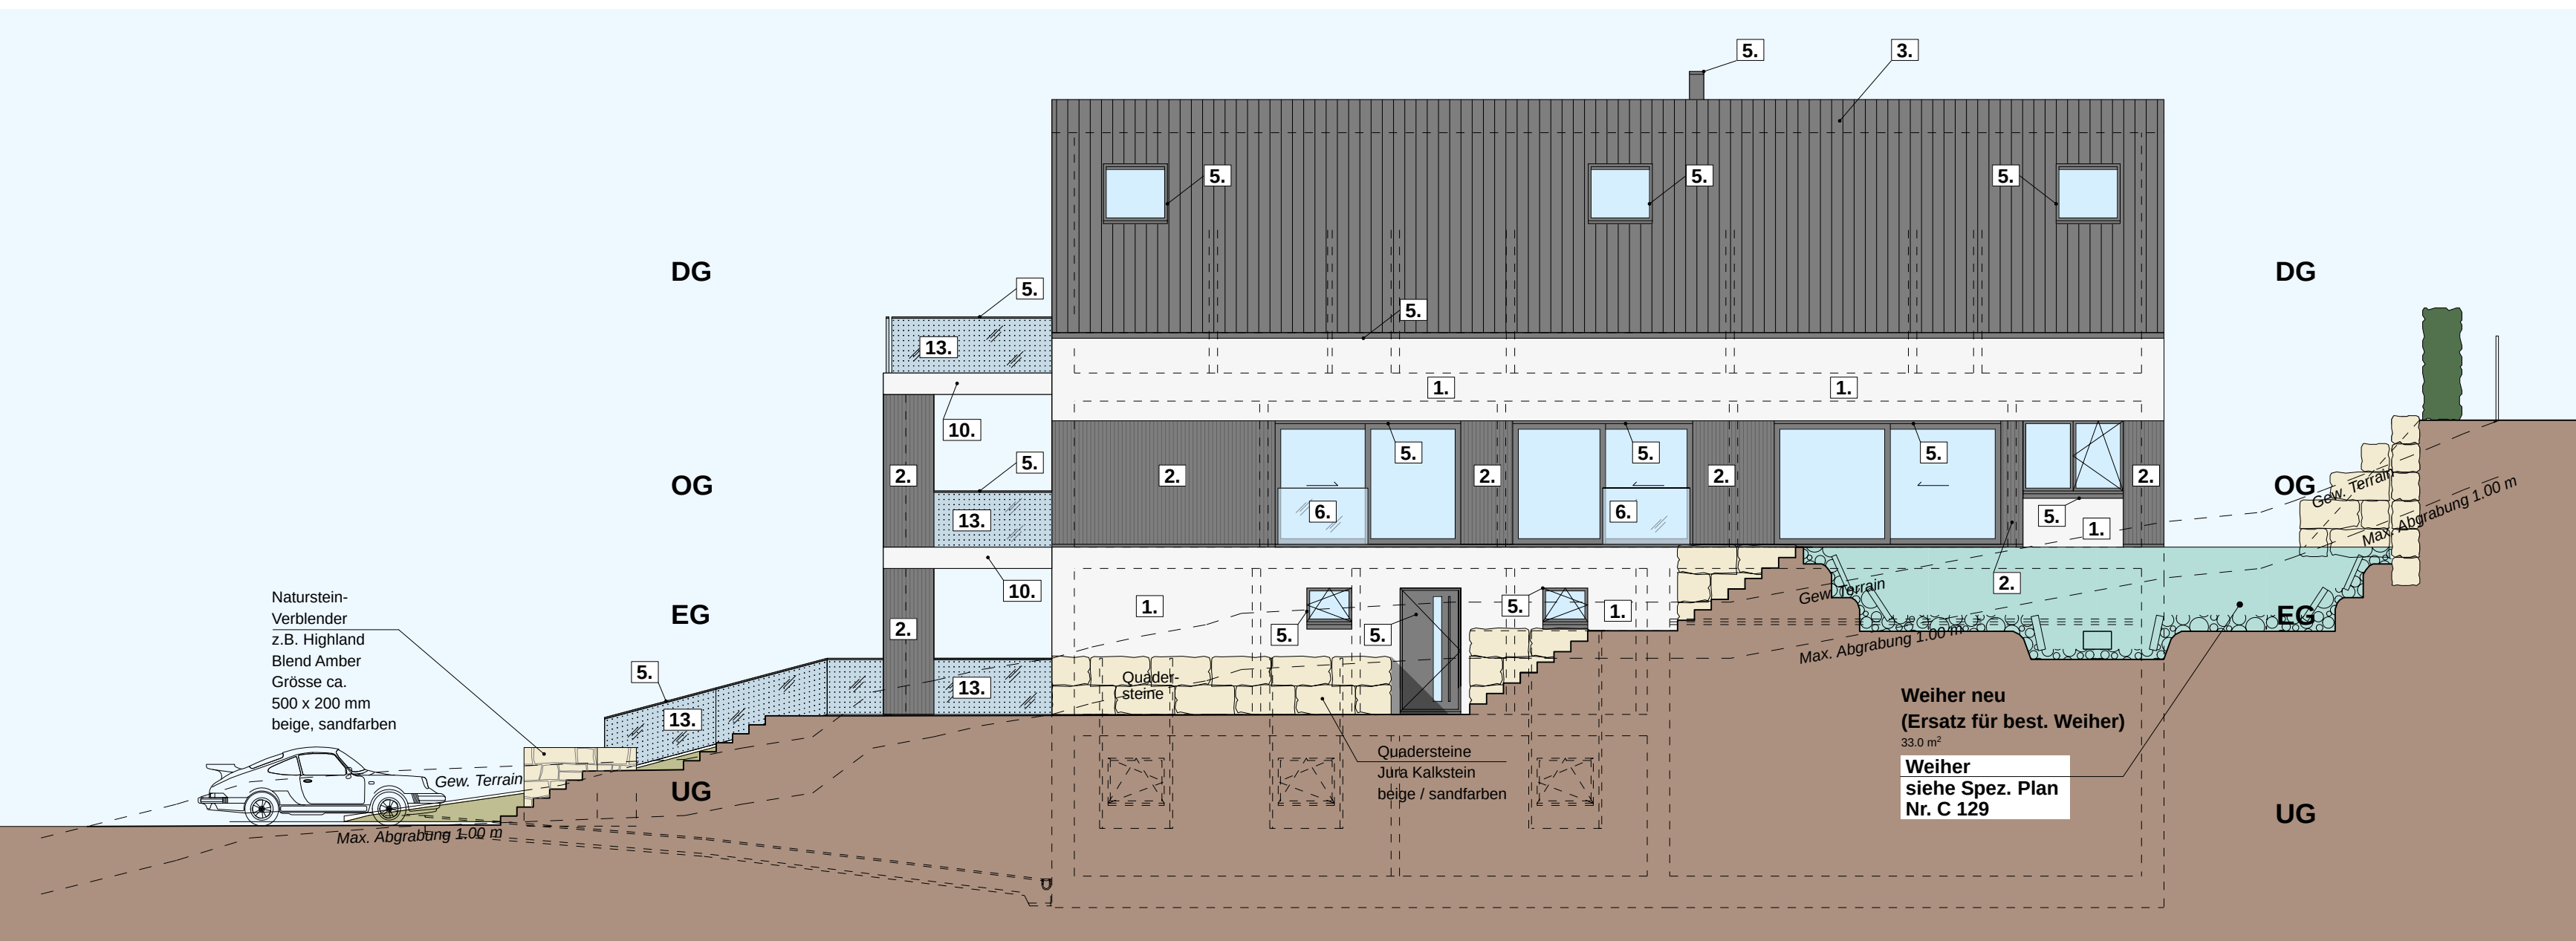

Ostseite Haus C

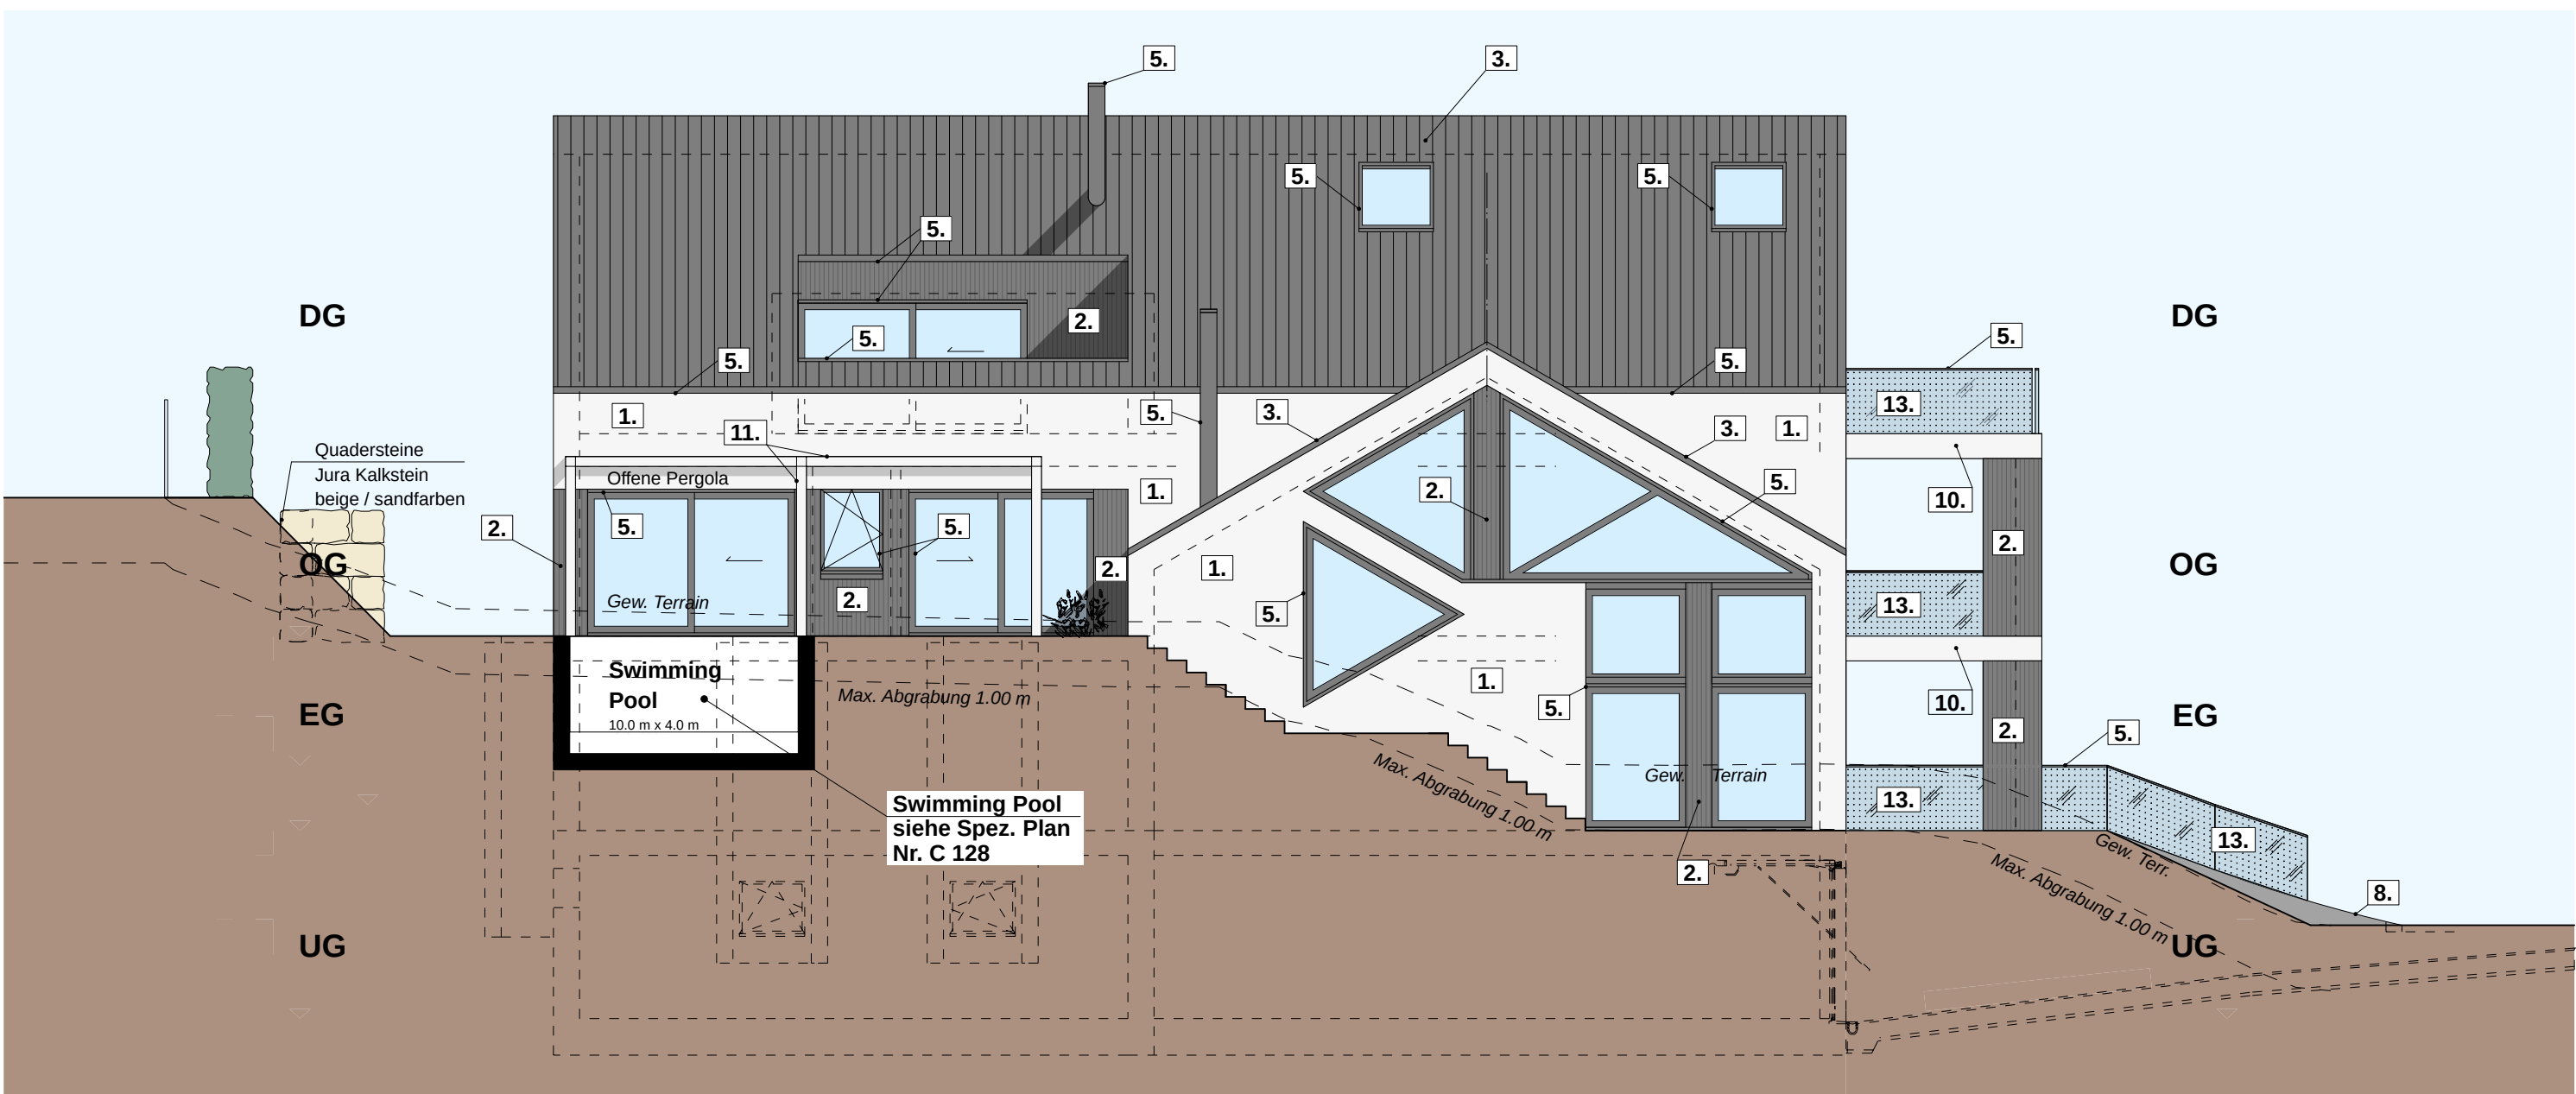

Westseite Haus C

Projektverfasser:

dw design & concept ag
Haldenstrasse 106
8620 Wetzikon

Unterschrift Projektverfasser

Bauherr / Grundeigentümer:

dw Immobilien ag
Haldenstrasse 106
8620 Wetzikon

Unterschrift Bauherr / Grundeigentümer

±0.00 = 717.60 m ü.M (OK Fertigbelag EG Haus A und B)

Alle Masse sind vom Unternehmer vor der Ausführung am Bau zu nehmen, bzw. zu kontrollieren. Abfällige Differenzen sind unverzüglich mit der Bauleitung zu klären. Falls nicht anders vermerkt sind die Feisschichten von OK fertig Boden bis UK Sturz gemessen. Türhöhen sind von OK fertig Boden oder Schwelle bis UK roher Sturz gemessen.

Index	Datum	Geändert von	Änderung
A	13.02.2023	MDS	Planzusammenfassung / Baugestaltung Haus C Format angepasst.
B	26.07.2023	MDS	Einzelblätter in Dg bei Terrassen Haus A angepasst. Massnahmen bei Stützen domestisch verändert. Planzusammenfassung / Haus B angepasst, gelistet und 3 m zu Haus A verschoben. Ein Teil der Stützenmauern wurden mit Natursteinverblender eingeklinkert.
C	27.02.2024	MDS	Einzelblätter und Planblätter angepasst, Kaminhöhe korrigiert.
D	26.04.2024	MDS	Terrassenhöhe ergänzt, Hecke, Pool und Stütze ergänzt, Vergr. Terrassen gem. Uggelie Sempach.
E	02.10.2024	MDS	Vergr. Terrassenhöheänder mit beidseitig reflektiven Variante SEEN Shiny dual ersetzt.

BAUVORHABEN: Überbauung Zumikon

ADRESSE: Haldenstrasse 5, 8126 Zumikon
Parzelle 2999

dw design & concept

dw design & concept ag
Haldenstrasse 106
8620 Wetzikon

Tel: +41 (0)43 477 44 33

info@dw-dc.ch

www.dw-dc.ch

Phase

ESG

Plannummer

Planinhalt

Plangröße

Name

gezeichnet

geprüft

freigegeben

BAUFREIGABE

117E

Revidiertes Farz - und Materialkonzept Fassaden Haus A, B, C

1300x900

Datum

Maßstab

1:100